
Схема расположения колонн на отм. +0,320 (1:50)

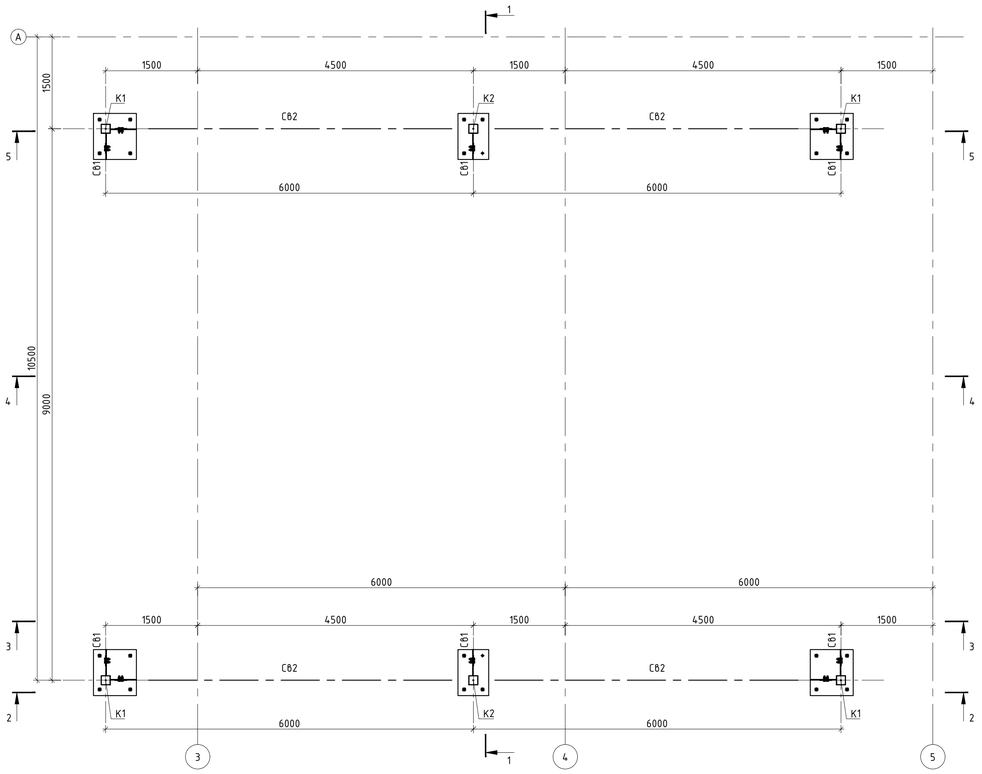


Спецификация элементов металлопроката

Наименование профиля ГОСТ, ТУ	Наименование или марка металла ГОСТ, ТУ	Номер или размер профиля, мм	Поз.	Марка металла по элементам конструкций, т				Общая масса, т
				Колонны	Распорки, стойки, связи	Профлист		
Профили стальные гнутые замкнутые сварные квадратные и прямоугольные ГОСТ 30245-2003	С245 ГОСТ 27772-15	50х50х3	1		2,03			2,03
		150х150х5	2	1,07	1,76			2,83
	Итого:		3	1,07	3,79			4,86
Профили стальные листовые гнутые с трапециидальными формами по ГОСТ 24045-2016	Ст3пс ГОСТ 10704-91	Н75-750-0,7	4			1,13		1,13
		С10-1000-0,7	5			0,89		0,89
	Итого:		6			2,02		2,02
Сталь листовая горячекатаная, по ГОСТ 19903-2015	С245 ГОСТ 27772-15	t=4	7		0,50			0,50
		t=8	8	0,13	0,17			0,30
		t=10	9	0,05	0,05			0,10
		t=20	10	0,42				0,42
	Итого:		11	0,60	0,72			1,32
Всего масса металла			12	1,67	4,51	2,02		8,20

*Примечание: спецификация элементов металлопроката составлена на листы 2-4 комплекта - ЈО1-24207-КМ

Ведомость элементов

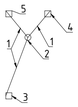Марка	Сечение: Эскиз	Поз.	Состав	Усилие для прикрепления: М, кНм	N, кН	Q,кН	Группа констр.	Марка стали	Примечания
К1		1	150х150х5				1	С245	
		2	-10х240х400					С245	
		3	-20х700х700					С245	
К2		1	150х150х5					С245	
		2	-10х240х400					С245	
		3	-20х700х1000					С245	
С81		1	150х150х5					С245	
С82		1	150х150х5					С245	
		2	-8хФ250					С245	
		3	-8х300х425					С245	
		4	-8х250х630					С245	
		5	-8х260х260					С245	
С83		1	50х50х5					С245	
С84		1	50х50х5					С245	
Сл1		1	50х50х5					С245	
Сл2		1	50х50х5					С245	
Р1		1	50х50х5					С245	
Р2		1	50х50х5					С245	
Рс1		1	50х50х5					С245	
Ст1		1	50х50х5					С245	
Нс1		1	Н75-750-0,7					Ст3пс	
Пл1		1	С10-1000-0,7					Ст3пс	

*Примечание: ведомость элементов составлена на листы 2-4 комплекта - ЈО1-24207-КМ

Схема расположения конструкций на отм. +8,070 (1:50)


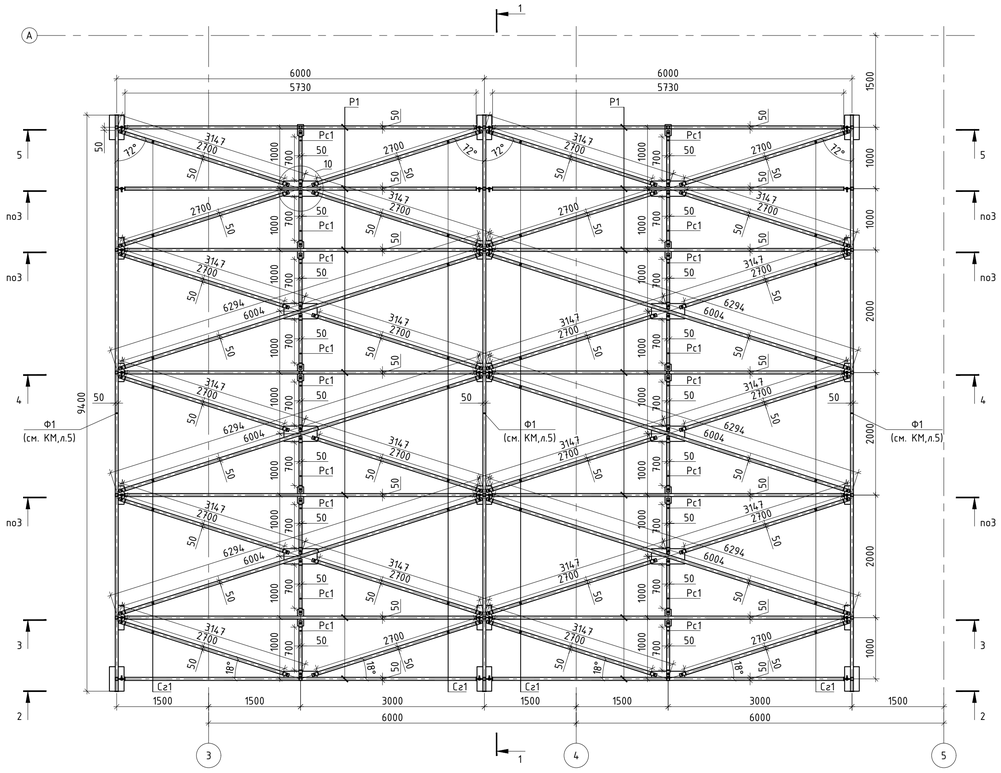


Схема расположения конструкций на отм. +8,900...+10,345 (1:50)
(Разрез 6-6)

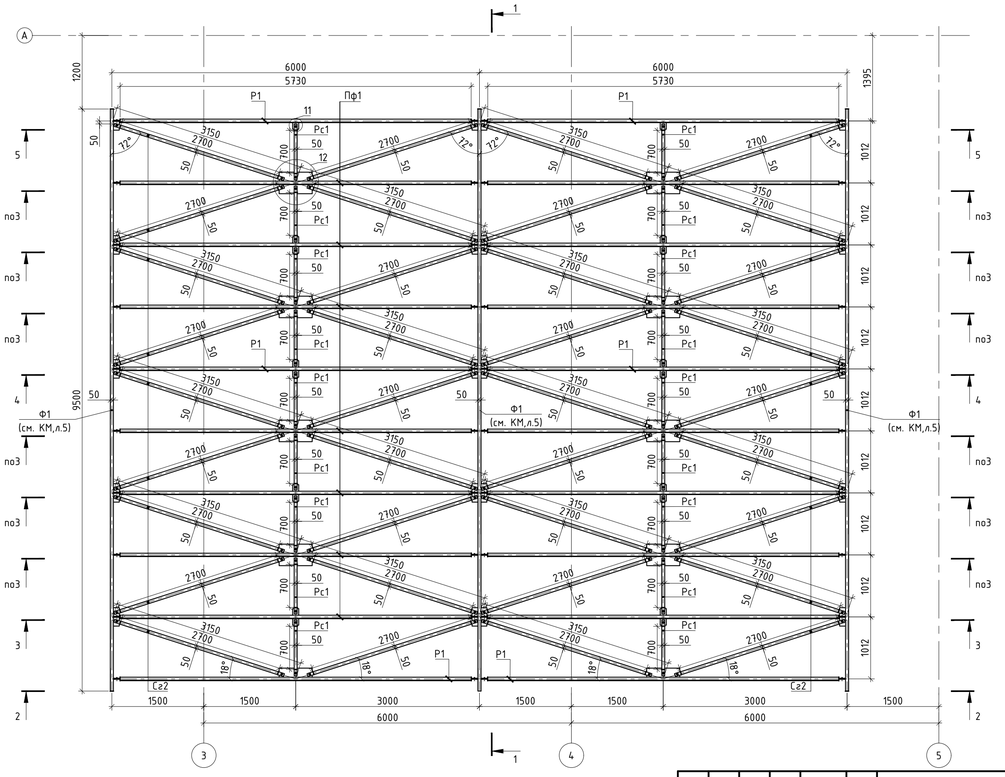

Согласовано

Взам. инв. №

Подп. и дата

Инв. № подл.

Изм.	Кол. уч.	Лист	№ док.	Подп.	Дата
ГИП					
Разраб.		Андреев			

ЈО1-24207-КМ

-

Стадия	Лист	Листов
Р	2	

Схема расположения колонн на отм. +0,320.
Схема расположения конструкций на отм. +8,070.
Схема расположения конструкций на отм. +8,900...+10,345. Ведомость элементов. Спецификация металлопроката