


8
3
(1:5)

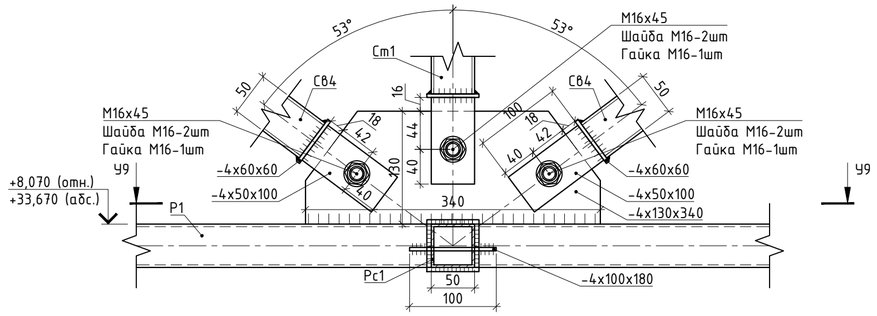


-4x130x340 (1:5)

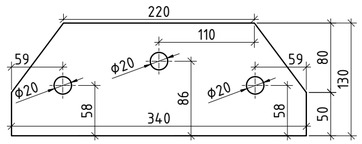


У9-У9 (1:5)

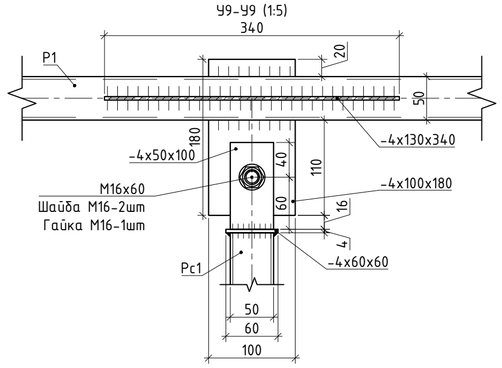


10
3
(1:5)

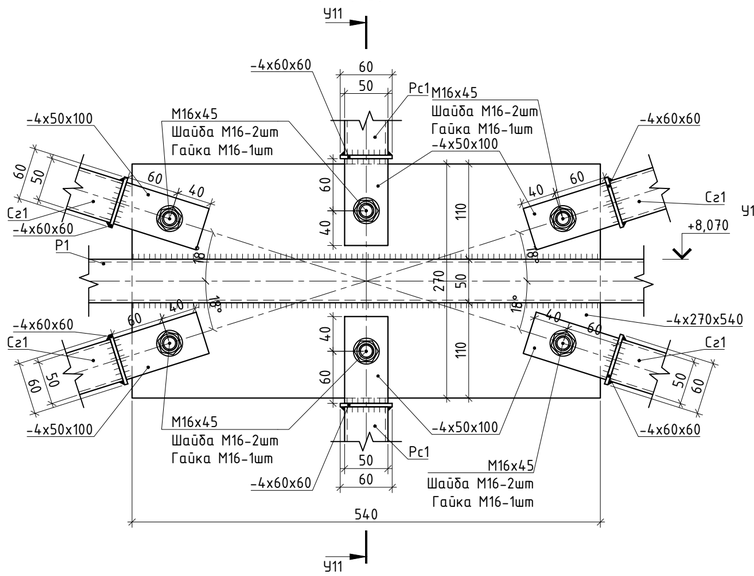

У11-У11 (1:5)

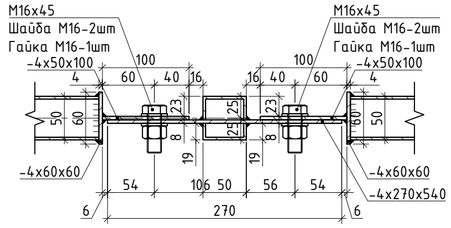


9
3
(1:5)

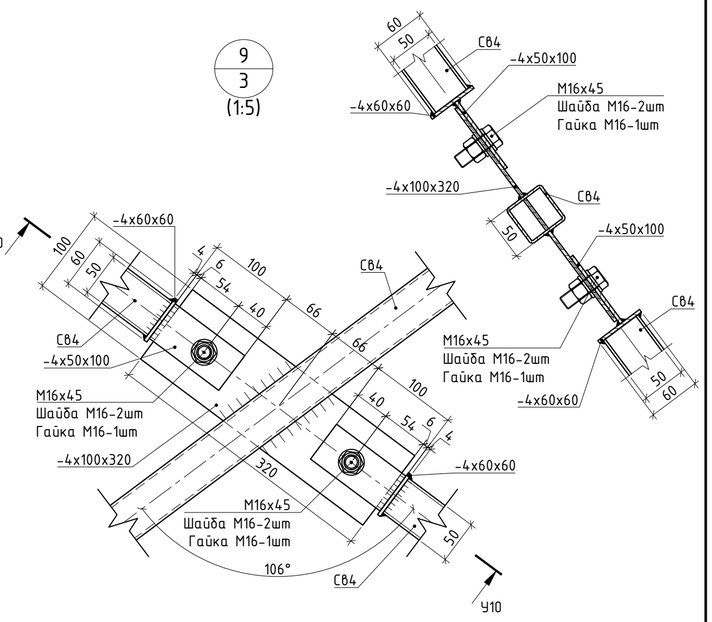


У10-У10 (1:5)

12
3
(1:5)

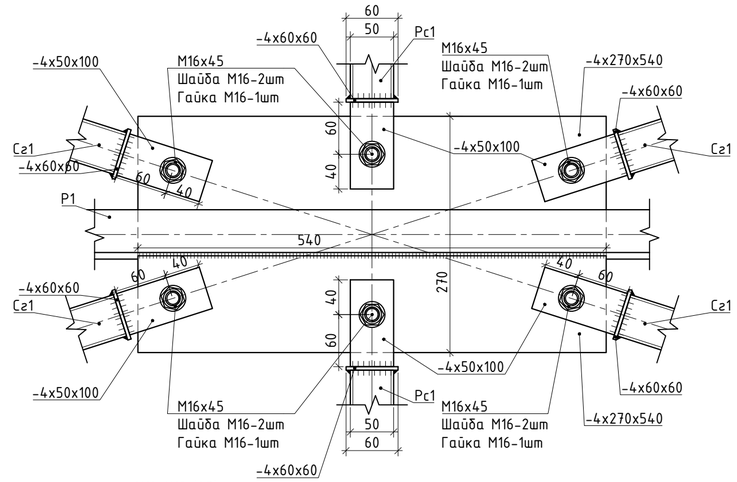


-8x145x180 (1:5)


13
3
(1:5)

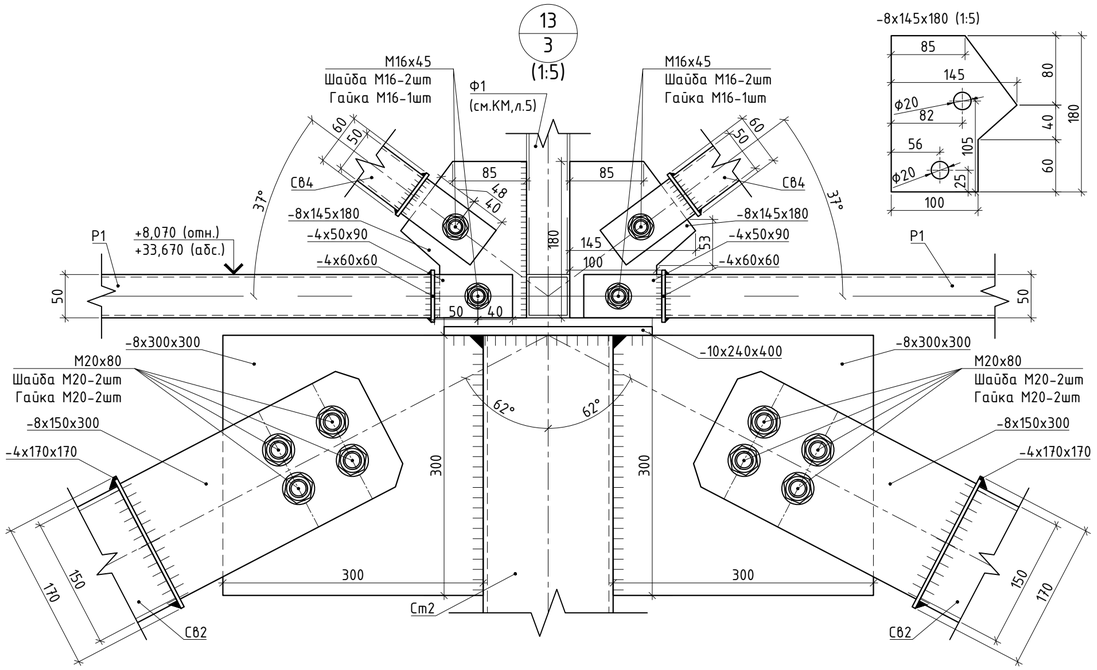

11
3
(1:5)

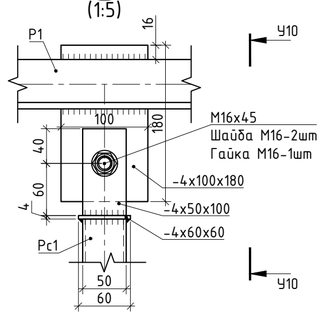

У10-У10 (1:5)

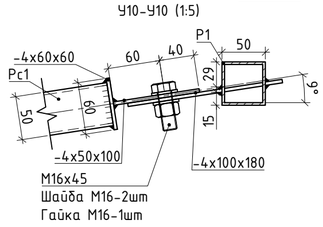

Согласовано

Взам. инв. №

Подп. и дата

Инв. № подл.

						J01-24207-КМ
Изм.	Кол. уч	Лист	№ док.	Подп.	Дата	
ГИП						–
Разраб.		Андреев				
Н. контр.						Узлы 8, 9, 10, 11, 12, 13

Стадия	Лист	Листов
Р	4	