Ферма Ф1 (1:10)

А
1:2

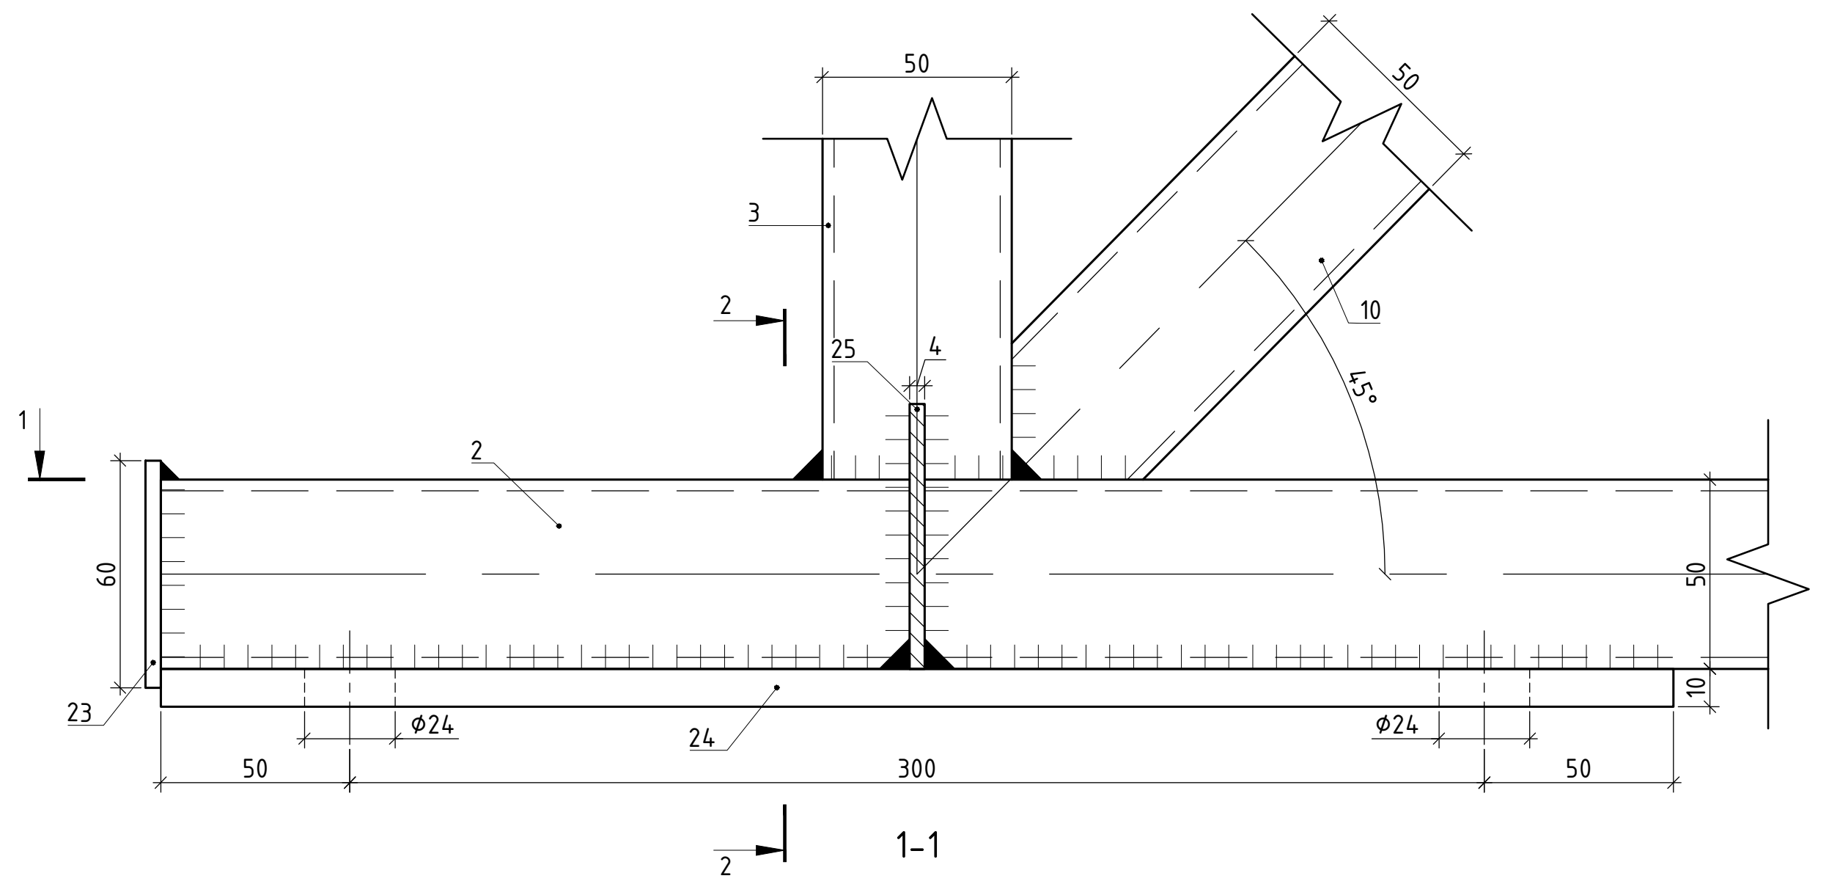

2-2

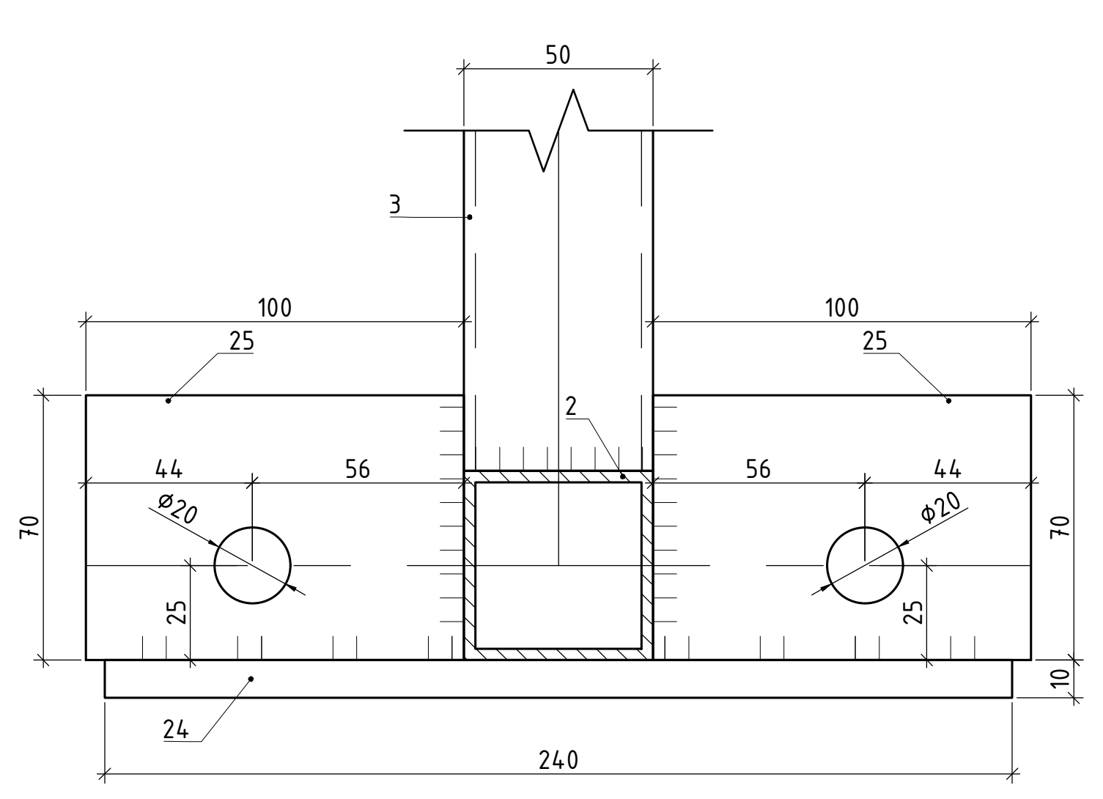

1-1

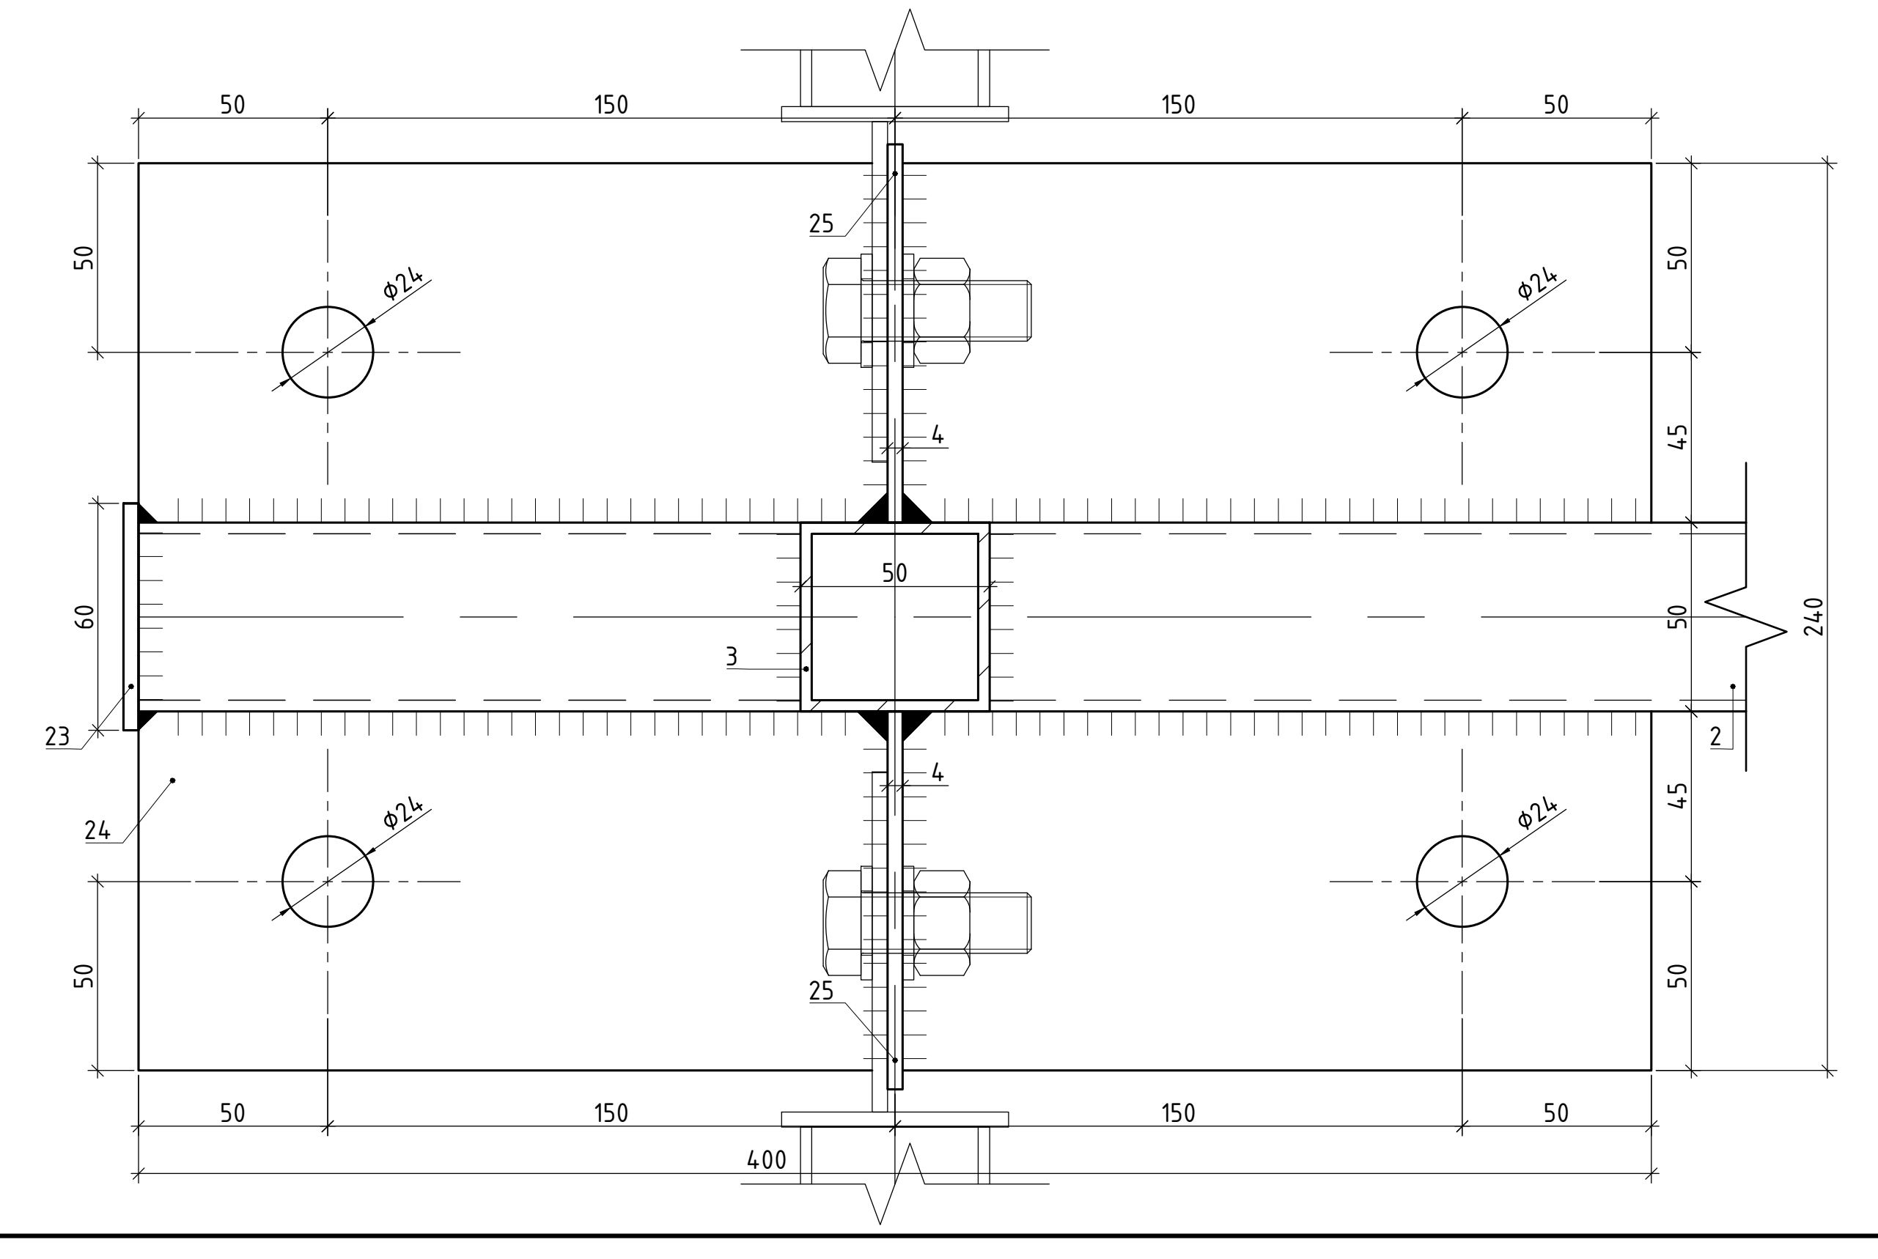

Б
1:2

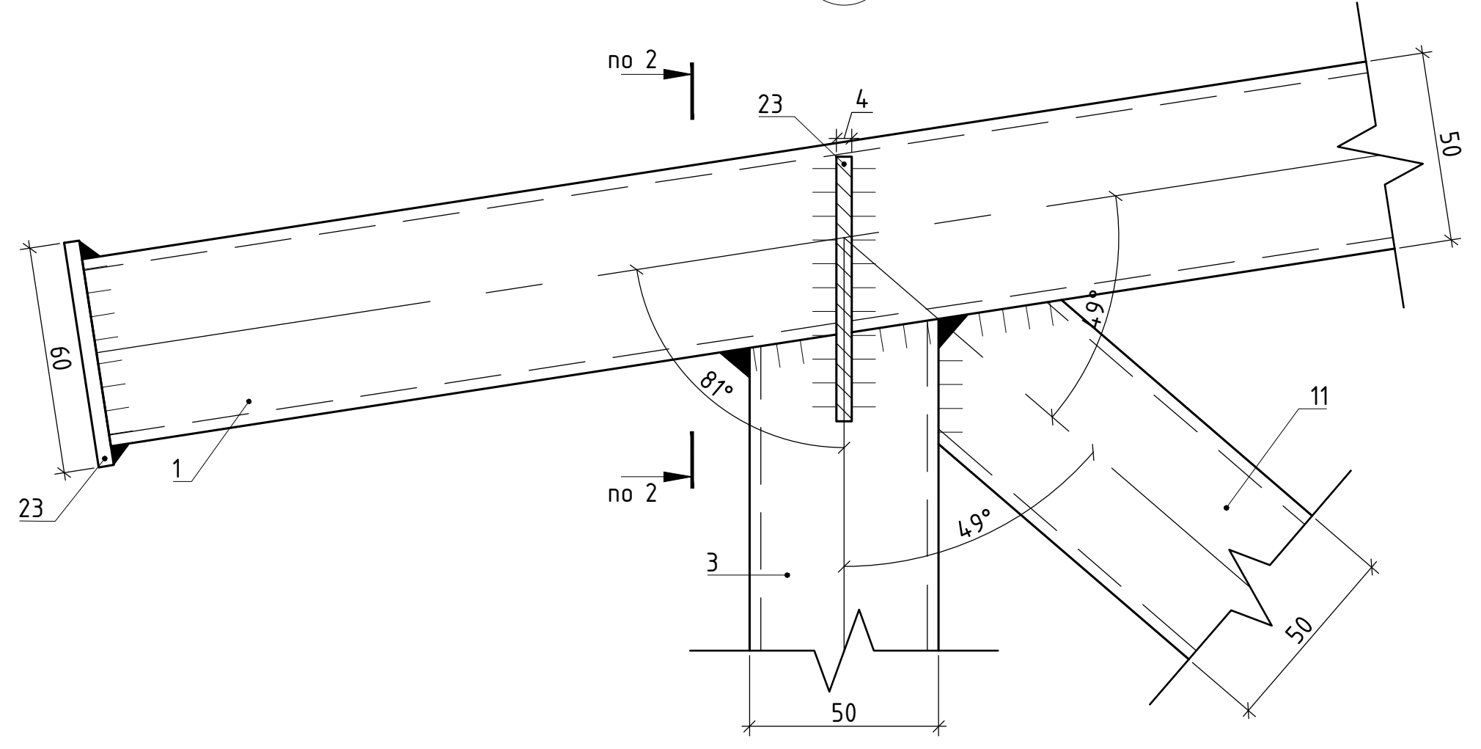

В
1:2

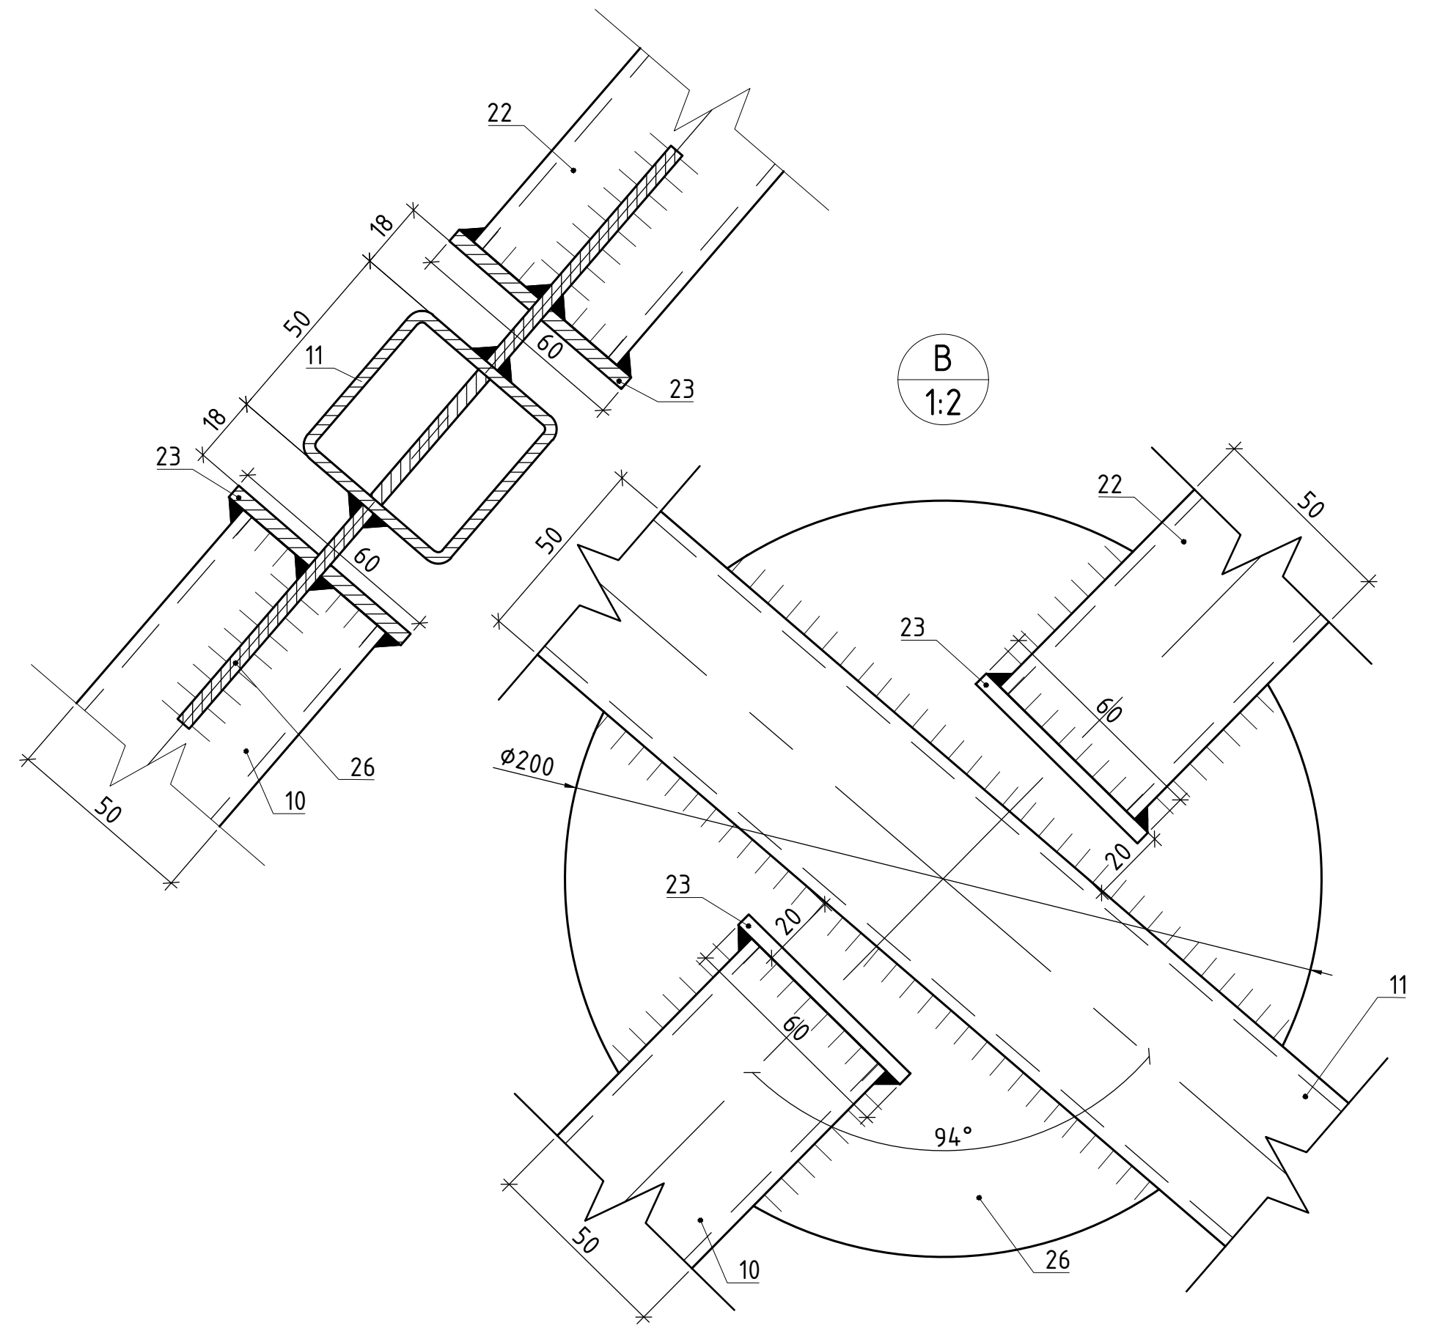

Г
1:2

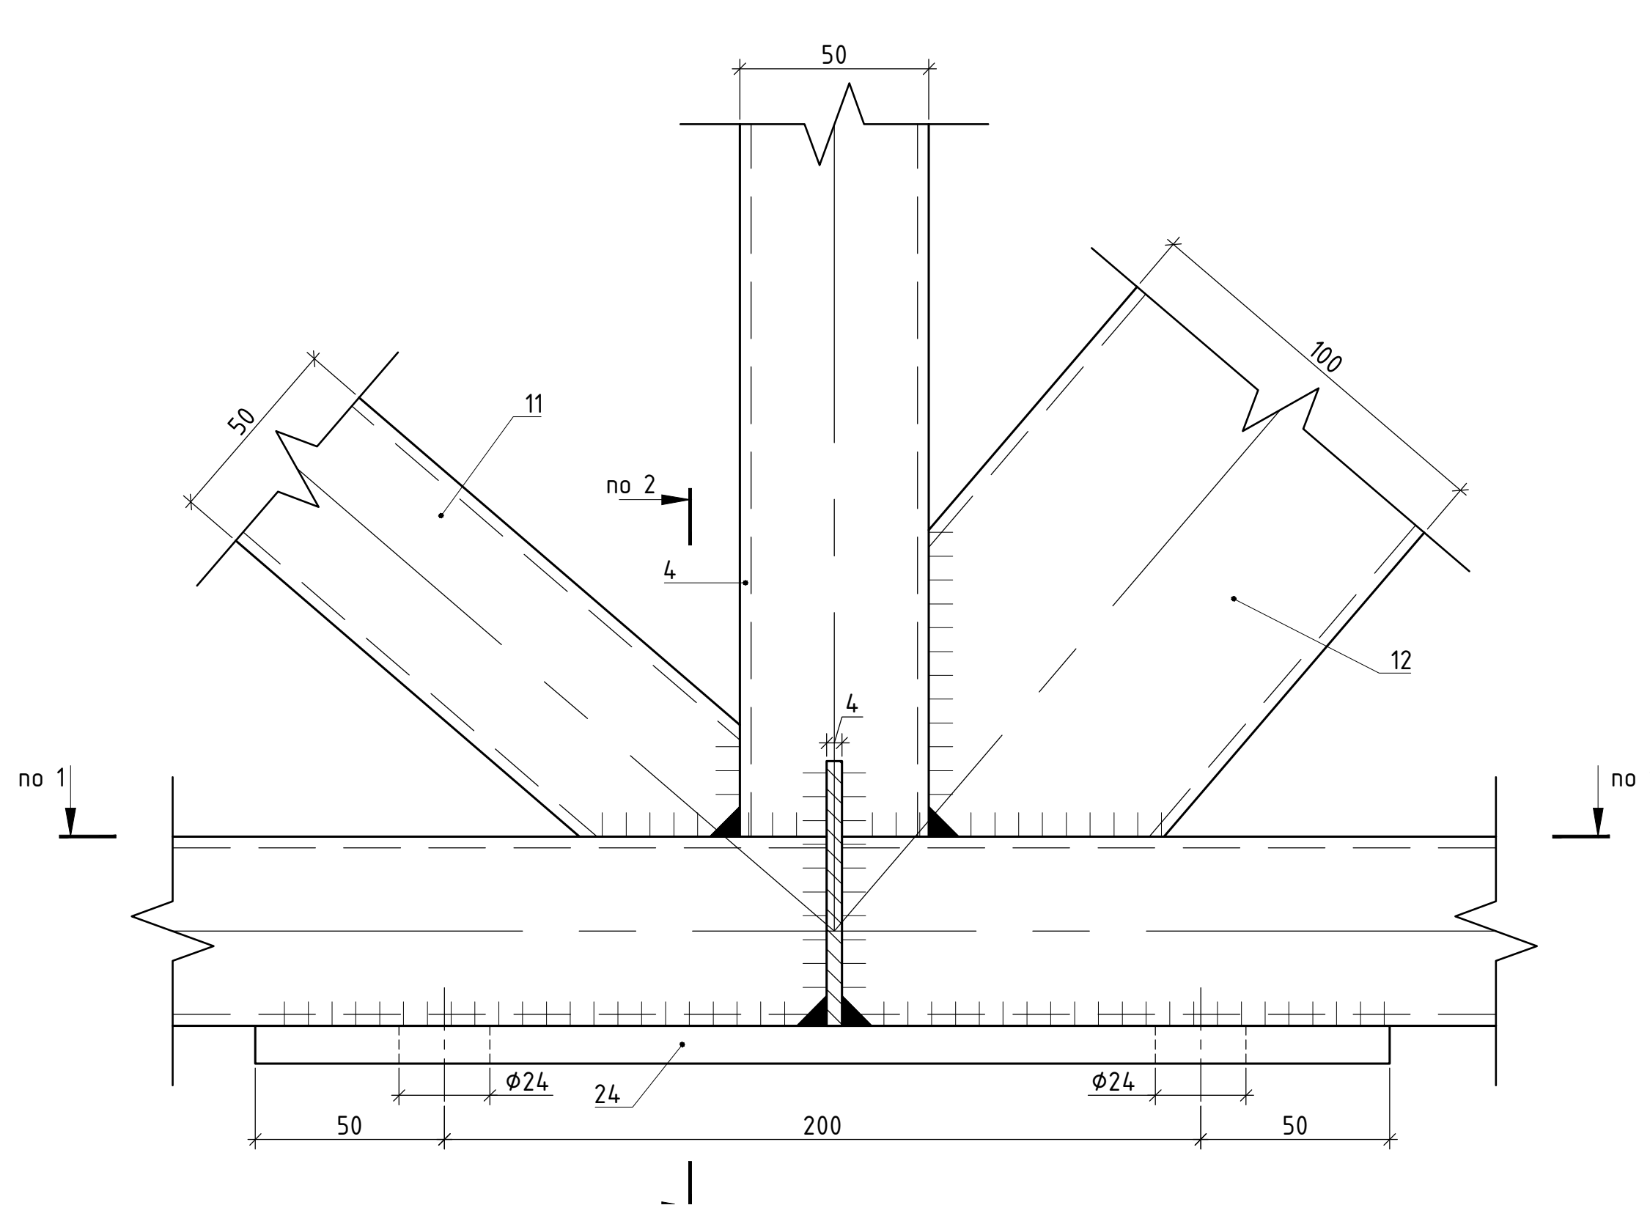

Отправная марка	Сборочная марка	Количество	Сечение	Длина, мм	Масса, кг		
					штуки	общая	марки
Ф1	1	1	Гн. ☐ 50x50x3	9500	4,31	40,945	218,7
	2	1	Гн. ☐ 50x50x3	9400	4,31	40,514	
	3	1	Гн. ☐ 50x50x3	814	4,31	3,508	
	4	1	Гн. ☐ 50x50x3	968	4,31	4,172	
	5	1	Гн. ☐ 50x50x3	1276	4,31	5,500	
	6	1	Гн. ☐ 50x50x3	1583	4,31	6,823	
	7	1	Гн. ☐ 50x50x3	1891	4,31	8,150	
	8	1	Гн. ☐ 50x50x3	2045	4,31	8,814	
	9	1	Гн. ☐ 50x50x3	2199	4,31	9,478	
	10	1	Гн. ☐ 50x50x3	566	4,31	2,439	
	11	1	Гн. ☐ 50x50x3	1211	4,31	5,219	
	12	1	Гн. ☐ 100x60x3	1538	7,07	10,874	
	13	1	Гн. ☐ 50x50x3	1538	4,31	6,629	
	14	1	Гн. ☐ 50x50x3	1783	4,31	7,685	
	15	1	Гн. ☐ 50x50x3	1783	4,31	7,685	
	16	1	Гн. ☐ 50x50x3	2045	4,31	8,814	
	17	1	Гн. ☐ 50x50x3	2045	4,31	8,814	
	18	1	Гн. ☐ 50x50x3	2318	4,31	9,991	
	19	1	Гн. ☐ 50x50x3	2458	4,31	10,594	
	20	1	Гн. ☐ 50x50x3	1078	4,31	4,646	
	21	1	Гн. ☐ 50x50x3	1030	4,31	4,439	
	22	1	Гн. ☐ 50x50x3	683	4,31	2,944	
	23	8	-4x60x60	-	0,113	0,001	
	24	4	-10x240x400	-	7,536	0,030	
	25	16	-4x70x100	-	0,22	0,004	
	26	2	-4xØ200	-	0,986	0,002	
	Масса сварных швов					2,2	

Согласовано

Взам. инв. №

Подп. и дата

Инв. № подл.

Изм.	Кол. уч	Лист	№ док.	Подп.	Дата
ГИП					
Разраб.		Андреев			
Н. контр.					

J01-24207-КМ

-

Стадия	Лист	Листов
Р	5	

Ферма Ф1