| Отправная марка | Сборочная марка | Количество | Сечение | Длина, мм | Масса, кг | | |
|---|---|---|---|---|---|---|---|
| | | | | | штуки | общая | марки |
| Пф1 | 1 | 1 | Гн. ◻ 50х50х3 | 5730 | 4,31 | 24,696 | 64,69 |
| | 2 | 1 | Гн. ◻ 50х50х3 | 3006 | 4,31 | 12,956 | |
| | 3 | 2 | Гн. ◻ 50х50х3 | 1395 | 4,31 | 12,025 | |
| | 4 | 2 | Гн. ◻ 50х50х3 | 1292 | 4,31 | 11,137 | |
| | 5 | 3 | Гн. ◻ 50х50х3 | 300 | 4,31 | 3,879 | |
| | 6 | 2 | -4х55х60 | - | 0,104 | 0,0002 | |
| | 7 | 2 | -4х50х90 | - | 0,353 | 0,0007 | |
| | Масса сварных швов | | | | | | 0,7 |

Ферма Пф1 (1:10)

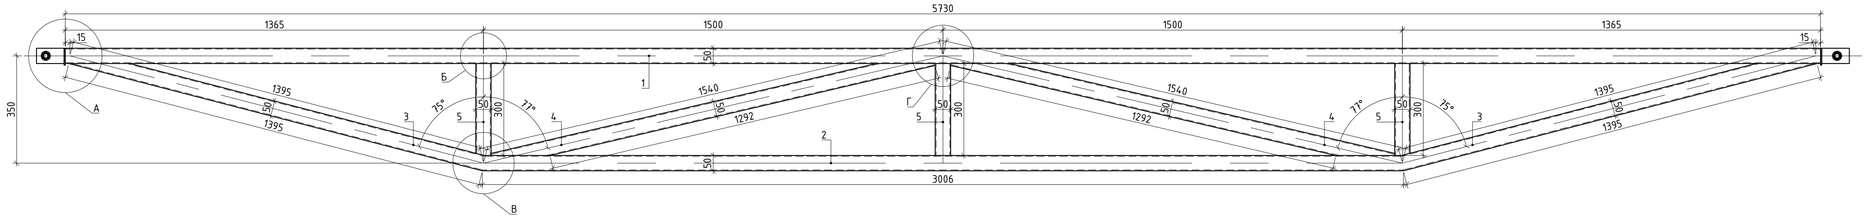


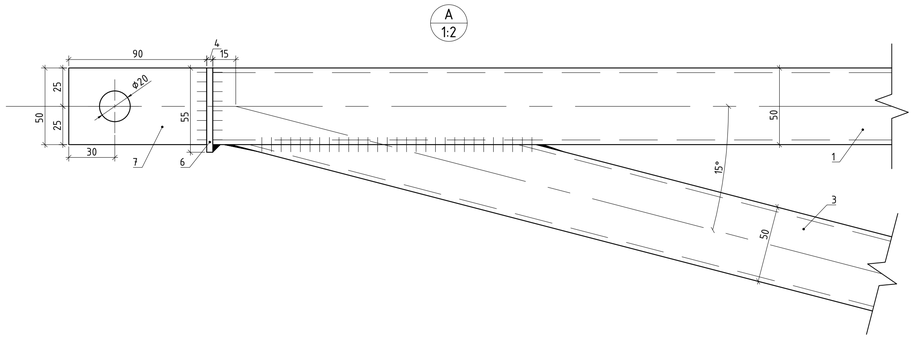


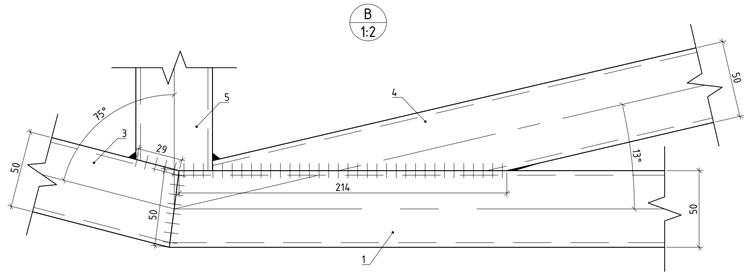


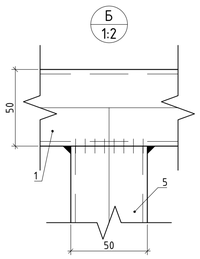


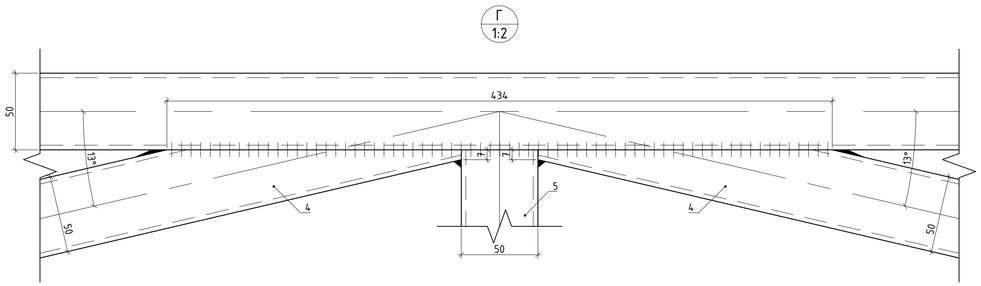


Согласовано

Взам. инв. №

Подп. и дата

Инв. № подл.

| | | | | | | | | | |
|---|---|---|---|---|---|---|---|---|---|
| | | | | | | | | JO1-24207-КМ | |
| Изм. | Кол. уч. | Лист | № док. | Подп. | Дата | | | | |
| ГИП | | | | | | | Стадия | Лист | Листов |
| Разраб. | | Андреев | | | | - | Р | 6 | |
| | | | | | | | | | |
| | | | | | | | | | |
| Н. контр. | | | | | | Ферма Пф1 | | | |