


Опалубочный план плиты на отм. 0,000 (+25,600) (1:50)

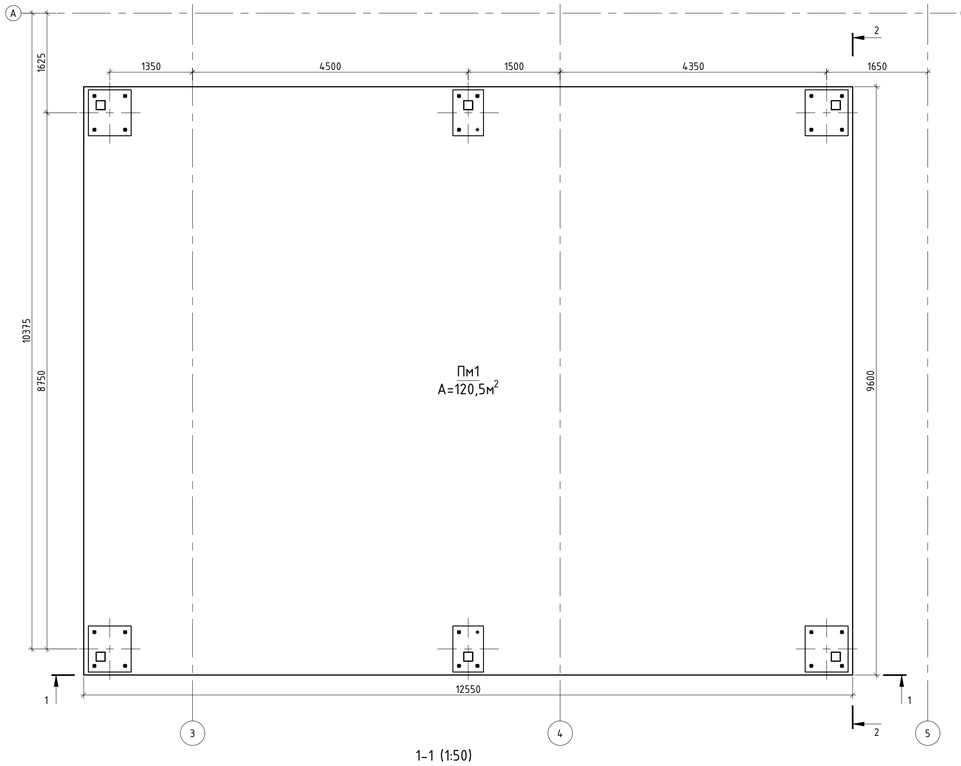


1-1 (1:50)

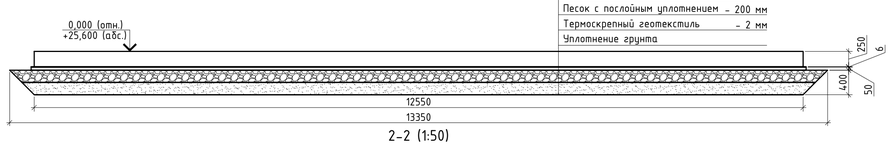

2-2 (1:50)

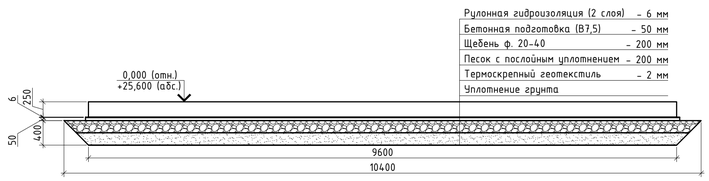

3-3 (1:5)

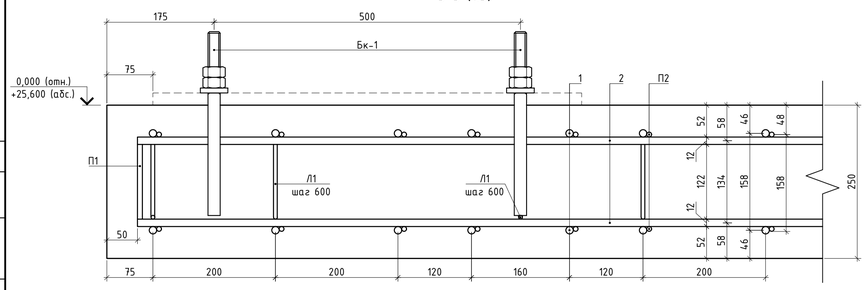

4-4 (1:5)


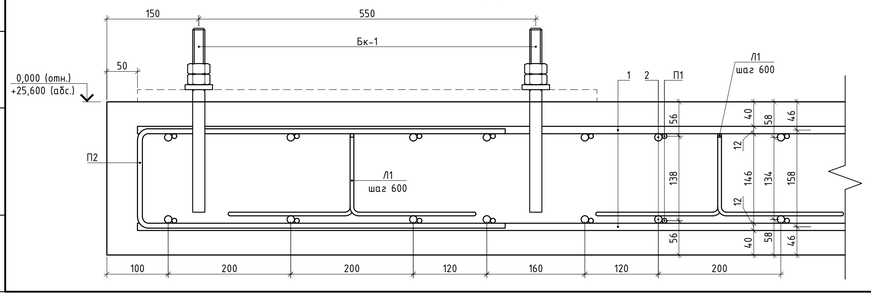


Схема верхнего и нижнего армирования плиты Пм1 (1:50)

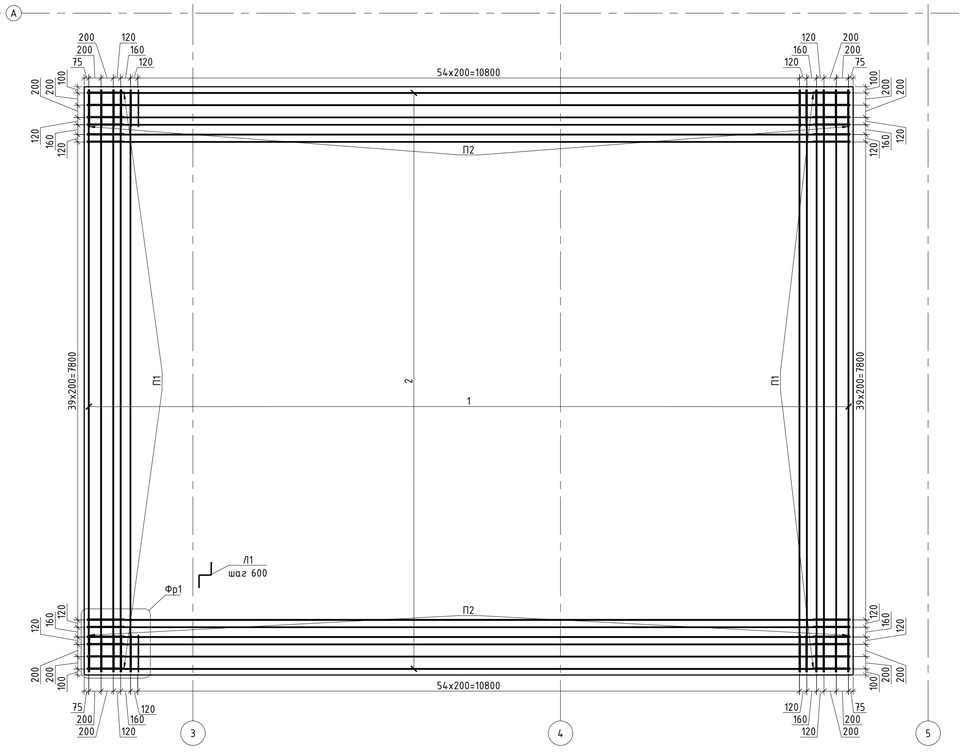

Спецификация материалов фундаментной плиты Пм1

Поз.	Обозначение	Наименование	Кол.	Масса ед. кг	Примечания
		Плиты монолитные			
Пм1	Данный лист	Пм1	1		
		Материалы			
	Плита Пм1	Бетон класса В25, F100, W6	30,13		$м^3$
		Рулонная гидроизоляция	122,75		$м^2$
	Бетонная подготовка	Бетон класса В7,5, F75, W4	6,14		$м^3$
		Щебень ф. 20-40	617,22		$м^3$
		Песок средней крупности	536,74		$м^3$
		Термоскрепный геотекстиль	120,50		$м^2$
Бк-1	Болтокомплект	Болтокомплект для фундамента стойки	4		шт

Спецификация материалов болтокомплекта БК-1

Поз.	Обозначение	Наименование	Кол.	Масса ед. кг	Примечания
		Болт 5М20х200, Вст3пс6 ГОСТ 24379.1-2012	4		шт
		Гайка М20	4		шт
		Контргайка М20	4		шт
		Шайба М20	4		шт

Спецификация элементов к монолитным конструкциям

Поз.	Обозначение		Кол.	Масса ед., кг	Примечание
		Пм1			
		Сборочные единицы и детали			
1	Данный лист	ø12 А500С ГОСТ Р 52544-2006 l=9500	130	8,44	1096,68
2	Данный лист	ø12 А500С ГОСТ Р 52544-2006 l=12450	100	11,06	1105,56
П1	Данный лист	ø8 А500С ГОСТ Р 52544-2006 l=2550	65	1,01	65,47
П2	Данный лист	ø8 А500С ГОСТ Р 52544-2006 l=750	50	0,30	14,81
Л1	Данный лист	ø6 А500С ГОСТ Р 52544-2006 l=750	238	0,17	39,63


Ведомость расхода стали на элемент

Марка элемента	Арматура класса (ГОСТ 52544-2006)				Общий расход кг
	Класс А240	Класс А500С		Итого класса А500С	
	ø6	ø8	ø12		
Фундаментная плита Пм1	40	80	2202	2283	2322

Ведомость деталей

Поз.	Эскиз
П1	l=1320 мм; R10; 600; 146; R18; 600
П2	l=1335 мм; R10; 600; 162; R18; 600
Л1	l=860 мм; 200; 128; 200; 200; 200

Фрагмент 1 (1:5)

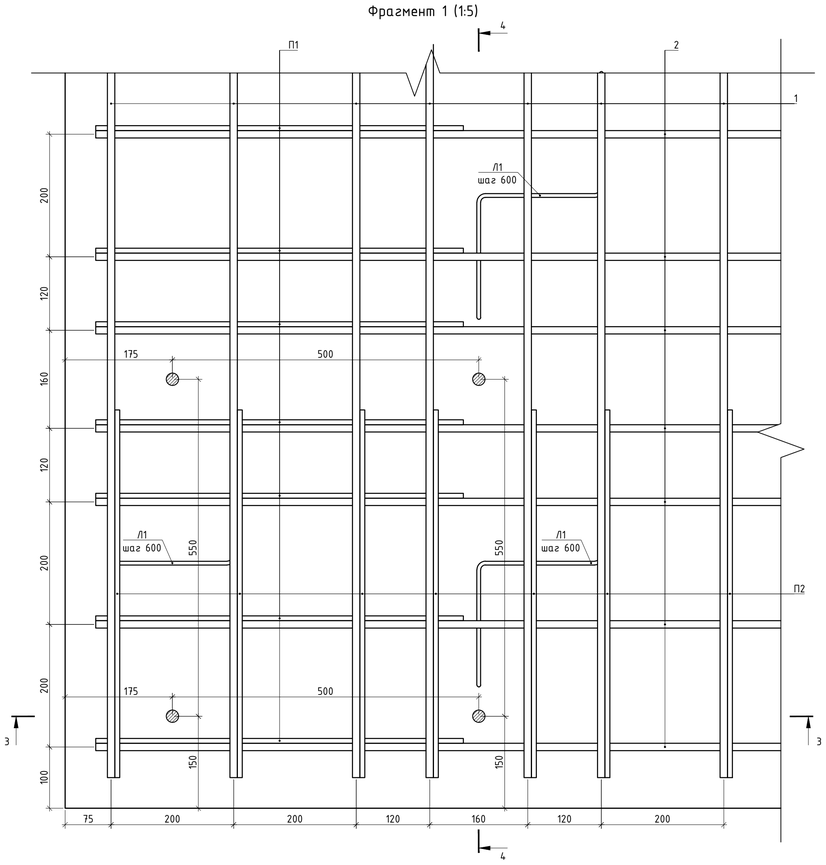

Изм.	Кол. уч.	Лист	№ док.	Подп.	Дата	J01-24207-КЖ			
ГИП						–	Стадия	Лист	Листов
Разраб.		Андреев					Р	2	
Н. контр.						Плита Пм1. Опалубочный план. Армирование. Спецификация материалов. Спецификация материалов болтокомплекта БК-1. Спецификация элементов к монолитным конструкциям. Ведомость расхода стали. Ведомость деталей			

Согласовано

Взам. инв. №

Подп. и дата

Инв. № подл.