Ведомость рабочих чертежей комплекта "КМ"

Лист	Наименование	Лист
1	Общие данные	
2	План расположения колонн на отм. -0,040. Ведомость элементов	
3	Схема расположения конструкций на отм. +2,500. Спецификация элементов металлопроката	
4	Разрезы 1-1, 2-2, 3-3, 4-4, 5-5, 6-6, 7-7	
5	Фрагмент А. Узлы 1-12. Ограждения Ог1, Ог2	
6	ЛВМ-1, ЛВМ-2, ЛВМ-3. Разрезы Л1-Л1, Л2-Л2, Л3-Л3, Л4-Л4, Л5-Л5. Узлы Л1, Л2, ..., Л10.	
	Спецификация элементов металлопроката	
7	Фрагмент Б. Разрезы 8-8,...,11-11. Узлы 13-22. Спецификация элементов металлопроката	
8	Узлы 23-30	
9	Фрагмент В. Разрезы 12-12, 13-13. Узлы 31-35. Спецификация элементов металлопроката	
10	Фрагмент Г. Разрезы 14-14, 15-15. Узлы 36, 37. Спецификация элементов металлопроката	
11	Фрагмент Д	

Общие указания

Основные исходные данные

1. Настоящая рабочая документация выполнена в соответсвии с договором и разработана на основании архитектурных и технологических заданий.
2. Проект соответствует действующим нормам, правилам, стандартам и обеспечивает безопасную эксплуатацию сооружений при соблюдении предусмотренных проектом мероприятий.
3. Ведомость основных комплектов рабочих чертежей см. основной кмоплект марки АР.
4. Металлоконструкции запроектированы в соответствии с требованиями СП 16.13330.2017 "Стальные конструкции", СП 20.13330.2016 "Нагрузки и воздействия".
5. Уровень ответственности сооружения - нормальный, в соответствии с ГОСТ Р 27751-2014 "Надежность строительных конструкций и оснований" класс сооружения КС-2. При расчете учтен коэффициент надежности по ответственности 1,0.

Указания по изготавлению и монтажу конструкций

6. Монтаж конструкций вести по проекту производства работ, разработанному с учетом конкретных возможностей монтажной организации и рекомендаций данного проекта.
7. Изготавление и монтаж конструкций вести согласно требованиям:
СП 70.13330.2012 "Несущие и ограждающий конструкции";
СП 49.13330.2010 "Безопасность труда в строительстве. Часть 1. Общие требования";
СНиП 12-04-2002 "Безопасность труда в строительстве. Часть 2";
ГОСТ 23118-2019 "Конструкции стальные строительные";
СП 53-101-98 "Изготавление и контроль качества стальных строительных конструкций".
8. Заводские соединения-сварные.
9. Монтажные соединения:
сварные;
на болтах нормальной точности.
10. Операционный контроль качества сварных швов производить по ГОСТ 23118-2019.
11. Разделку кромок и зазоры в сварных соединениях принимать по ГОСТ 8713-79, ГОСТ 5264-80, ГОСТ 14771-76.
12. Все принципиальные изменения в процессе разработки деталировочных чертежей КМД должны быть согласованы с ООО "Урбан".

Материал конструкций

13. Заводские сварные соединения выполнять полуавтоматической сваркой в среде углексилого газа (ГОСТ 8050-85) по ГОСТ 14771-76 сварочной проволокой СВ-08Г2С ф1.4-2.0 мм по ГОСТ 2246-76.
14. Монтажные сварные соединения выполнять ручной сваркой по ГОСТ 5264-80, ГОСТ 11534-75: электродами типа Э50А. Неоговоренны сварные швы принимать не менее указанных в табл. 38 СП 16.13330.2017.
16. Болты должны иметь клеймо и маркировку завода изготовителя. Применение автоматной стали для изготовления болтов, а также облегченных болтов не допускается.

Антикоррозионная защита и огнезащита

17. При выполнении антикоррозионной и огнезащиты стальных конструкци руководствоваться требованиями СП 28.13330.2017 "Защита строительных конструкций от коррозии", СП 2.13130.2020 "Системы противопожарной защиты. Обеспечение огнестойкости объектов защиты", ФЗ №123 "Технический регламент о требованиях пожарной безопасности".
18. Перед нанесением защитных покрытий поверхнось конструкций необходиом очистить до степени "2" в соответствии с требованиями ГОСТ 9.402-2004. Качество лакокрасочного покрытия должно соответствовать классу IV.
19. Степень огнестойкости здания - II. В соттветствии с таблицей №21 ФЗ №123 предел огнестойкости основных несущих элементов здания должен быть не менее:
- колонны, связи, распорки - R90;
- балки перекрытия - REI45;

20. Цвет наружного покровного слоя колонн, балок, связей, распорок, площадок, лестниц принимать RAL 7045 (серый).
21. Цвет наружного покровного слоя ограждений площадок и лестниц принимать RAL 1006 (ярко оранжевый).
22. Поставка стальных конструкций огрунтованными или окончательно окрашенными определяется заказчиком.
Грунт - 2 слоя грунта ГФ-021 (ГОСТ 25129-2020)
Краска - 2 слоя эмали ПФ-115 (ГОСТ 6465-2023)

Перечень ответственных строительных конструкций и работ

23. Обязательно составление актов освидетельствования всех скрытых работ:
- акт на монтаж всех металлических элементов, указанных в ведомости элементов;
- акт на предварительную подготовку повехностей, защищаемых от агрессивного воздействия среды;
- акт на установку стальных конструкций, скрывающихся в процессе производства последующих рабо;
- акт на опирание и анкеровку несущих металлических конструкций;
- акт на защиту строительных конструкций и закладных деталей от коррозии.

Согласовано


Взам. инв. №

Подп. и дата

Инв. № подл.

						КПТО/11/КР-4.КМ1	
Изм.	Кол. уч.	Лист	№ док.	Подп.	Дата		
ГИП						Комплекс по переработке рыбы	Стадия: Р; Лист: 1; Листов:
Разраб.		Андреев					
Н. контр.						Общие данные	


План расположения колонн на отм. -0,040 (М1:100)

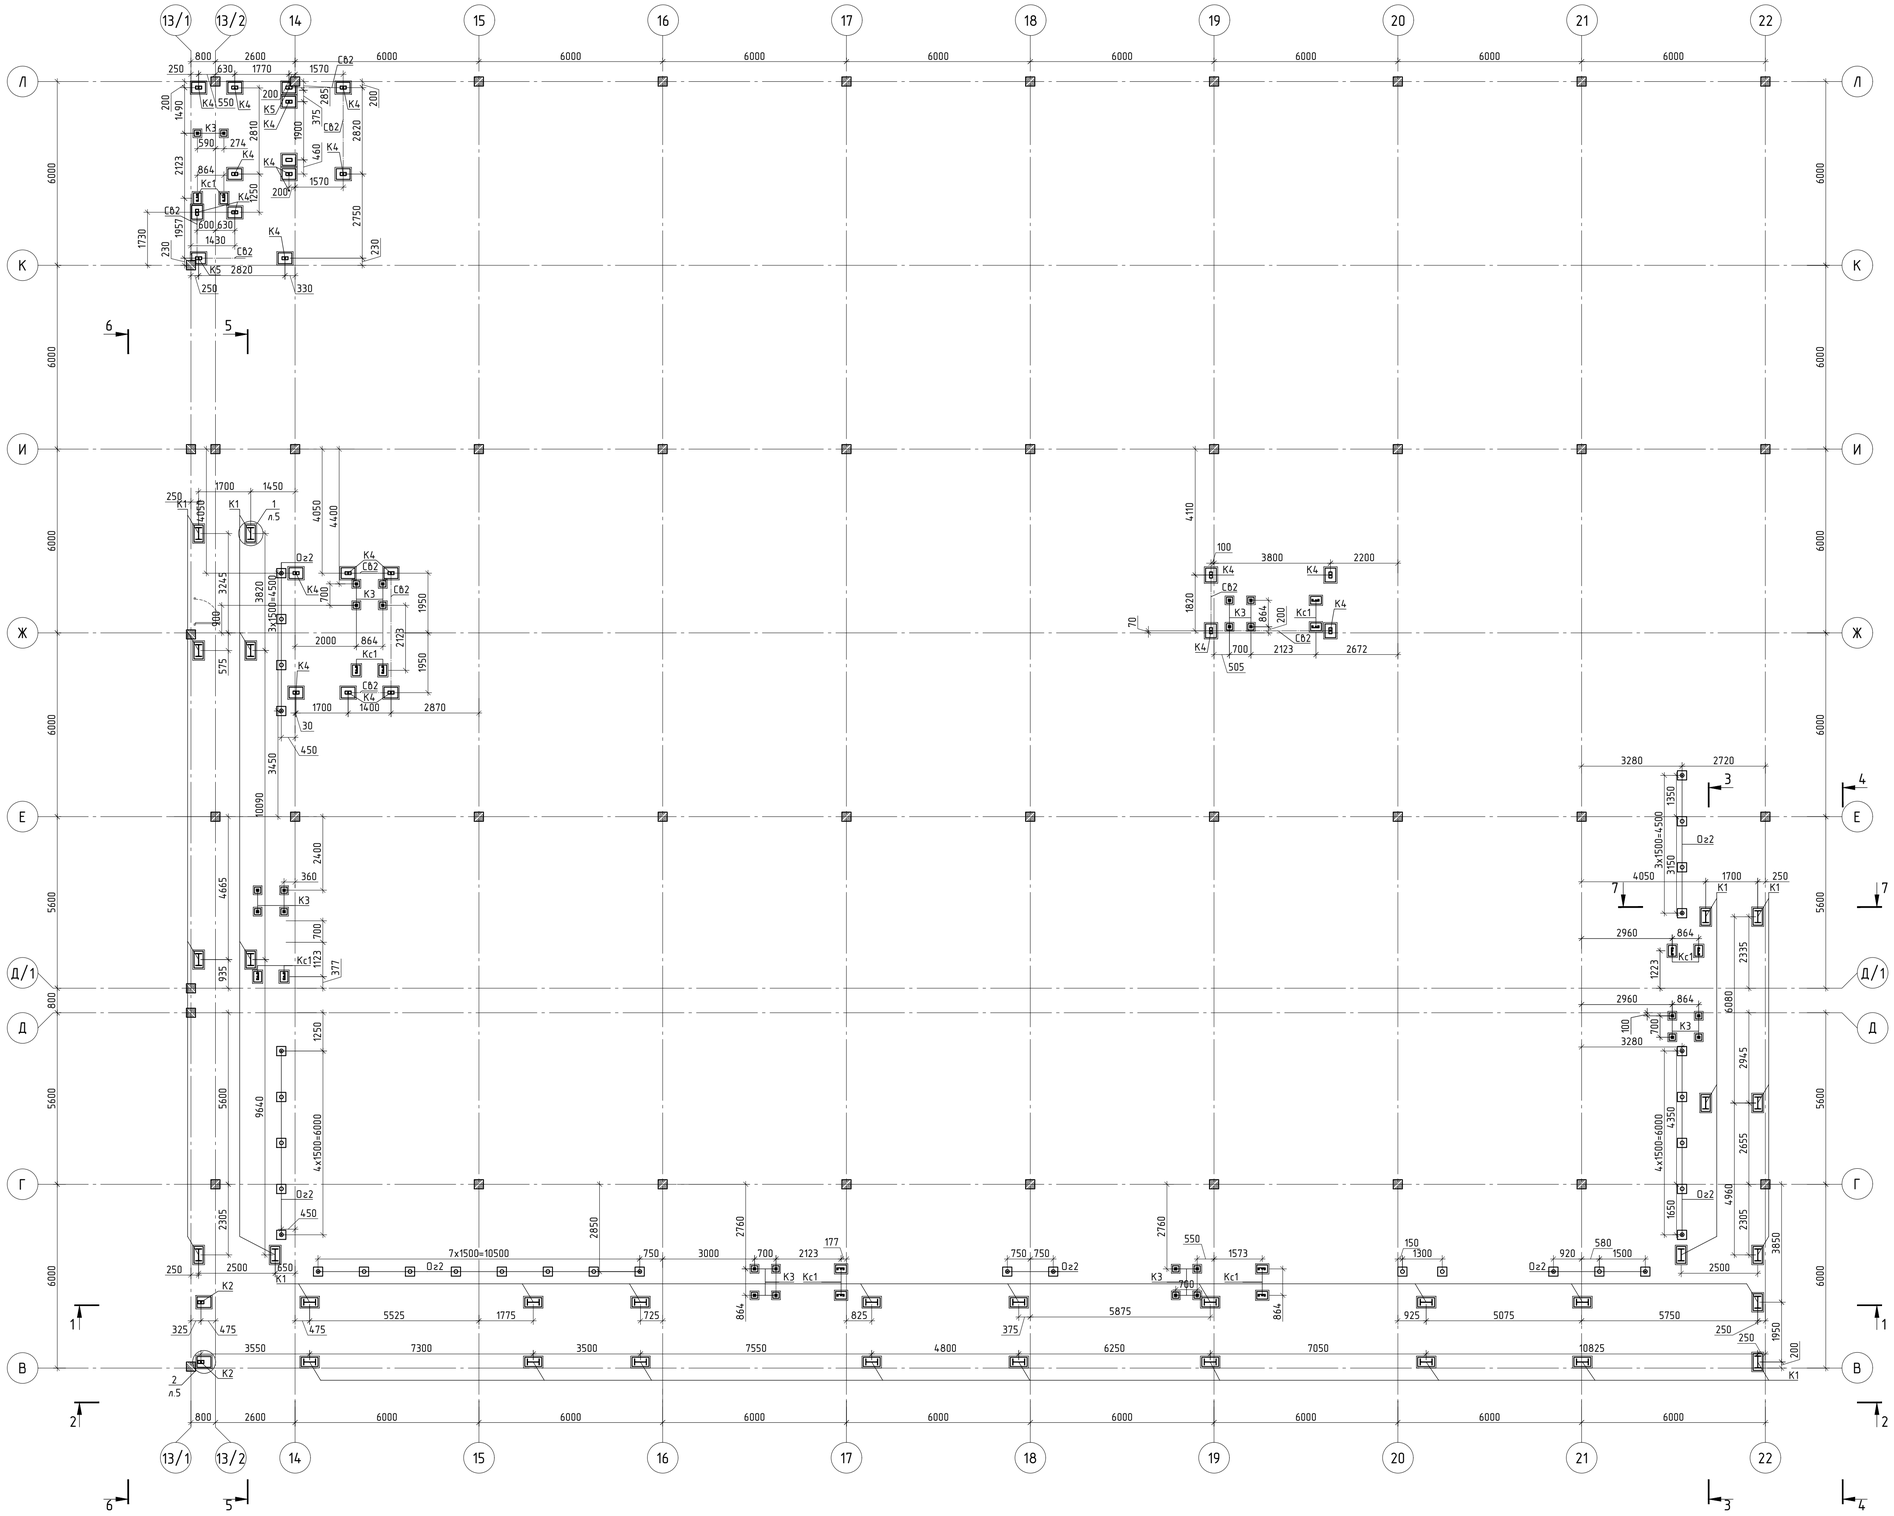
13/1
13/2
14
15
16
17
18
19
20
21
22
Л
К
И
Ж
Е
Д/1
Д
Г
В
6000
5600
800
2600
1770
1570
Сб2
630
550
K4
K5
K3
Кс1
590
274
2810
1900
375
285
460
2820
2123
1250
1570
1430
600
1730
1957
230
2750
330
250
2820
1700
1450
4050
4400
K1
1 л.5
Оц2
3745
3820
3150+4500
700
1950
900
575
2000
864
2123
1400
2870
30
450
3450
10090
2400
360
4665
935
1123
377
5600
9640
4х1500=6000
2305
2850
7х1500=10500
750
3000
2760
700
177
2500
550
K2
325
475
5525
1775
725
864
825
7300
3500
7550
4800
6250
7050
10825
2 л.5
4110
100
3800
2200
1820
505
2672
3280
2720
1350
3150
4050
2960
1223
2335
6080
2945
4350
2655
4960
1650
2305
3850
920
580
1500
5875
760
150
1300
925
5075
5750
250
1950
200
Кс1
Оц2
K1
K2
K3
K4
K5
Сб2
Сб1
1
2
3
4
5
6
7
Ведомость элементов
Марка
Сечение
Эскиз
Поз.
Состав
Усилие для прикрепления
M, кНм
N, кН
Q,кН
Группа констр.
Марка стали
Примечания
Б1
1
20Б1
С245
Б2
1
20Б1
С245
Сц1
1
80х80х3
С245
2
-4х100х100
С245
Р1
1
80х80х3
С245
2
-4х100х100
С245
Р2
1
80х80х3
С245
2
-4х100х100
С245
Р3
1
80х80х3
С245
Сб1
1
80х80х3
С245
2
80х80х3
С245
3
80х80х3
С245
4
80х80х3
С245
5
-4х100х100
С245
Сб2
1
80х80х3
С245
2
-4х100х100
С245
К1
1
20К1
С245
2
-20х300х550
С245
3
-20х300х550
С245
К2
1
200х100х5
С245
2
-20х300х300
С245
3
-20х300х550
С245
К3
1
80х80х3
С245
2
-20х300х300
С245
3
-20х140х140
С245
К4
1
200х100х5
С245
2
-20х200х300
С245
3
-20х200х300
С245
К5
1
200х100х5
С245
2
-20х300х300
С245
3
-20
С245
Кс1
1
16П
С245
Уг1
1
40х40х4
С245
Нс1
1
НП60-845-0,8
Ст3пс
Нс2
1
SP 34х50/30х3, S4
Ст3пс
Оц1
1
Ф48х3.5
С245
2
Ф48х3.5
С245
3
-8х140
С245
Оц2
1
Ф127х3
С245
2
-20х300х300
С245
3
-4хФ150
С245
Оц3
1
Ф48х3.5
С245
2
Ф48х3.5
С245
3
-8х140
С245
2
*Примечание: ведомость элементов составлена на листы 2-11 комплекта КПТО/11/КР-4 КМ1


Согласовано
Взам. инв. №
Подп. и дата
Инв. № подл.

Изм.	Кол. уч.	Лист	№ док.	Подп.	Дата	КПТО/11/КР-4.КМ1			
ГИП						Комплекс по переработке рыбы	Стадия	Лист	Листов
Разраб.		Андреев					Р	2	
Н. контр.									

Схема расположения конструкций на отм. +2,500 (М1:100)

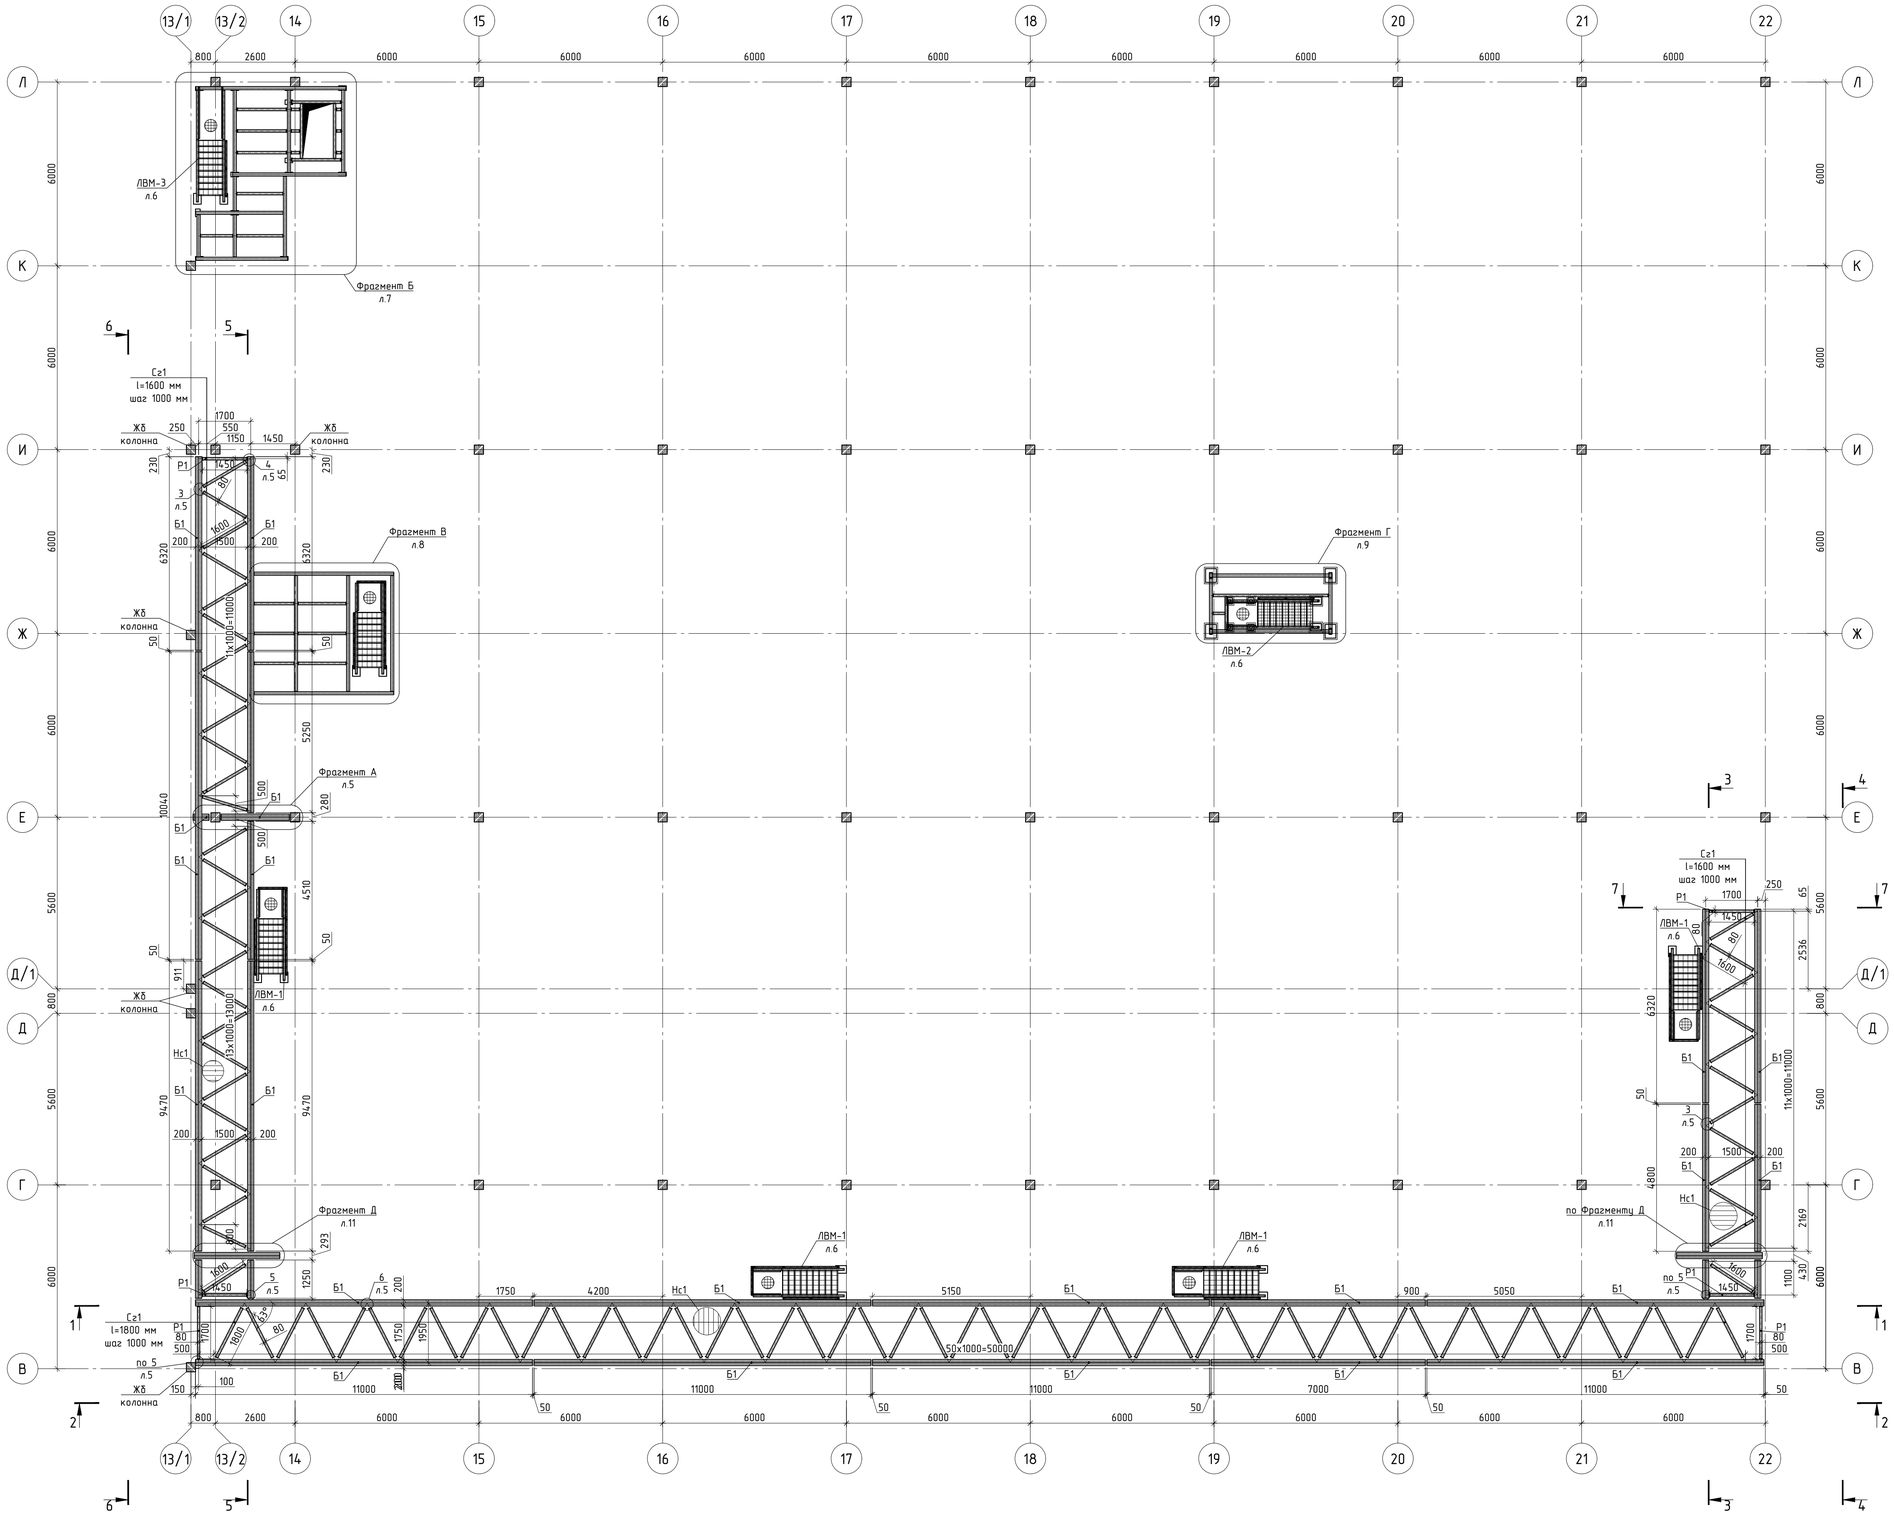

Принципиальная схема анкеровки профнастила к полке бакли(1:10)

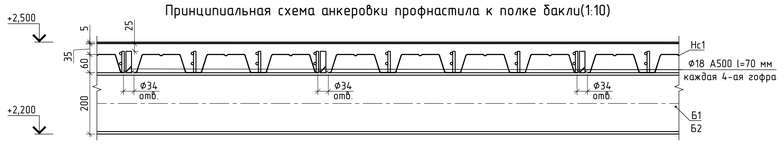

Спецификация элементов металлопроката

Наименование профиля ГОСТ, ТУ	Наименование или марка металла ГОСТ, ТУ	Номер или размер профиля, мм	Поз.	Марка металла по элементам конструкций, т				Общая масса, т
				Колонны	Балки	Распорки, стойки, связи	Ограждение	
Двутавры стальные горячекатанные по ГОСТ Р 57837О-2017	С245	20Б1	1		8,06			8,06
	ГОСТ	20К1	2	2,99				2,99
	Итого:		3	2,99	8,06			11,06
Профили стальные гнутые замкнутые сварные квадратные и	С245	200х100х5	4	0,10				0,10
	ГОСТ		5					
	Итого:		6	0,10				0,10
Трубы стальные квадратные по ГОСТ 8639-82	С245	80х80х3	7			1,18		1,18
	ГОСТ		8					
	Итого:		9			1,18		1,18
Сталь листовая горячекатаная, по ГОСТ 19903-74	С245 ГОСТ 27772-15	t=2	10				2,24	2,24
		t=4	11			0,06	0,02	0,08
		t=8	12		0,02	1,10	0,30	1,43
		t=10	13	0,08	0,18			0,27
		t=12	14		0,002			0,00
		t=20	15	1,74			0,47	2,20
	Итого:		16	1,82	0,21	1,16	3,03	6,21
Трубы стальные электросварные прямошовные	В-Ст3сп	48х3,5	17				2,64	2,64
	ГОСТ	127х3	18				0,18	0,18
	Итого:		19				2,82	2,82
Всего масса металла			20	4,91	8,27	2,33	5,85	21,37
В том числе по маркам или								
С245			21	4,91	8,27	2,33	3,03	18,55
В-Ст3сп			22				2,82	2,82

*Примечание: спецификация элементов металлопроката составлена на листы 2-5, 11 комплекта КПТО/11/КР-4 КМ1, без учета металлопроката на элементы конструкций лестниц и площадок, вынесенных на фрагментах Б, В, Г

							КПТО/11/КР-4.КМ1		
Изм.	Кол. уч.	Лист	№ док.	Подп.	Дата				
ГИП						Комплекс по переработке рыбы	Стадия	Лист	Листов
Разраб.		Андреев					Р	3	
						Схема расположения конструкций на отм. +2,500. Спецификация элементов металлопроката			
Н. контр.									

Согласовано


Взам. инв. №

Подп. и дата


Инв. № подл.

Полимерное покрытие
для пищевых производств – 5 мм
Ж/б плита – 30 95 мм
Настил профилированный
НП60-845-0,8 – 60 мм

1-1 (М1:50)

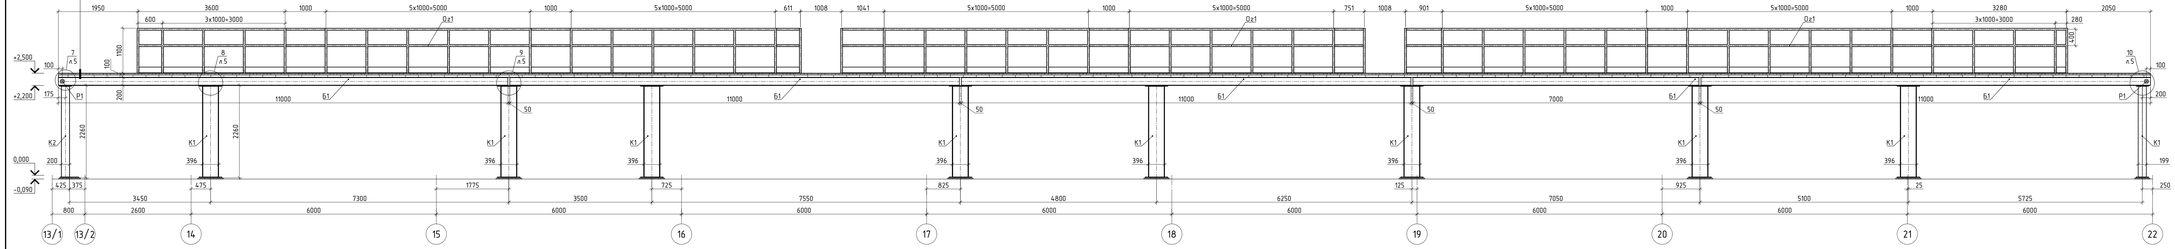


2-2 (М1:50)

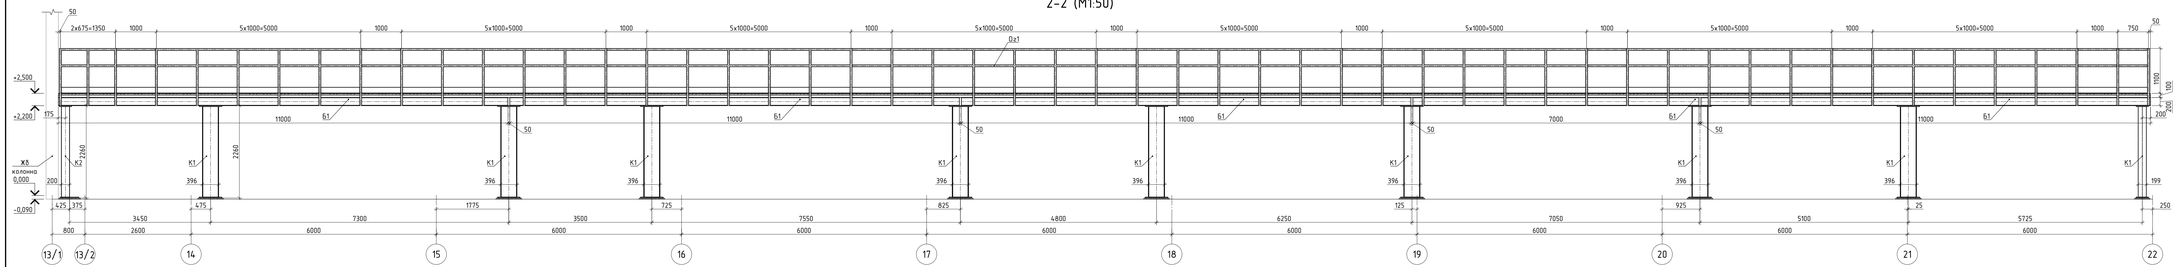


Полимерное покрытие
для пищевых производств – 5 мм
Ж/б плита – 30 95 мм
Настил профилированный
НП60-845-0,8 – 60 мм


5-5 (М1:50)

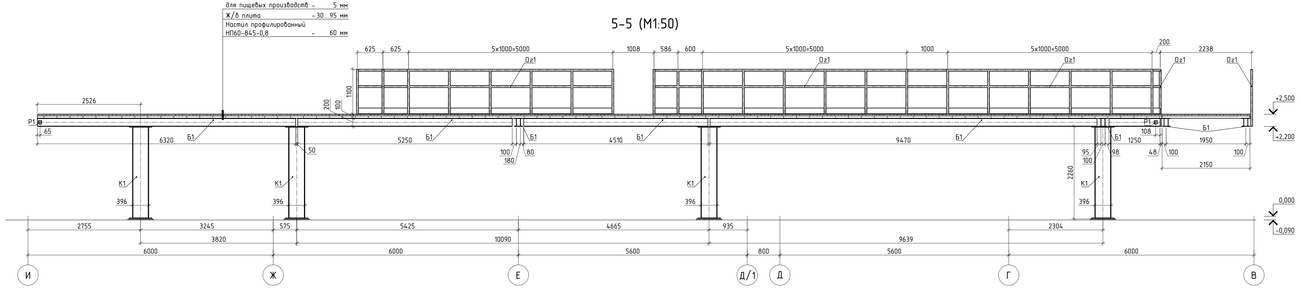


3-3 (М1:50)

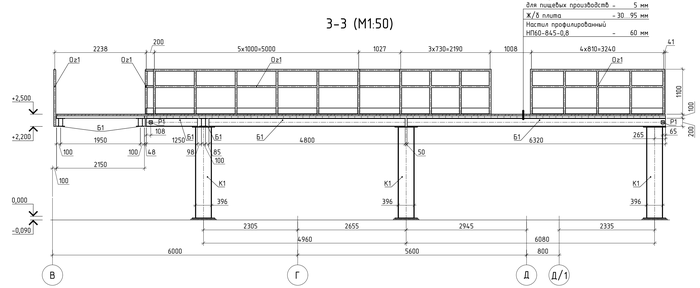


7-7 (М1:50)

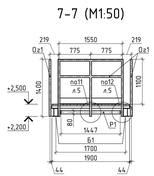

6-6 (М1:50)

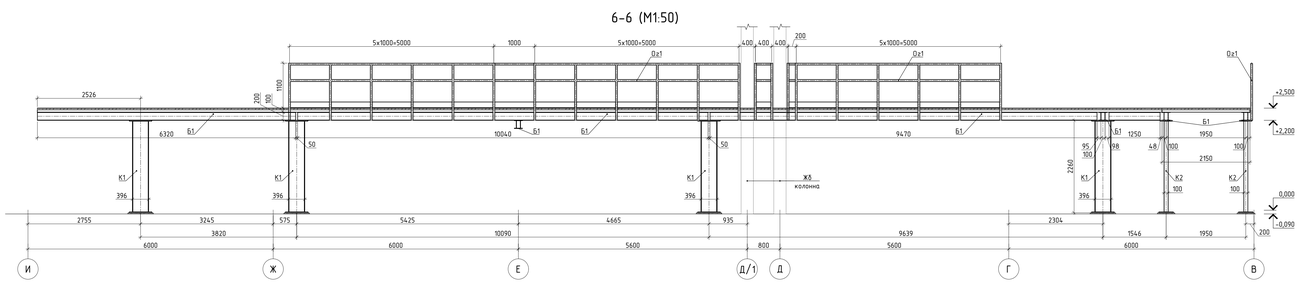

4-4 (М1:50)

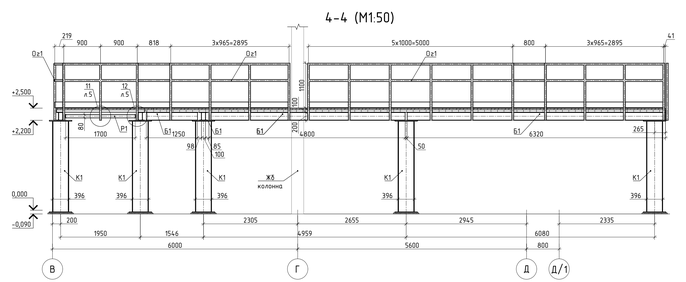


						КПТО/11/КР-4.КМ1	
Изм.	Кол. уч.	Лист	№ док.	Подп.	Дата		
ГИП						Комплекс по переработке рыбы	Стадия: Р; Лист: 4; Листов:
Разраб.		Андреев					
Н. контр.						Разрезы 1-1, 2-2, 3-3, 4-4, 5-5, 6-6, 7-7	


Согласовано

Инв. № подл. | Подп. и дата | Взам. инв. №


Фрагмент А (1:10)

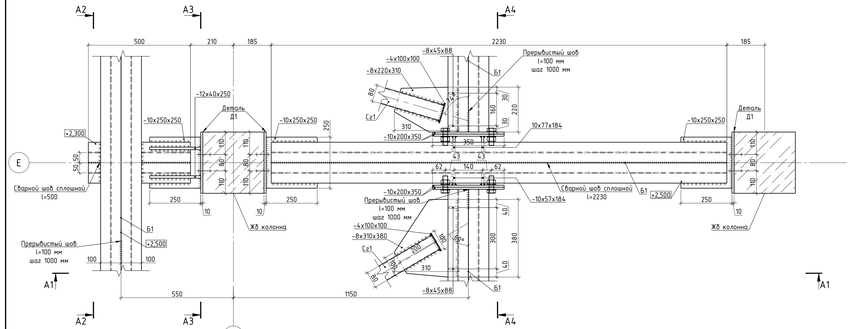


А1-А1 (1:10)

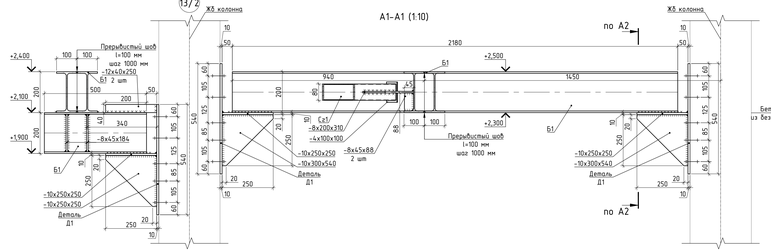


Деталь Д1 (1:10)

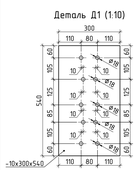


А3-А3 (1:10)

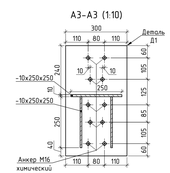


А2-А2 (1:10)

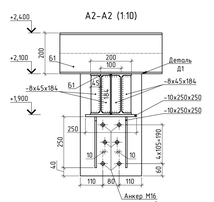


А4-А4 (1:5)

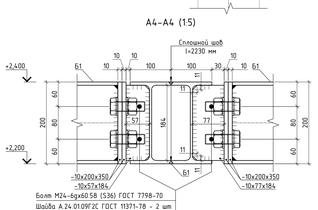


Ограждение Ог1 (1:10)

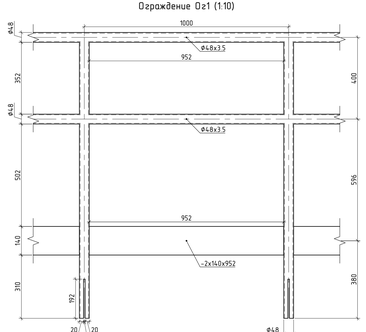


Ограждение Ог2 (1:10)

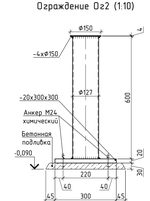


Ограждение Ог2 (1:10)

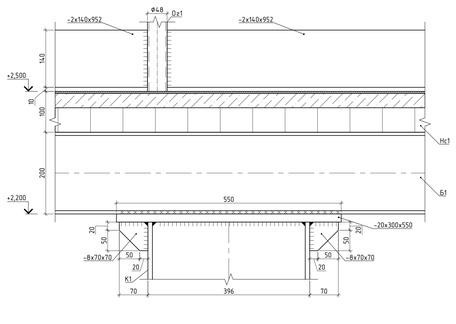


Ограждение Ог2 (1:10)

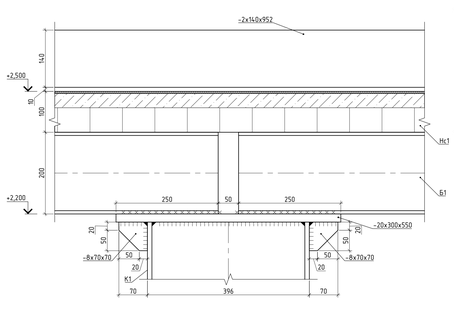


Ограждение Ог2 (1:10)

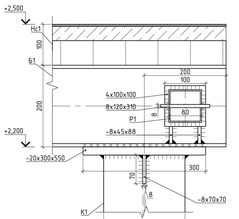


Ограждение Ог2 (1:10)

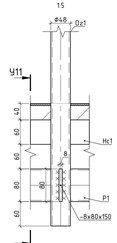

Ограждение Ог2 (1:10)

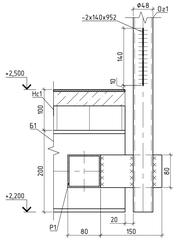


Ограждение Ог2 (1:10)

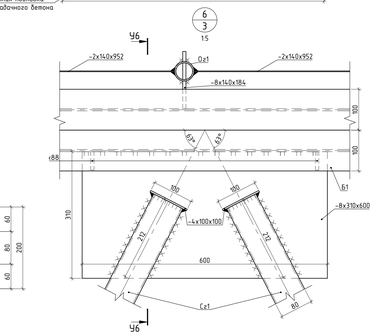


Ограждение Ог2 (1:10)


Ограждение Ог2 (1:10)

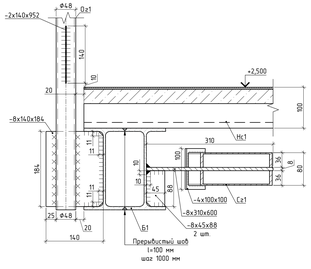


Ограждение Ог2 (1:10)

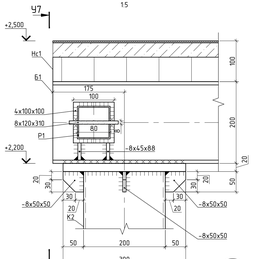


Ограждение Ог2 (1:10)

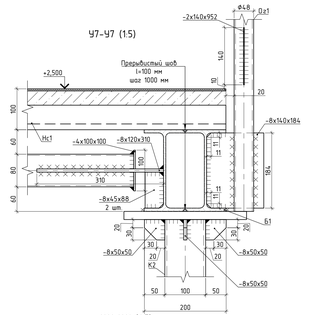


Ограждение Ог2 (1:10)

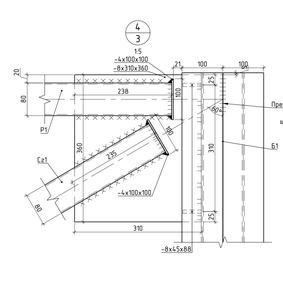


Ограждение Ог2 (1:10)

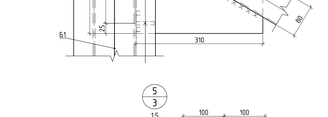

Ограждение Ог2 (1:10)

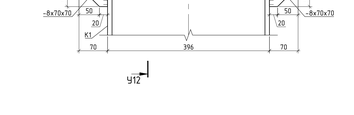


Ограждение Ог2 (1:10)

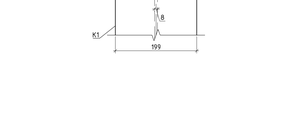


Ограждение Ог2 (1:10)



Ограждение Ог2 (1:10)

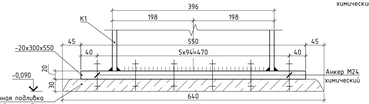

Ограждение Ог2 (1:10)

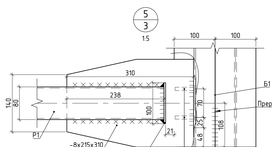

Ограждение Ог2 (1:10)



Ограждение Ог2 (1:10)

Ограждение Ог2 (1:10)

Ограждение Ог2 (1:10)

Ограждение Ог2 (1:10)

Ограждение Ог2 (1:10)

Ограждение Ог2 (1:10)

Ограждение Ог2 (1:10)

-20х300х550
Анкер М24
химический
Бетонная
подливка

ЛВМ-1 (1:25)



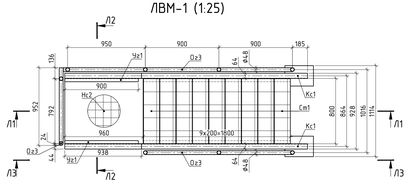



Схема баз колонн ЛВМ-1, ЛВМ-2 на отм. 0,000 (1:25)

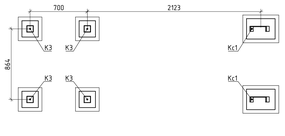


ЛВМ-2 (1:25)

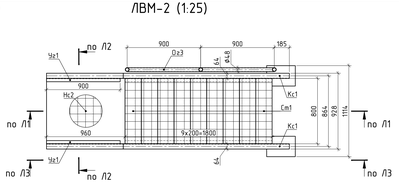


Л2–Л2 (1:25)

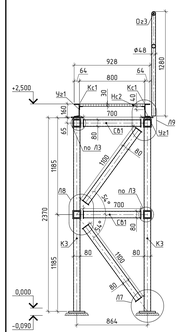


Л1–Л1 (1:25)

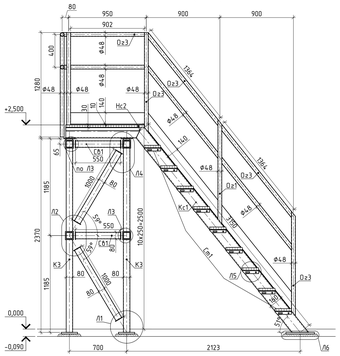


Л3–Л3 (1:25)

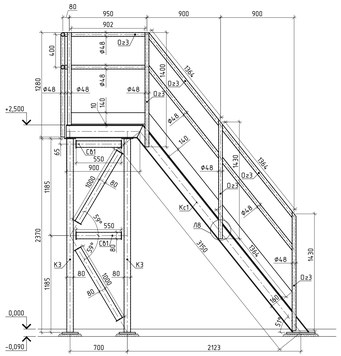


Л1 (6) 1:5

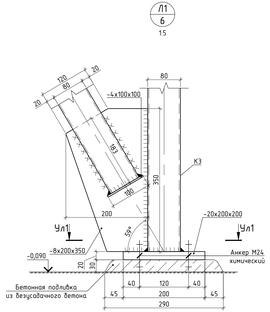


Ул1–Ул1 (1:5)

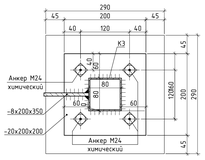


Л2 (6) 1:5

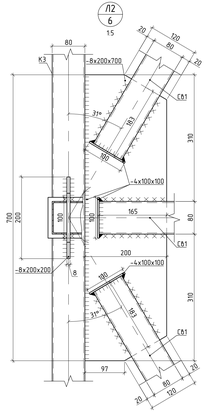


Л4 (6) 1:5

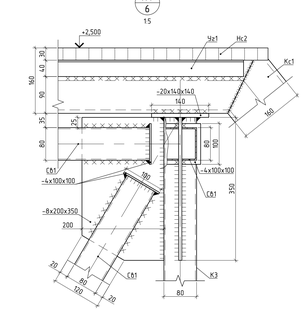


Л5 (6) 1:5

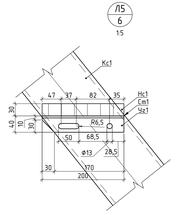


Л6 (6) 1:5

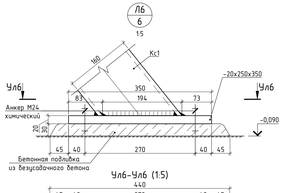


Ул6–Ул6 (1:5)

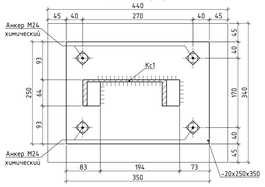


Л7 (6) 1:5

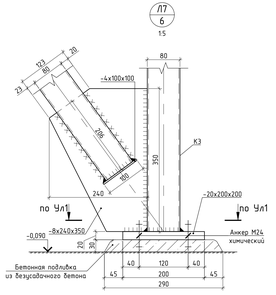


Л8 (6) 1:5

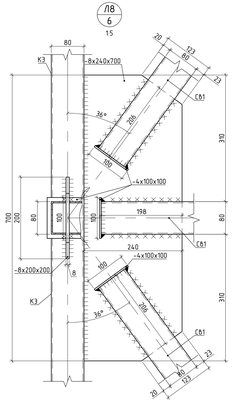

Л9 (6) 1:5

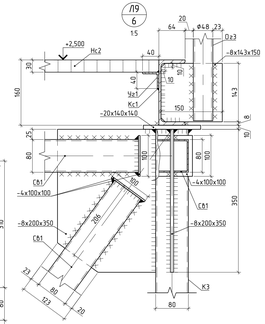

Л10 (6) 1:5

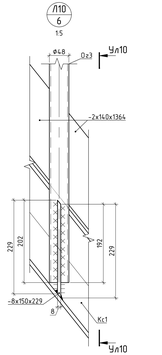

Ул10–Ул10 (1:5)


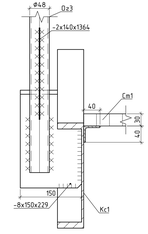



Схема баз колонн ЛВМ-3 на отм. 0,000 (1:25)




ЛВМ-3 (1:25)

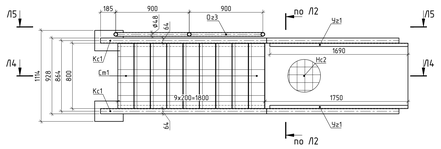

Л4–Л4 (1:25)

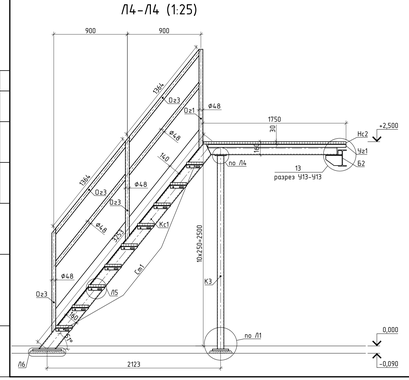

Л5–Л5 (1:25)

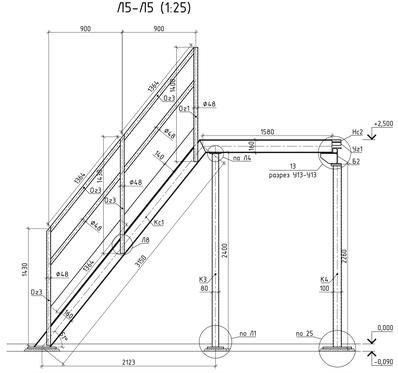

Спецификация элементов металлопроката

Наименование профиля ГОСТ, ТУ	Наименование или марка металла ГОСТ, ТУ	Номер или размер профиля, мм	Поз.	Марка металла по элементам конструкций, т				Общая масса, т
				Колонны	Косцуры	Распорки, связи, связи	Ограждения	
Швеллеры стальные горячекатаные с параллельными	С245 ГОСТ	16П	1		0,115			0,115
			2					
	Итого.		3		0,115			0,115
Трубы стальные квадратные по ГОСТ 8639-82	С245 ГОСТ	Гн.80х80х5	4	0,108		0,153		0,262
			5					
	Итого.		6	0,108		0,153		0,262
Сталь листовая горячекатаная, по ГОСТ 19903-74	С245 ГОСТ 27772-15	t=2	7				0,112	0,112
		t=4	8			0,010		0,010
		t=8	9	0,096	0,019			0,114
		t=20	10	0,037	0,011			0,048
	Итого.		11	0,133	0,030	0,010	0,112	0,284
Трубы стальные электросварные прямошовные	В-Сп3сп ГОСТ	48х3,5	12				0,053	0,053
	Итого.		13				0,053	0,053
Уголки стальные горячекатаные равнополочные	С245 ГОСТ	40х40х5	15		0,016			0,016
			16					
	Итого.		17		0,016			0,016
Всего масса металла			18	0,242	0,161	0,163	0,164	0,730
В том числе по маркам или								
С245			19	0,242	0,161	0,163		0,677
В-Сп3сп			20				0,053	0,053

*Примечание: спецификация элементов металлопроката составлена на ЛВМ-1(2)

Спецификация элементов металлопроката


Наименование профиля ГОСТ, ТУ	Наименование или марка металла ГОСТ, ТУ	Номер или размер профиля, мм	Поз.	Марка металла по элементам конструкций, т				Общая масса, т
				Колонны	Косцуры	Распорки, связи, связи	Ограждения	
Швеллеры стальные горячекатаные с параллельными	С245 ГОСТ	16П	1		0,115			0,115
			2					
	Итого.		3		0,115			0,115
Трубы стальные квадратные по ГОСТ 8639-82	С245 ГОСТ	Гн.80х80х5	4	0,108		0,153		0,262
			5					
	Итого.		6	0,108		0,153		0,262
Сталь листовая горячекатаная, по ГОСТ 19903-74	С245 ГОСТ 27772-15	t=2	7				0,086	0,086
		t=4	8			0,003		0,003
		t=8	9	0,025	0,013			0,038
		t=20	10	0,019	0,011			0,030
	Итого.		11	0,044	0,024	0,003	0,086	0,156
Трубы стальные электросварные прямошовные	В-Сп3сп ГОСТ	48х3,5	12				0,033	0,033
			13					
	Итого.		14				0,033	0,033
Уголки стальные горячекатаные равнополочные	С245 ГОСТ	40х40х5	15		0,021			0,021
			16					
	Итого.		17		0,021			0,021
Всего масса металла			18	0,152	0,160	0,156	0,119	0,587
В том числе по маркам или								
С245			19	0,152	0,160	0,156		0,554
В-Сп3сп			20				0,033	0,033

*Примечание: спецификация элементов металлопроката составлена на ЛВМ-3


Изм.	Кол. уч.	Лист	№ док.	Подп.	Дата	КПТО/11/КР-4.КМ1		
ГИП								
Разраб.	Андреев					Комплекс по переработке рыбы	Стадия	Лист	Листов
							Р	6	
Н. контр.						ЛВМ-1, ЛВМ-2, ЛВМ-3 Разрезы Л1–Л1, Л2–Л2, Л3–Л3, Л4–Л4, Л5–Л5 Узлы Л1, Л2, …, Л10. Спецификация элементов металлопроката.		

Инв. № подл. | Подп. и дата | Взам. инв. № | Согласовано


Фрагмент Б (1:25)

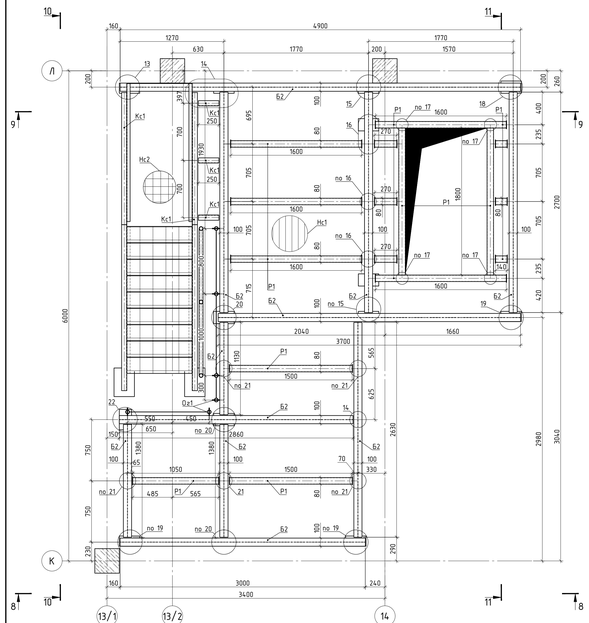


8-8 (М1:50)

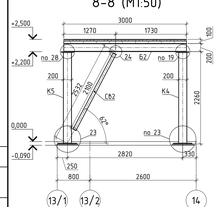


10-10 (М1:50)

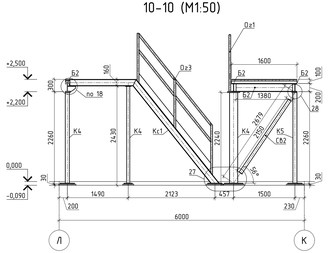


9-9 (М1:50)

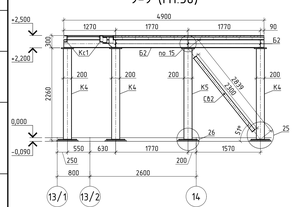


11-11 (М1:50)

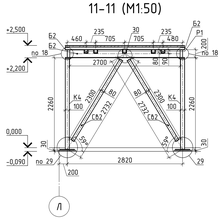


У13-У13 (1:5)

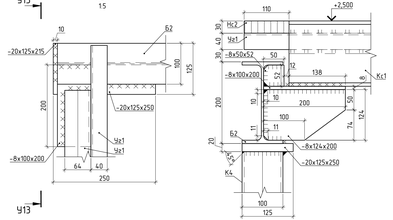


У14.2-У14.1 (1:5)

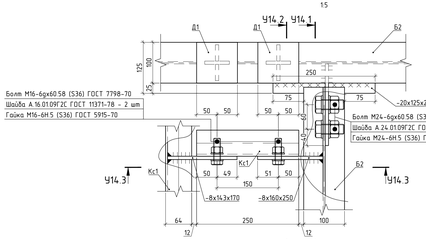


У14.1-У14.1 (1:5)

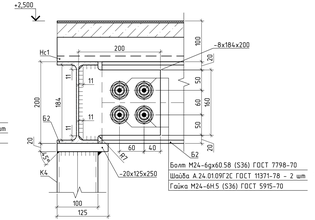


У14.2-У14.2 (1:5)

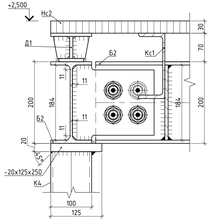


У14.3-У14.3 (1:5)

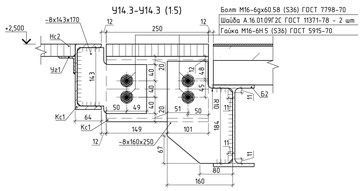


Деталь Д1 (1:5)

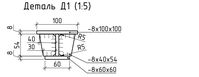


У15-У15 (1:5)

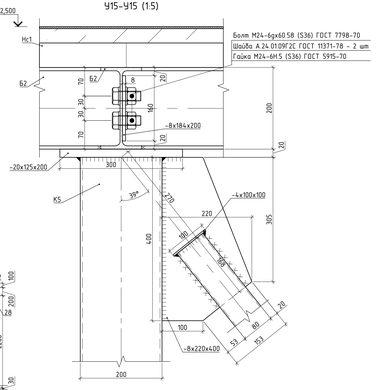


У16-У16 (1:5)

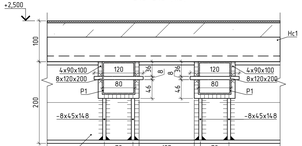

-8х143х170 (1:5)

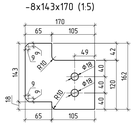

-8х160х250 (1:5)

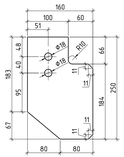

Спецификация элементов металлопроката

Наименование профиля ГОСТ, ТУ	Наименование или марка металла ГОСТ, ТУ	Номер или размер профиля, мм	Поз.	Марка металла по элементам конструкций, т				Общая масса, т
				Колонны	Балки	Распорки, стойки, связи	Ограждения	
Двутавры стальные горячекатанные по ГОСТ	С245 ГОСТ	20Б1	1		0,62			0,62
	Итого:		2					
Р 57837-2017	Итого:		3		0,62			0,62
Профили стальные гнутые замкнутые сварные квадратные и	С245 ГОСТ	200х100х5	4	0,65				0,65
	Итого:		5					
			6	0,65				0,65
Трубы стальные квадратные по ГОСТ 8639-82	С245 ГОСТ	80х80х3	7			0,20		0,20
	Итого:		8					
			9			0,20		0,20
Швеллеры стальные горячекатанные с параллельными	С245 ГОСТ	16П	10		0,01			0,01
	Итого:		11					
			12		0,01			0,01
Сталь листовая горячекатаная, по ГОСТ 19903-74	С245 ГОСТ 27772-15	т=2	13				0,05	0,05
		т=4	14			0,01		0,01
		т=8	15	0,04	0,12		0,01	0,17
		т=20	16	0,39				0,39
	Итого:		17	0,43	0,12	0,01	0,06	0,62
Трубы стальные электросварные прямошовные	В-Ст3сп ГОСТ	48х3,5	18				0,03	0,03
			19					
	Итого:		20				0,03	0,03
Всего масса металла			21	1,08	0,75	0,21	0,09	2,12
В том числе по маркам или								
С245			22	1,08	0,75	0,21	0,06	2,09
В-Ст3сп			23				0,03	0,03

*Примечание: спецификация элементов металлопроката составлена на листы 7, 8 комплекта КПТО/11/КР-4.КМ1


						КПТО/11/КР-4.КМ1	
Изм.	Кол. уч.	Лист	№ док.	Подп.	Дата		
ГИП						Комплекс по переработке рыбы	Стадия: Р; Лист: 7; Листов:
Разраб.	Андреев					Фрагмент Б. Разрезы 8-8, ..11-11 Узлы 13-22. Спецификация элементов металлопроката	
Н. контр.							


Согласовано


Взам. инв. №


Подп. и дата


Инв. № подл.

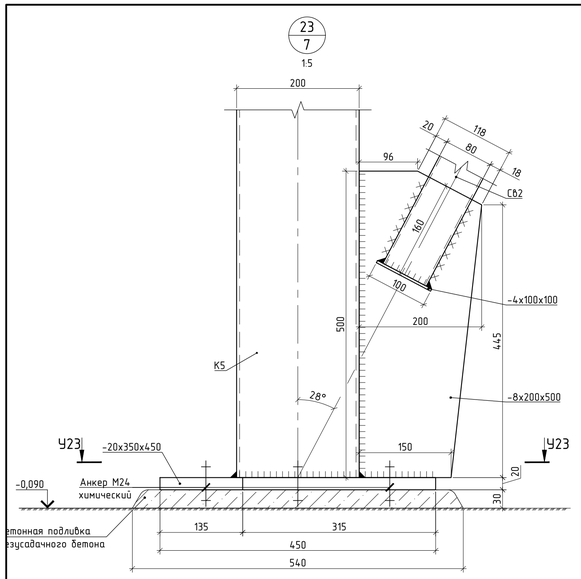

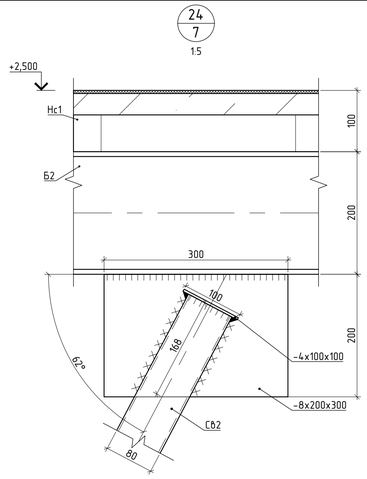


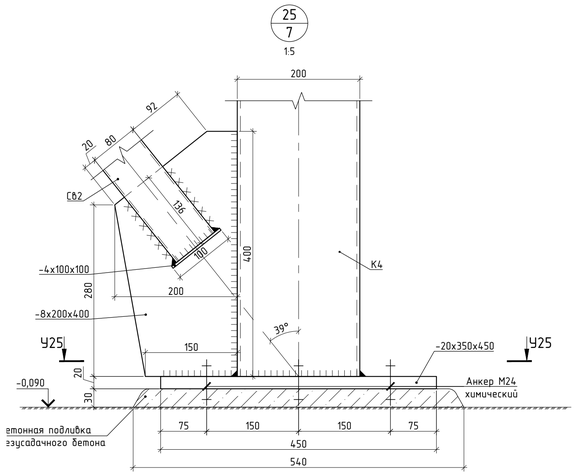

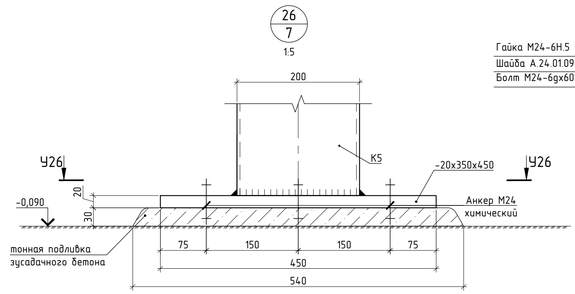


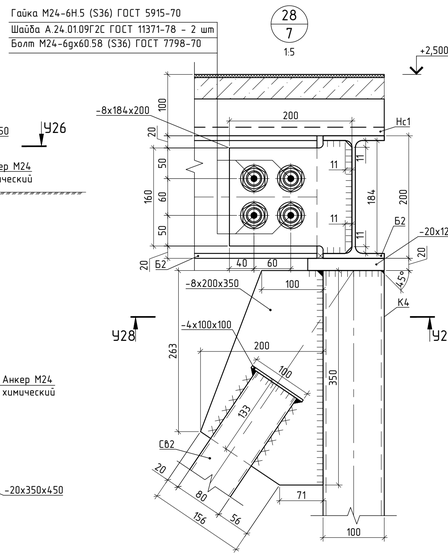


Ц23-Ц23 (1:5)

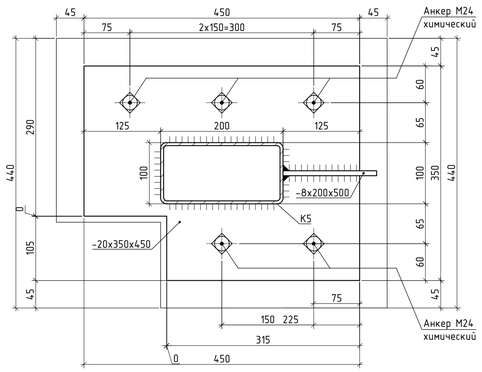


Ц25-Ц25 (1:5)

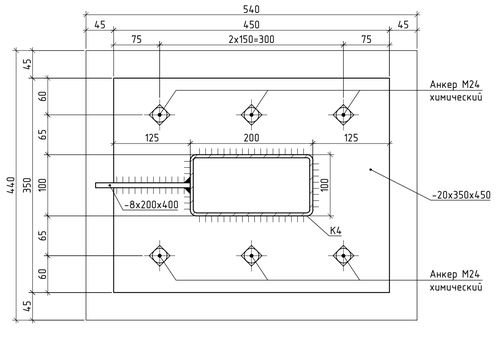



Ц26-Ц26 (1:5)

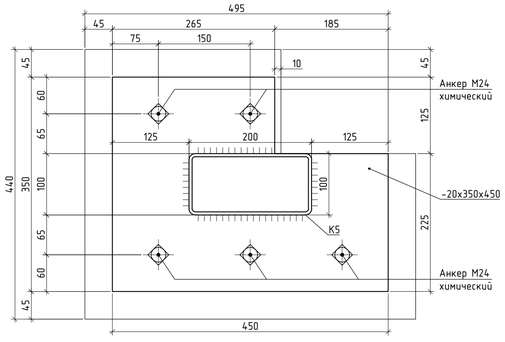


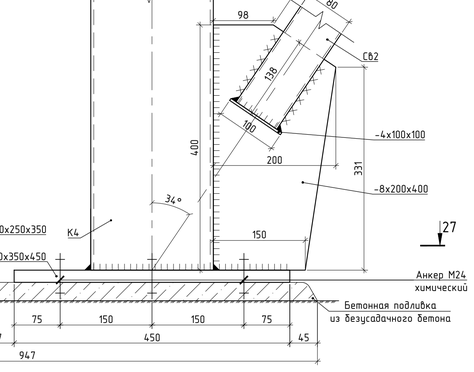

Ц27-Ц27 (1:5)

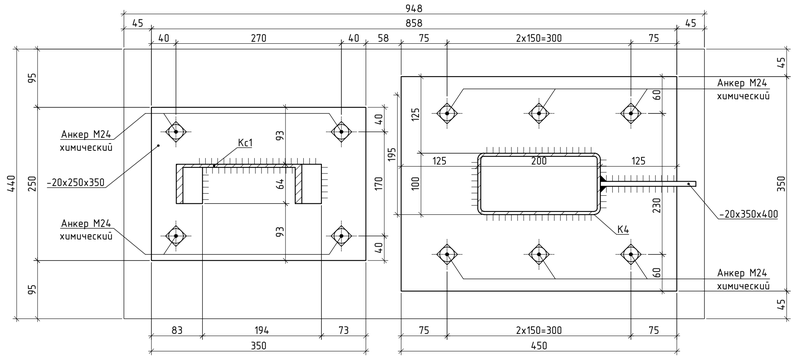

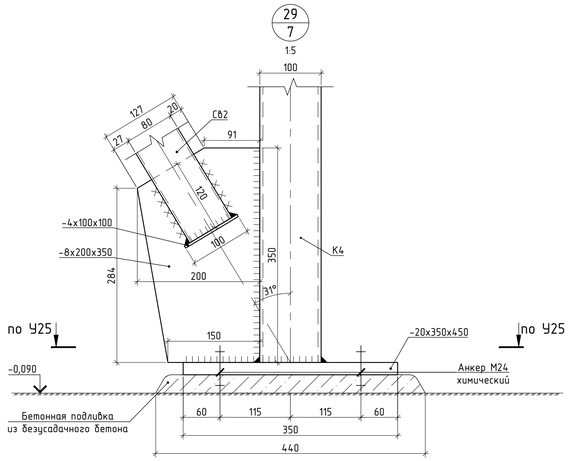

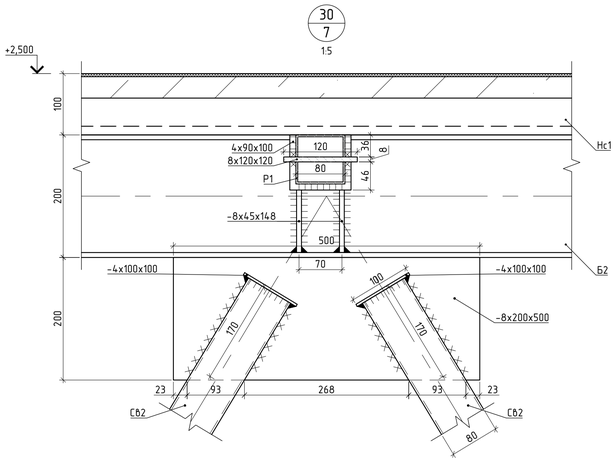

						КПТО/11/КР-4.КМ1
Изм.	Кол. уч.	Лист	№ док.	Подп.	Дата	
ГИП						Комплекс по переработке рыбы
Разраб.		Андреев				Стадия: Р; Лист: 8; Листов:
						Узлы 23-30
Н. контр.						


Согласовано

Взам. инв. №

Подп. и дата

Инв. № подл.


Фрагмент В (1:25)

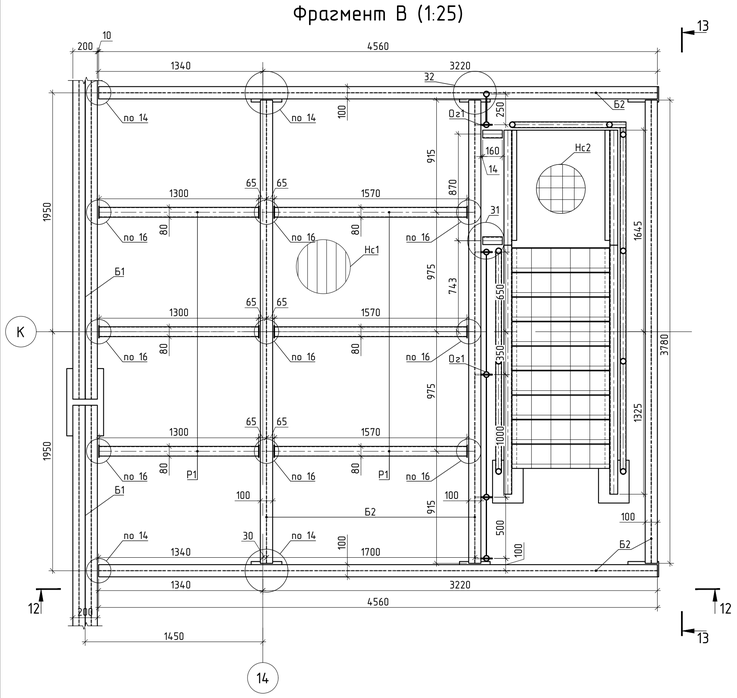

12–12 (1:50)


13–13 (1:50)

31/9 (1:5)

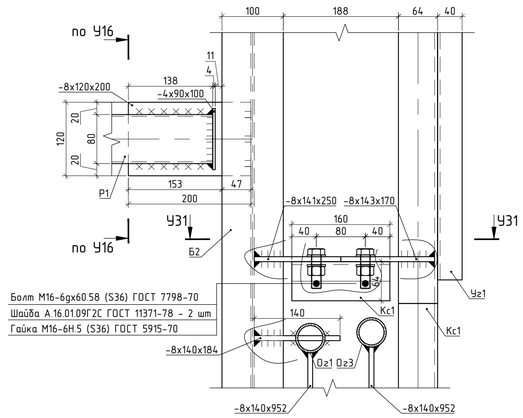


Болт М16-6gх60.58 (S36) ГОСТ 7798-70
Шайба А.16.01.09Г2С ГОСТ 11371-78 - 2 шт
Гайка М16-6Н.5 (S36) ГОСТ 5915-70

У31–У31 (1:5)

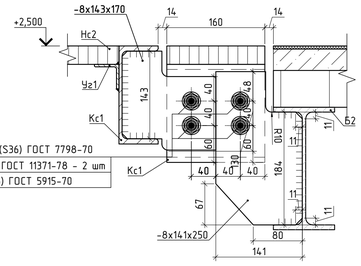


Болт М16-6gх60.58 (S36) ГОСТ 7798-70
Шайба А.16.01.09Г2С ГОСТ 11371-78 - 2 шт
Гайка М16-6Н.5 (S36) ГОСТ 5915-70


-8х143х153 (1:5)

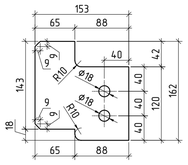

-8х141х250 (1:5)

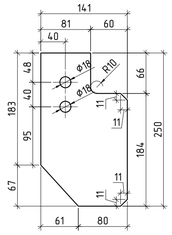


32/9 (1:5)

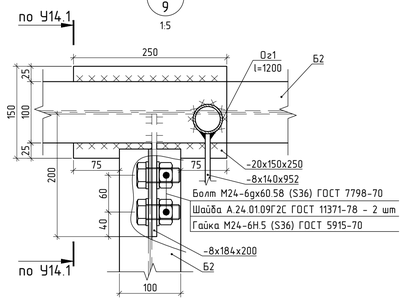


Болт М24-6gх60.58 (S36) ГОСТ 7798-70
Шайба А.24.01.09Г2С ГОСТ 11371-78 - 2 шт
Гайка М24-6Н.5 (S36) ГОСТ 5915-70


33/9 (1:5)

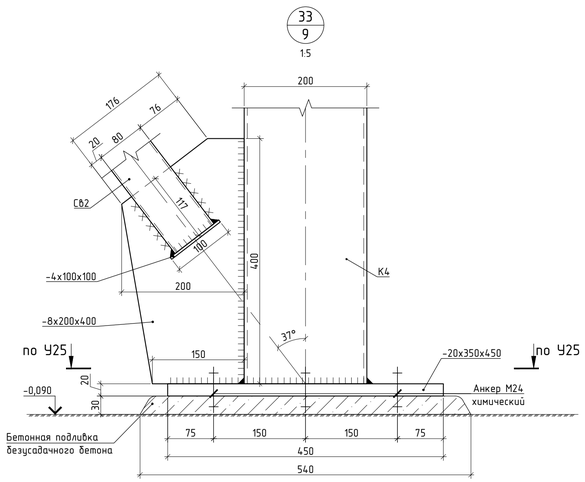

34/9 (1:5)

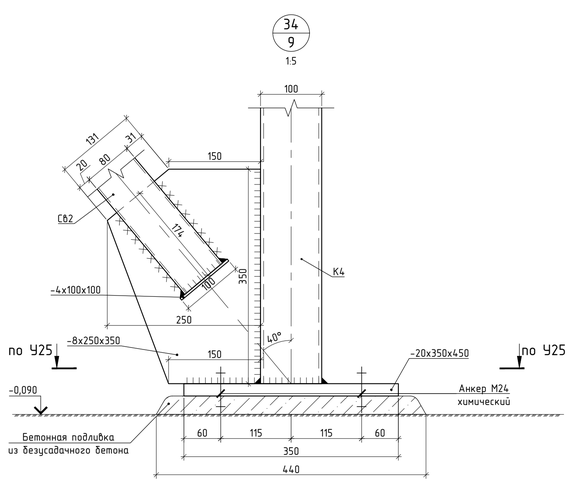

35/9 (1:5)

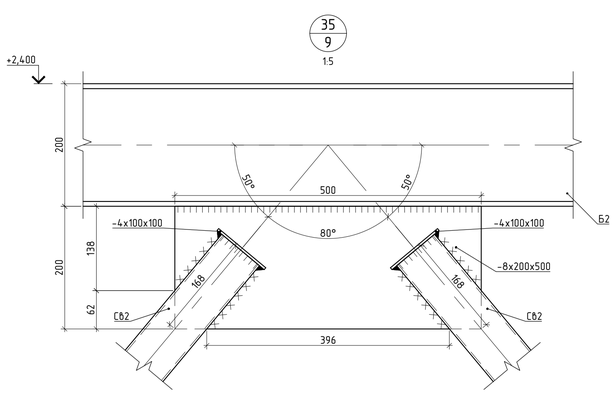

Спецификация элементов металлопроката

Наименование профиля ГОСТ, ТУ	Наименование или марка металла ГОСТ, ТУ	Номер или размер профиля, мм	Поз.	Марка металла по элементам конструкций, т				Общая масса, т
				Колонны	Балки	Распорки, стойки, связи	Ограждение	
Двутавры стальные горячекатанные по ГОСТ	С245	20Б1	1		0,44			0,44
	ГОСТ		2					
Р 57837О-2017	Итого:		3		0,44			0,44
Профили стальные гнутые замкнутые сварные квадратные и	С245	200х100х5	4	0,30				0,30
	ГОСТ		5					
	Итого:		6	0,30				0,30
Трубы стальные квадратные по	С245	80х80х3	7			0,11		0,11
	ГОСТ		8					
ГОСТ 8639-82	Итого:		9			0,11		0,11
Швеллеры стальные горячекатанные с параллельными	С245	16П	10		0,01			0,01
	ГОСТ		11					
	Итого:		12		0,01			0,01
Сталь листовая горячекатаная, по ГОСТ 19903-74	С245 ГОСТ 27772-15	t=2	13				0,04	0,04
		t=4	14			0,01		0,01
		t=8	15	0,02	0,06		0,01	0,09
		t=20	16	0,18				0,18
	Итого:		17	0,20	0,06	0,01	0,05	0,31
Трубы стальные электросварные прямошовные	В-Ст3сп	48х3,5	18				0,03	0,03
	ГОСТ		19					
	Итого:		20				0,03	0,03
Всего масса металла			21	0,51	0,50	0,11	0,08	1,19
В том числе по маркам или								
С245			22	0,51	0,50	0,11	0,05	1,16
В-Ст3сп			23				0,03	0,03

*Примечание: спецификация элементов металлопроката составлена на лист 9 комплекта КПТО/11/КР-4.КМ1

Согласовано

Взам. инв. №

Подп. и дата

Инв. № подл.

Изм.	Кол. уч.	Лист	№ док.	Подп.	Дата
ГИП					
Разраб.		Андреев			
Н. контр.					


КПТО/11/КР-4.КМ1

Комплекс по переработке рыбы


Стадия	Лист	Листов
Р	9	

Фрагмент В. Разрезы 12-12, 13-13. Узлы 31-35. Спецификация элементов металлопроката


Фрагмент Г (1:25)

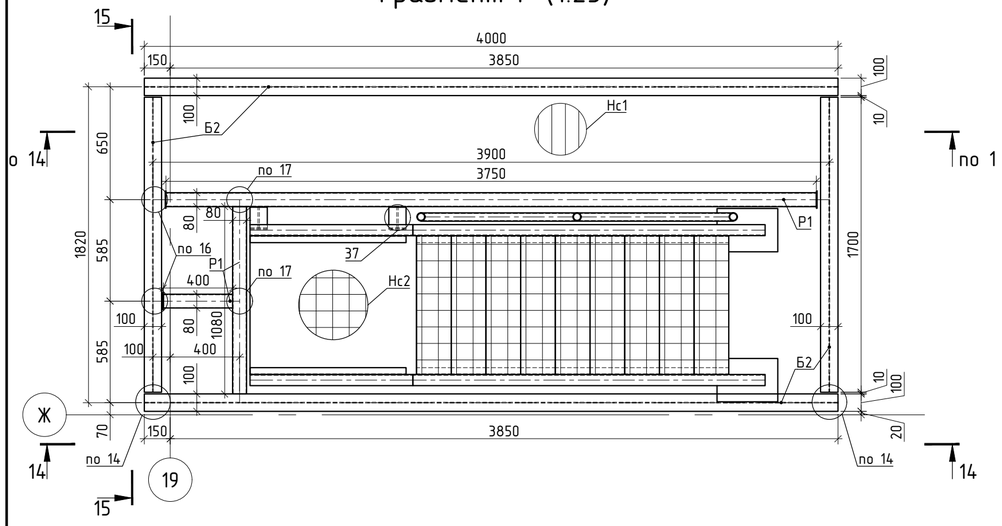

14-14 (1:50)

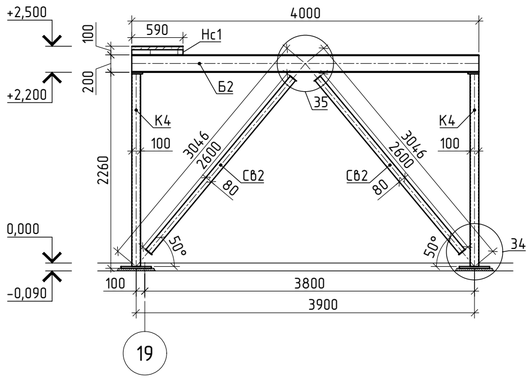


15-15 (1:50)

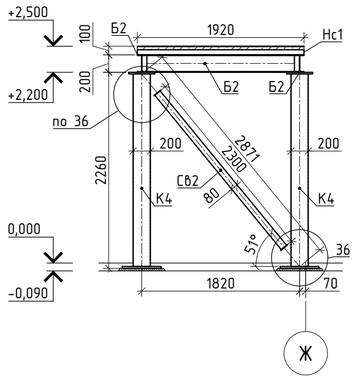


36 / 10

1:5

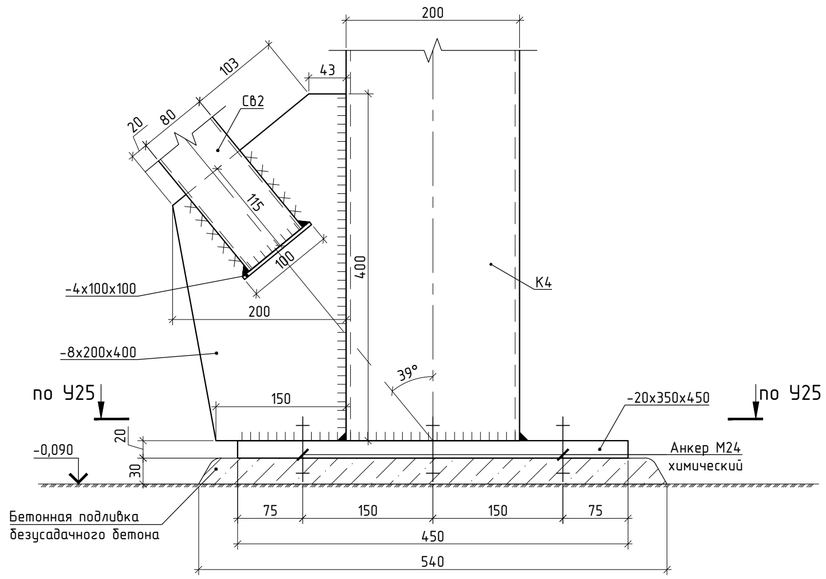


37 / 10

1:5

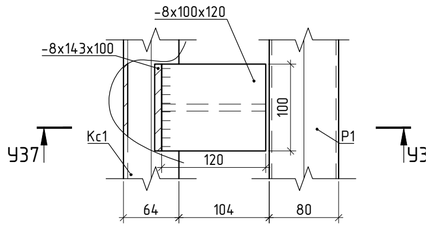

У37-У37 (1:5)

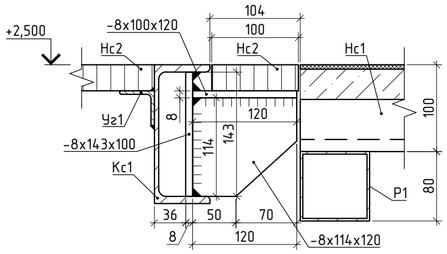

Спецификация элементов металлопроката

Наименование профиля ГОСТ, ТУ	Наименование или марка металла ГОСТ, ТУ	Номер или размер профиля, мм	Поз.	Марка металла по элементам конструкций, т				Общая масса, т
				Колонны	Балки	Распорки, стойки, связи	Ограждение	
Двутавры стальные горячекатанные по ГОСТ Р 57837О-2017	С245 ГОСТ	20Б1	1		0,24			0,24
	ГОСТ		2					
	Итого:		3		0,24			0,24
Профили стальные гнутые замкнутые сварные квадратные и	С245 ГОСТ	200х100х5	4	0,20				0,20
	ГОСТ		5					
	Итого:		6	0,20				0,20
Трубы стальные квадратные по ГОСТ 8639-82	С245 ГОСТ	80х80х3	7			0,04		0,04
	ГОСТ		8					
	Итого:		9			0,04		0,04
Сталь листовая горячекатаная, по ГОСТ 19903-74	С245 ГОСТ 27772-15	t=4	10			0,004		0,00
		t=8	11	0,03	0,03			0,06
		t=20	12	0,12				0,12
	Итого:		13	0,15	0,03	0,004		0,19
Всего масса металла			14	0,36	0,27	0,041		0,66
В том числе по маркам или								
С245			15	0,36	0,27	0,041		0,66

*Примечание: спецификация элементов металлопроката составлена на лист 10 комплекта КПТО/11/КР-4.КМ1

Согласовано

Взам. инв. №

Подп. и дата

Инв. № подл.

Изм.	Кол. уч	Лист	№ док.	Подп.	Дата
ГИП					
Разраб.		Андреев			
Н. контр.					


КПТО/11/КР-4.КМ1

Комплекс по переработке рыбы

Стадия	Лист	Листов
Р	10	

Фрагмент Г. Разрезы 14-14, 15-15. Узлы 36, 37. Спецификация элементов металлопроката

Фрагмент Д (1:10)

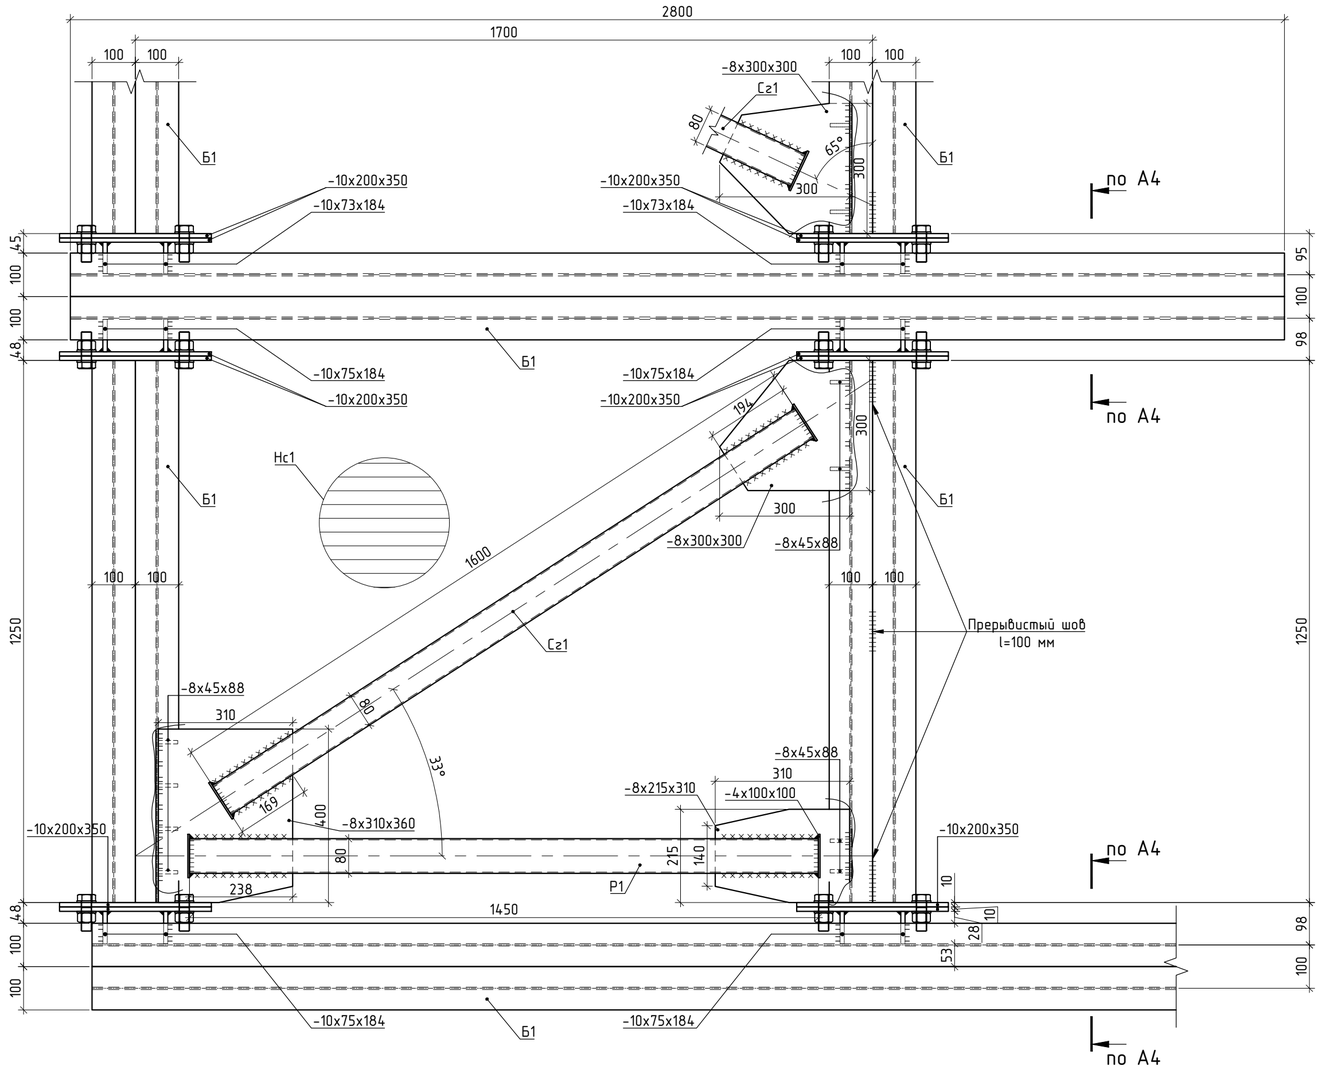

						КПТО/11/КР-4.КМ1	
Изм.	Кол. уч	Лист	№ док.	Подп.	Дата		
ГИП						Комплекс по переработке рыбы	Стадия: Р; Лист: 11; Листов:
Разраб.		Андреев					
Н. контр.						Фрагмент Д	

Согласовано

Взам. инв. №

Подп. и дата

Инв. № подл.