Ведомость рабочих чертежей комплекта

Лист	Наименование	Примечание
1	Общие данные	изм.02 (Зам.)
2	Схема расположения стоек. Схема расположения мауэрлата. Спецификации	изм.02 (Зам.)
3	Схема расположения связей между нижними поясами ферм Ф1, Ф2, Ф3. Схема расположения	
	ферм, косоуров, каньковых балок	
4	Разрезы 1-1, 2-2, 7-7, 8-8, 9-9	изм.02 (Зам.)
5	Разрезы 3-3, 4-4, 5-5, 6-6	
6	Разрезы 10-10, 11-11, 12-12, 13-13, 14-14	
7	Узлы	
8	Фрагмент 1, Фрагмент 2	
9	Фрагмент 3	
10	Фрагмент 4	изм.01 (Зам.)
11	Фермы Ф1, Ф2, Ф3	
12	Фрагмент 5	

Примечание: шпильки баз стоек установить на химических анкерах

Согласовано

Взам. инв. №

Подп. и дата

Инв. № подл.

						М16-КД
02		Зам.				
Изм.	Кол. уч	Лист	№ док.	Подп.	Дата	
ГИП						Стадия: Р; Лист: 1; Листов:
Разраб.		Андреев				
						Общие данные
Н. контр.						

Схема расположения стоек (1:30)


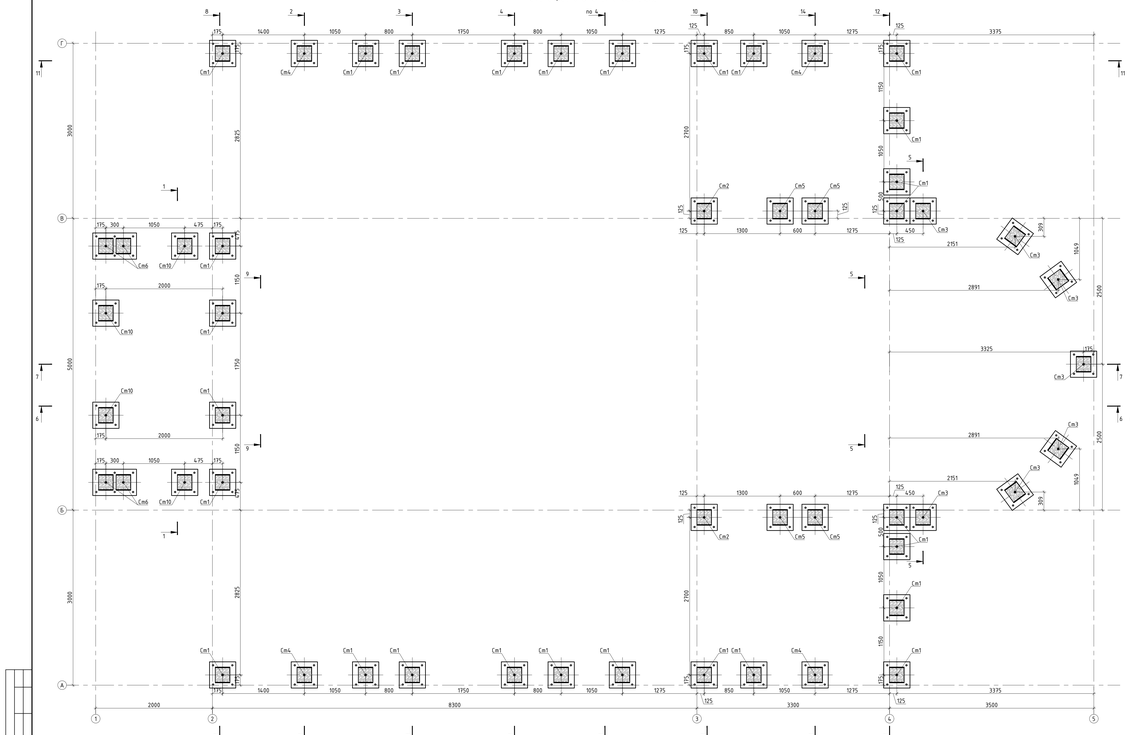


Схема расположения мауэрлата (1:30)

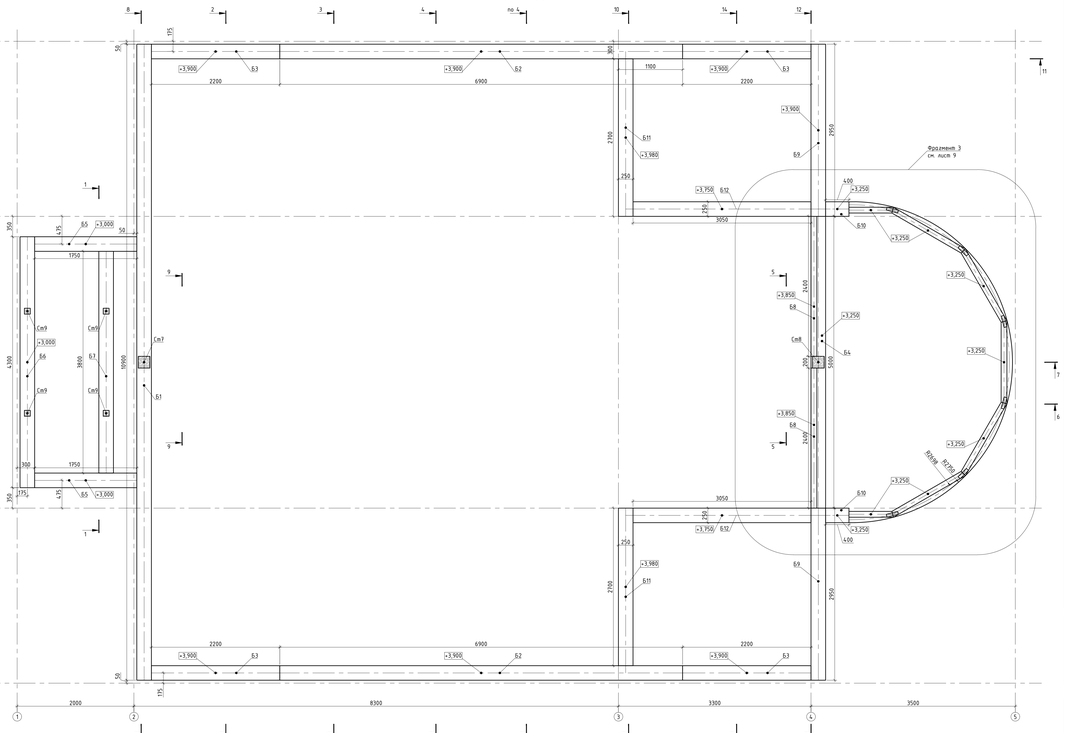

Спецификация

Поз.	Обозначение	Наименование	Кол.	Объем, м³	Итого, м³
Ст1	Стойка	250х250х3670	28	0,23	6,42
	База стойки	Тип 1	28		
Ст3	Стойка	250х250х3000	7	0,19	1,31
	База стойки	Тип 1	7		
Ст4	Стойка	250х250х3455	4	0,22	0,86
	База стойки	Тип 1	4		
Ст5	Стойка	250х250х3520	6	0,22	1,32
	База стойки	Тип 1	6		
Ст6	Стойка	250х250х3000	4	0,19	0,75
	База стойки	Тип 2	2		
Ст7	Стойка для К81	200х200х350	1	0,01	0,01
Ст8	Стойка для К82	200х200х500	1	0,02	0,02
Ст9	Стойка для Кс2	100х100х828	4	0,01	0,03
Ст10	Стойка	250х250х2770	4	0,17	0,69
	База стойки	Тип 1	4		
Б1	Мауэрлат	250х250х10900	1	0,68	0,68
Б2	Мауэрлат	250х250х6900	2	0,43	0,86
Б3	Мауэрлат	215х250х2200	4	0,12	0,47
Б4	Мауэрлат	250х250х5000	1	0,31	0,31
Б5	Мауэрлат	250х250х1750	2	0,11	0,22
Б6	Мауэрлат	250х250х4300	1	0,27	0,27
Б7	Мауэрлат	250х250х3800	1	0,24	0,24
Б8	Мауэрлат	250х250х2400	2	0,15	0,30
Б9	Мауэрлат	250х250х2950	2	0,18	0,37
Б10	Мауэрлат	250х250х400	2	0,03	0,05
Б11	Мауэрлат	250х250х2700	2	0,17	0,34
Б12	Мауэрлат	250х250х3050	2	0,19	0,38
Б13	Мауэрлат	250х250х2200	2	0,14	0,28
К81	Коньковая балка	200х200х3475	1	0,14	0,14
К82	Коньковая балка	200х200х2400	3	0,10	0,29
Кс13	Косоур	200х100х1833	12	0,04	0,44
Кс14	Косоур	200х100х1860	8	0,04	0,30
Кс15	Косоур	200х100х1753	4	0,04	0,14
Кс2	Косоур	200х100х2827	4	0,06	0,23
Кс3	Косоур	200х100х835	2	0,02	0,03
Кс4	Косоур	200х100х835	2	0,02	0,03
Кс5	Косоур	200х100х3399	2	0,07	0,14
Кс6	Косоур	200х100х3285	2	0,07	0,13
Кс7	Косоур	200х100х710	2	0,01	0,03
Кс8	Косоур	200х100х2738	5	0,06	0,28
Кл1	Деталь кольца	250х200х1424	5	0,07	0,36
Кл2	Деталь кольца	250х200х662	2	0,03	0,07
Ен1	Ембова	200х100х2451	4	0,05	0,20
Ен2	Ембова	200х100х2463	4	0,05	0,20
Ен3	Ембова	200х100х2320	4	0,05	0,19

Спецификация баз стоек

Тип	Внутр. типа	А, мм	В, мм	Т, мм	n, шт	Масса, кг	$n_{общ}$, шт	Масса общая, кг
Тип 1	Вертикальные (2 шт)	250	300	10	2	0,118	51	6,005
	Горизонтальный	450	450	10	1	0,159	51	8,107
Тип 2	Вертикальные (2 шт)	250	300	10	4	0,236	2	0,471
	Горизонтальный	350	450	10	1	0,265	2	0,530

Спецификация материалов болтокомплекта БК-1

Поз.	Обозначение	Наименование	Кол.	Масса ед. кг	Примечания
		Шпилька М20-6g х 250.58 ГОСТ22042- 76	4		шт
		Гайка М20	4		шт
		Контргайка М20	4		шт
		Шайба М20	4		шт

Примечание: количество болтокомплектов БК-1 составляет 51 шт

Спецификация материалов болтокомплекта БК-2

Поз.	Обозначение	Наименование	Кол.	Масса ед. кг	Примечания
		Шпилька М20-6g х 250.58 ГОСТ22042- 76	6		шт
		Гайка М20	6		шт
		Контргайка М20	6		шт
		Шайба М20	6		шт

Примечание: количество болтокомплектов БК-2 составляет 2 шт

								М16-КД	
Изм.	Кол. уч.	Лист	№ док.	Подп.	Дата				
ГИП									
Разраб.		Андреев				Стадия	Лист	Листов	
						Р	2		
Н. контр.									
						Схема расположения стоек. Схема расположения мауэрлата. Спецификации			

Инв. № подл. | Подп. и дата | Взам. инв. № | Согласовано

Схема расположения связей меду нижними поясами ферм Ф1, Ф2, Ф3 (1:30)





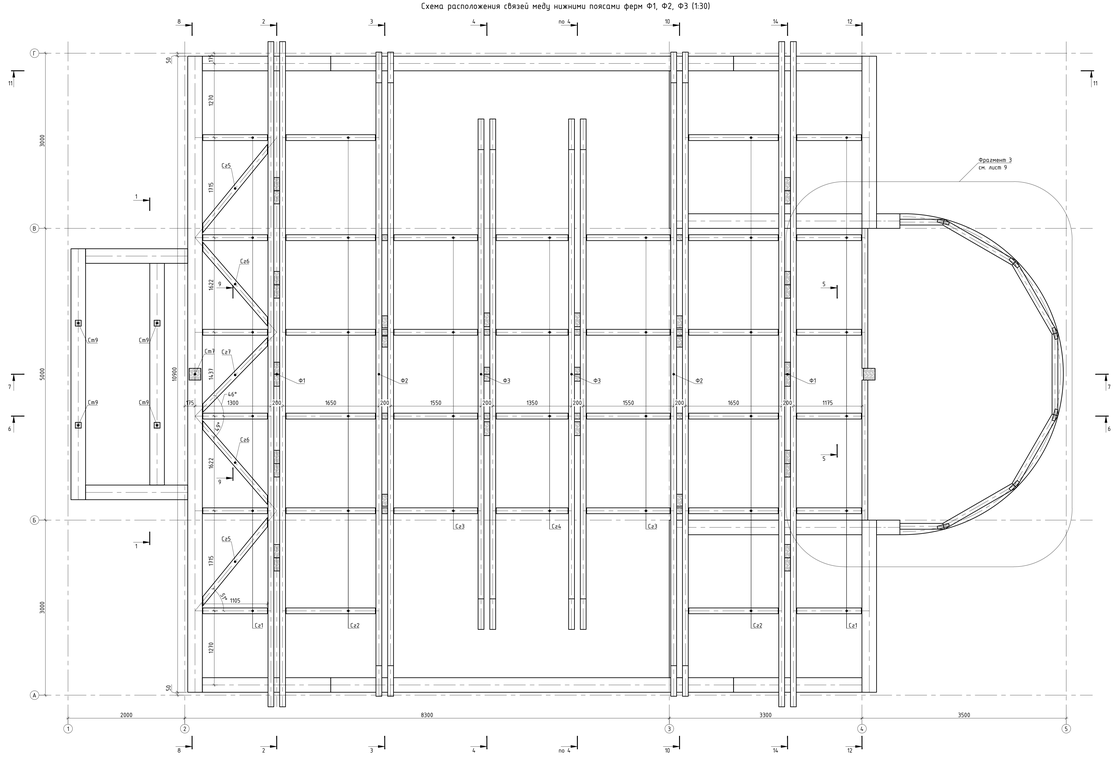



Схема расположения ферм, косоуров, канькавых балок (1:30)

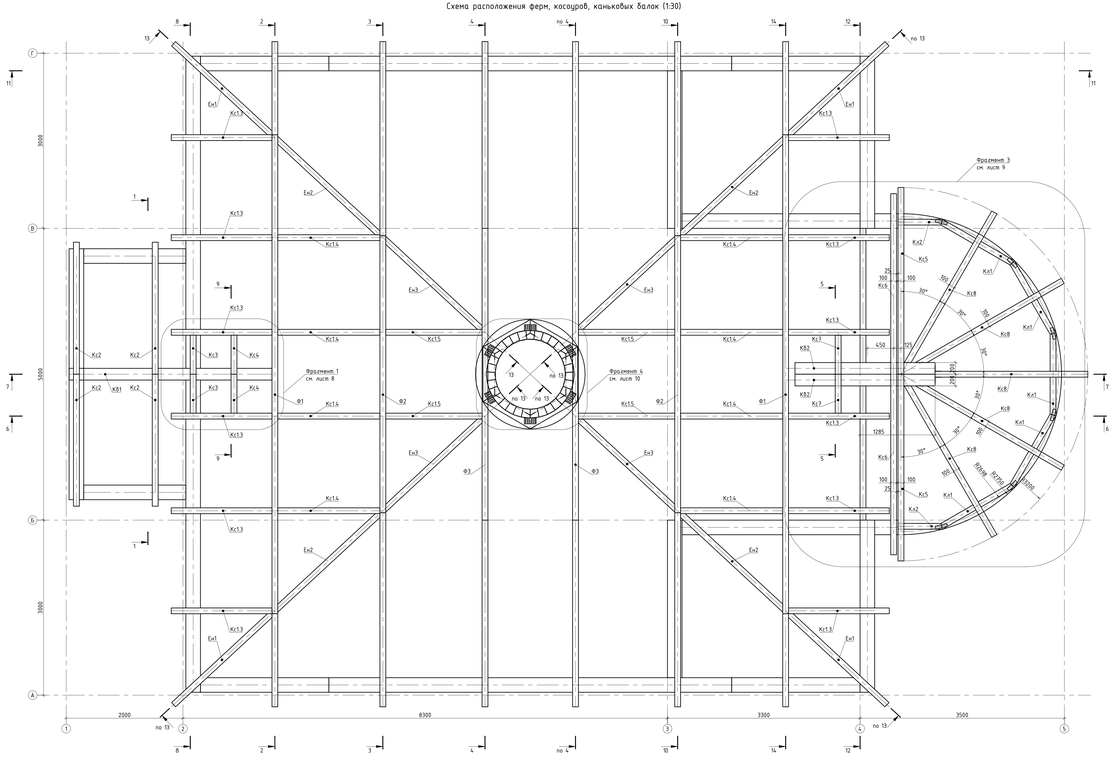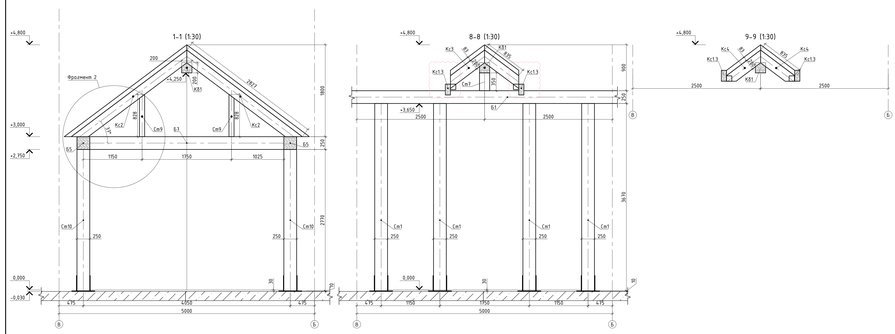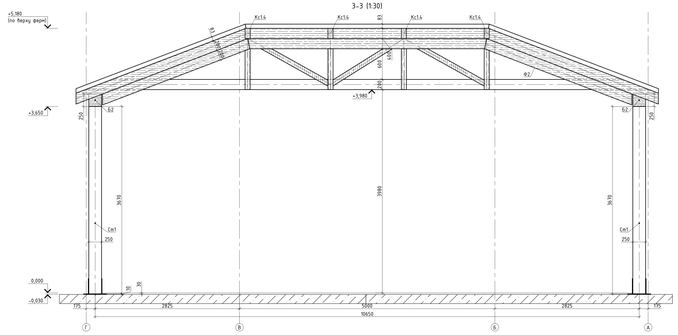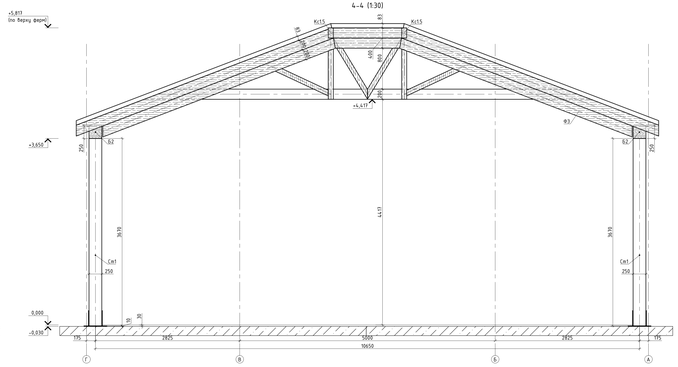



1-1 (1:30)
Фрагмент 2
+3.800
+3.000
+2.750
0.000
-0.030
Кс1
Кс2
Кс3
Кс9
Кс10
3-3 (1:30)
+5,180
(по верху фермы)
+3,650
0,000
-0,030
Кс1.4
Кс1.5
Кс1.6
Ф2
Ф3
Ст1
Ст2
Ст3
3675
3985
250
200
30
175
2825
5000
10650
Г
В
Б
А



4-4 (1:30)
+5,813
(по верху фермы)
+3,650
0,000
-0,030
Кс1.5
Ф3
Ст1
Ст2
Ст3
4315
3675
250
200
30
175
2825
5000
10650
Г
В
Б
А

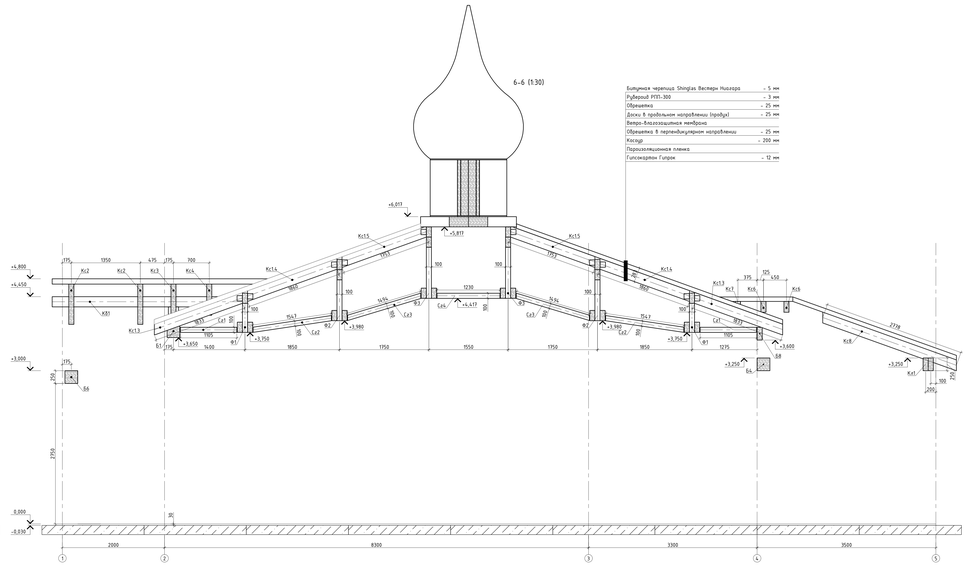
6-6 (1:30)
+6,013
+5,813
+4,800
+4,650
+3,050
0,000
-0,030
Кс1.2
Кс1.3
Кс1.4
Кс1.5
Кс1.6
Кс1.7
Кс1.8
Кс1.9
Кс1.10
Кс1.11
Кс1.12
Кс1.13
Кс1.14
Кс1.15
Кс1.16
Кс1.17
Кс1.18
Кс1.19
Кс1.20
Кс1.21
Кс1.22
Кс1.23
Кс1.24
Кс1.25
Кс1.26
Кс1.27
Кс1.28
Кс1.29
Кс1.30
Кс1.31
Кс1.32
Кс1.33
Кс1.34
Кс1.35
Кс1.36
Кс1.37
Кс1.38
Кс1.39
Кс1.40
Кс1.41
Кс1.42
Кс1.43
Кс1.44
Кс1.45
Кс1.46
Кс1.47
Кс1.48
Кс1.49


10–10 (1:30)

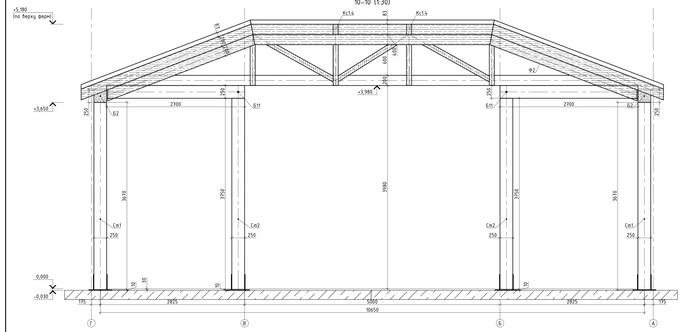


14–14 (1:30)

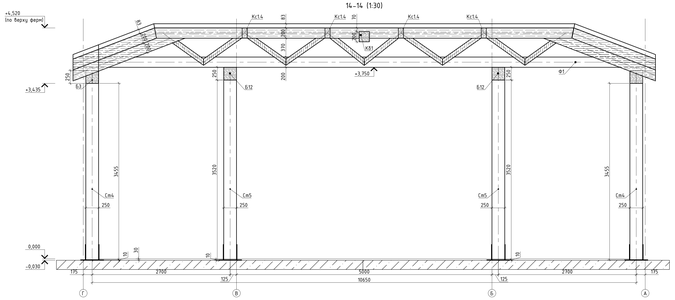


13–13 (1:30)
(по оси Ен1, Ен2, Ен3, конструкция купола не показана)

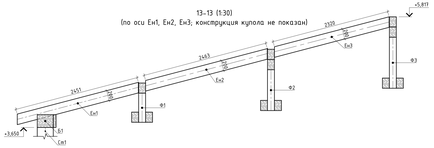

11–11 (1:30)

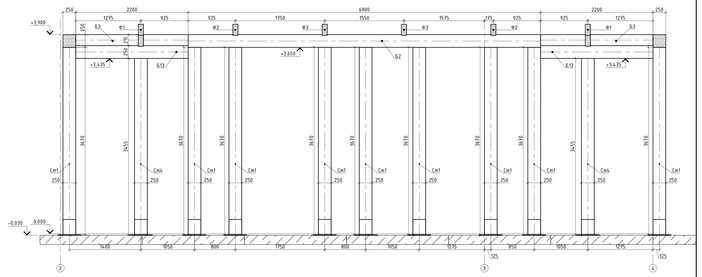

12–12 (1:30)

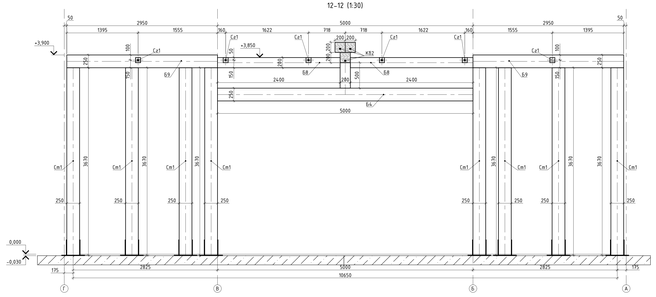

							М16-КД	
Изм.	Кол. уч.	Лист	№ док.	Подп.	Дата			
ГИП								
Разраб.		Андреев				Стадия	Лист	Листов
						Р	6	
						Разрезы 10-10, 11-11, 12-12, 13-13, 14-14		
Н. контр.								

Согласовано

Инв. № подл. | Подп. и дата | Взам. инв. №

Схема крепления раскосов ферм, косоуров, ендовы к мауэрлату (1:10)



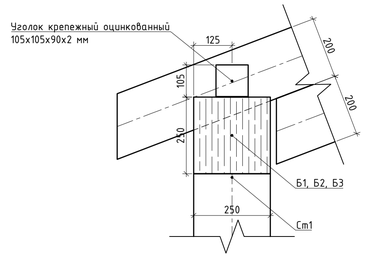



Схема крепления связей к нижнему поясу ферм и мауэрлату (1:10)

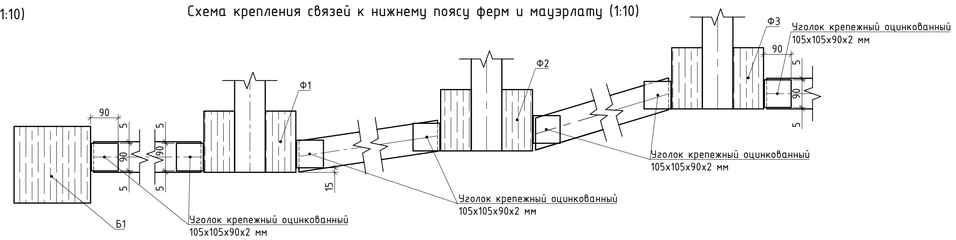


Дт1 (1:5)
-2х150х320

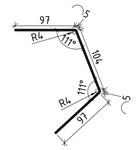

Дт2 (1:5)
-2х150х320

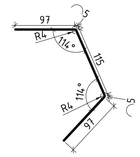

Дт3 (1:5)
-2х200х240

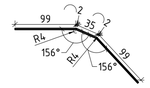

У1-У1 (1:10)

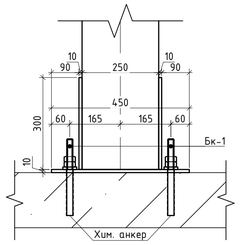


Схема крепления горизонтальных связей Сг1 и Сг2 к мауэрлату Б1 (1:10)



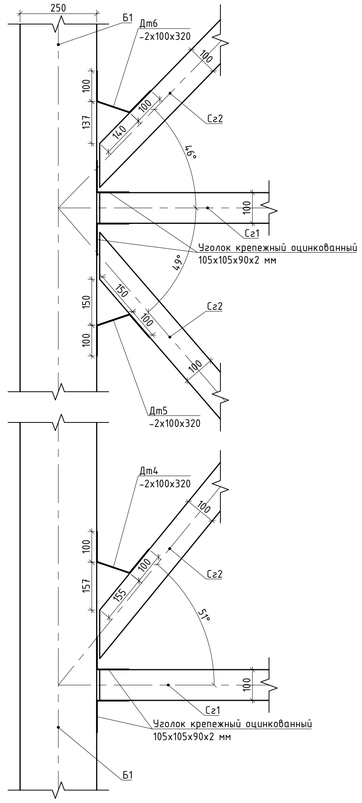



Схема крепления горизонтальных связей Сг1 и Сг2 к мауэрлату Б1 (1:10)

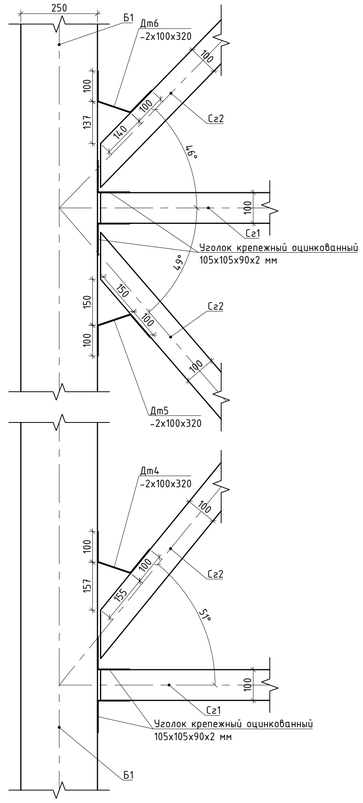


Дт6 (1:5)
-2х100х320

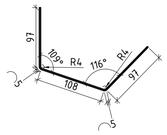


Дт5 (1:5)
-2х100х320

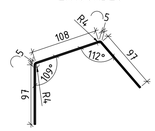


Дт4 (1:5)
-2х100х320

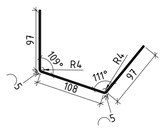


База стоек. Тип 1 (1:10)

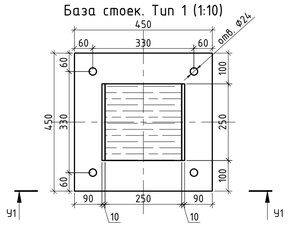


У6-У6 (1:10)

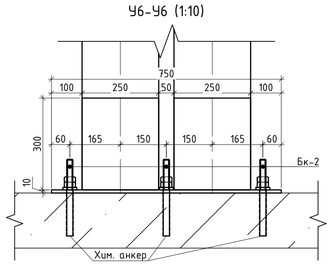


База стоек. Тип 2 (1:10)

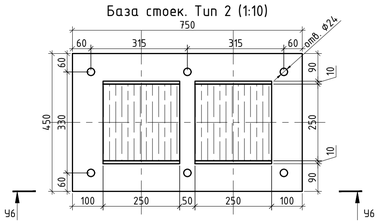


Узел крепления ендовы и раскосов к фермам (1:10)

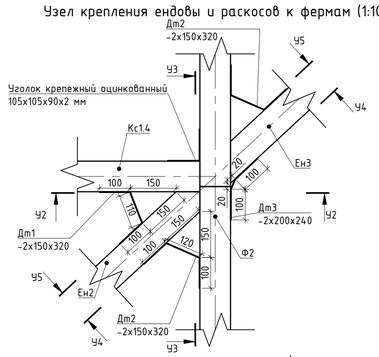


У2-У2 (1:10)

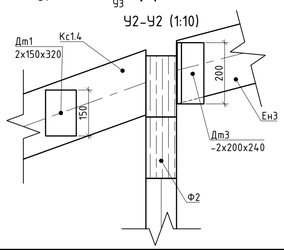


У3-У3 (1:10)

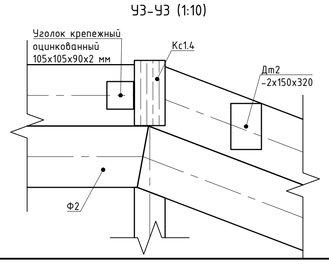

У4-У4 (1:10)

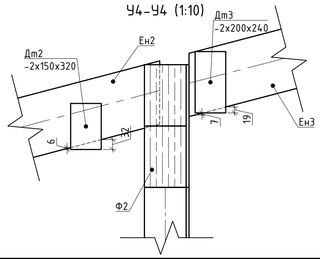

У5-У5 (1:10)

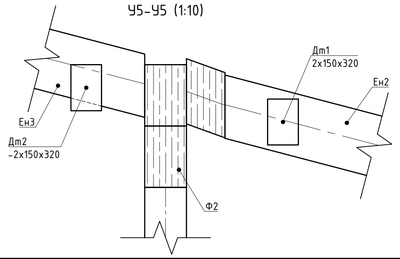


Согласовано


Инв. № подл. | Подп. и дата | Взам. инв. №

							М16-КД
Изм.	Кол. уч.	Лист	№ док.	Подп.	Дата		
ГИП						Стадия: Р	Лист: 7
Разраб.	Андреев						
Н. контр.						Узлы	


Фрагмент 1 (1:10)

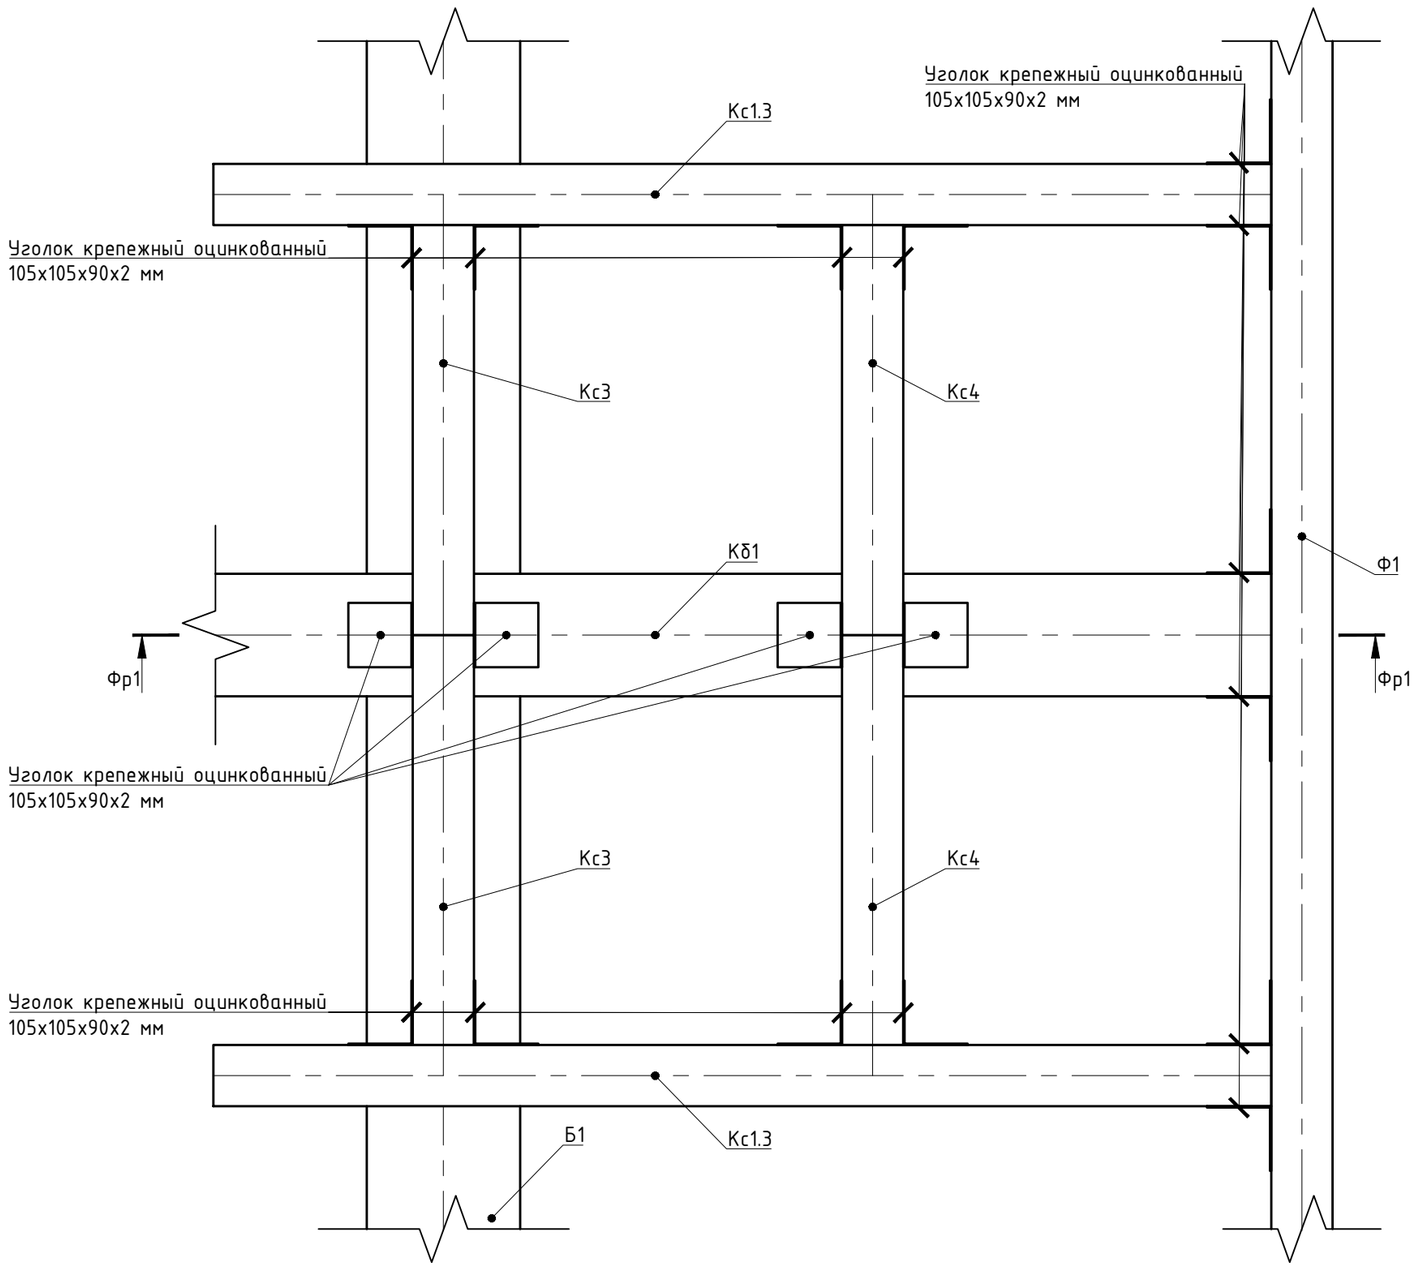

Фр1–Фр1 (1:10)

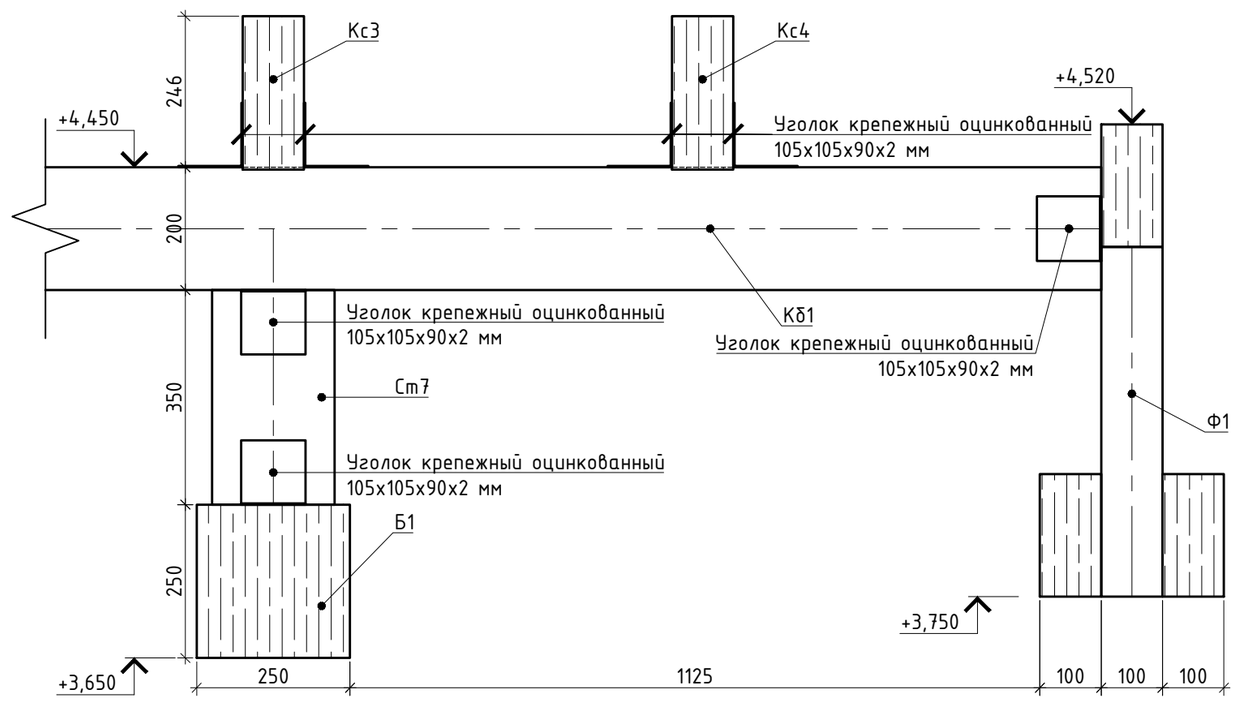

Фрагмент 2 (1:10)

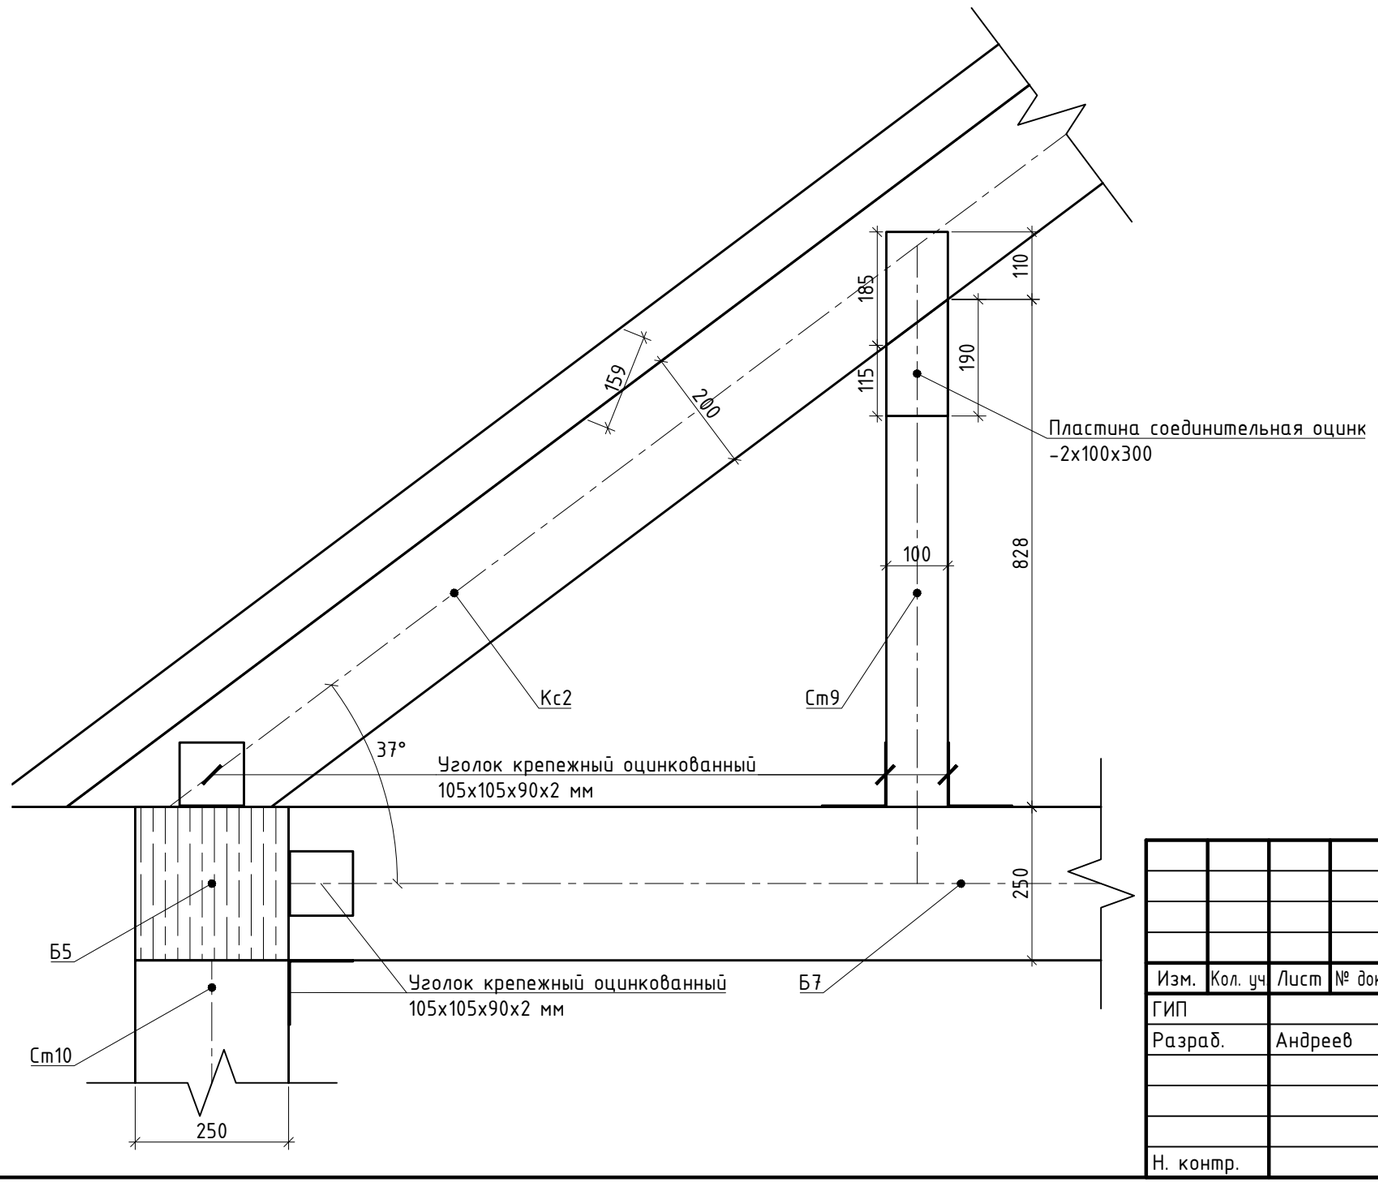

Согласовано


Взам. инв. №

Подп. и дата

Инв. № подл.


						М16-КД
Изм.	Кол. уч	Лист	№ док.	Подп.	Дата	
ГИП						Стадия: Р; Лист: 8; Листов:
Разраб.		Андреев				
Н. контр.						Фрагмент 1, Фрагмент 2

Фрагмент 3 (1:30)

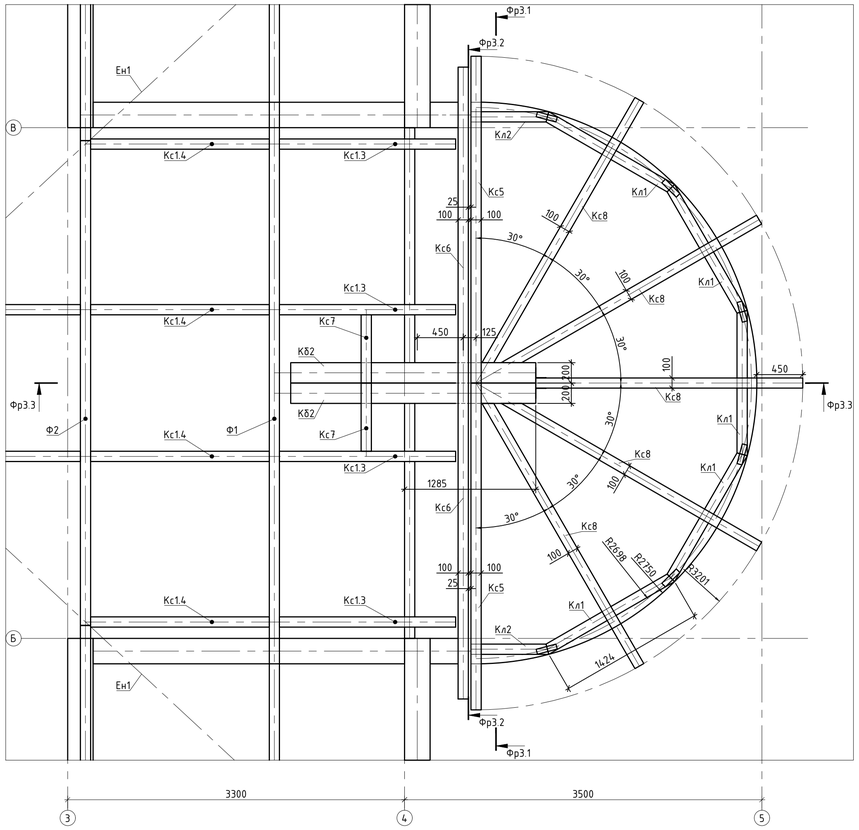


Узел "А"

1:10

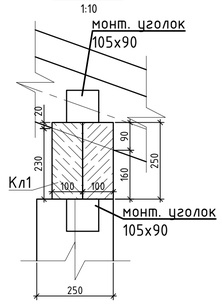


Фр3.3–Фр3.3 (1:30)

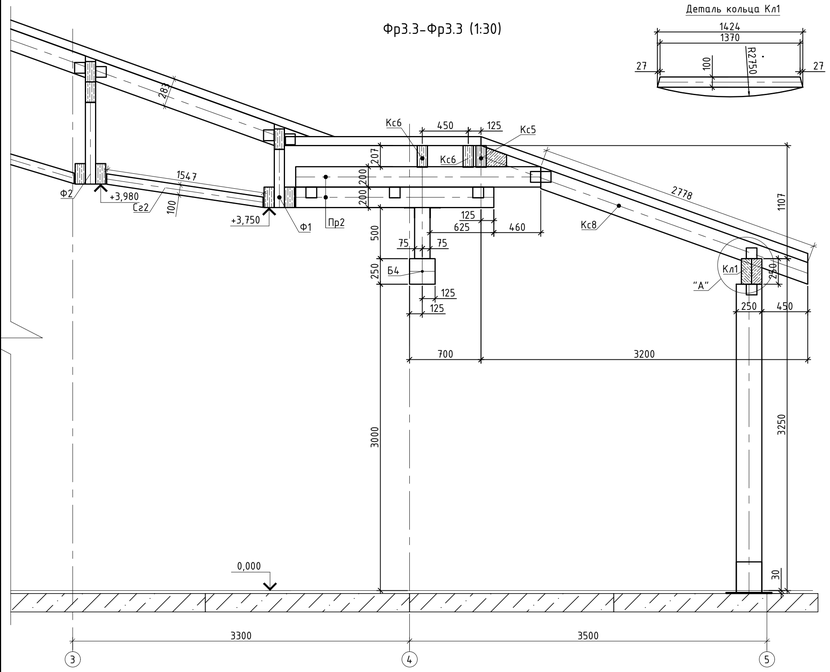


Деталь кольца Кл1

Фр3.2–Фр3.2 (1:30)

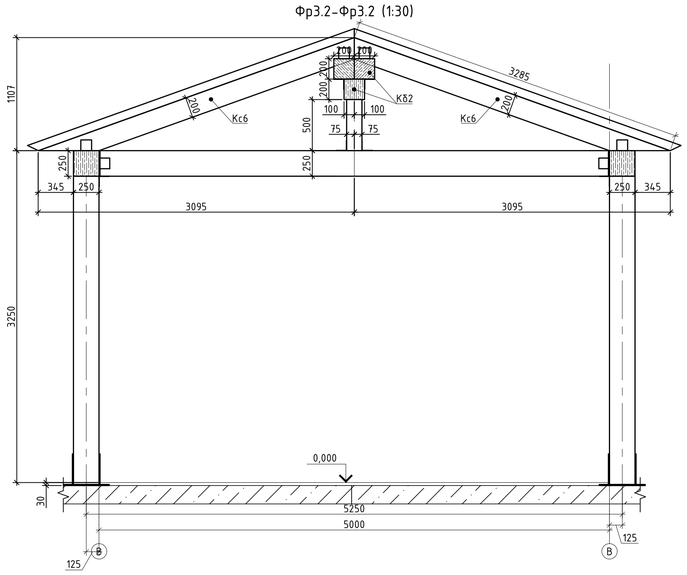

Фр3.1–Фр3.1 (1:30)

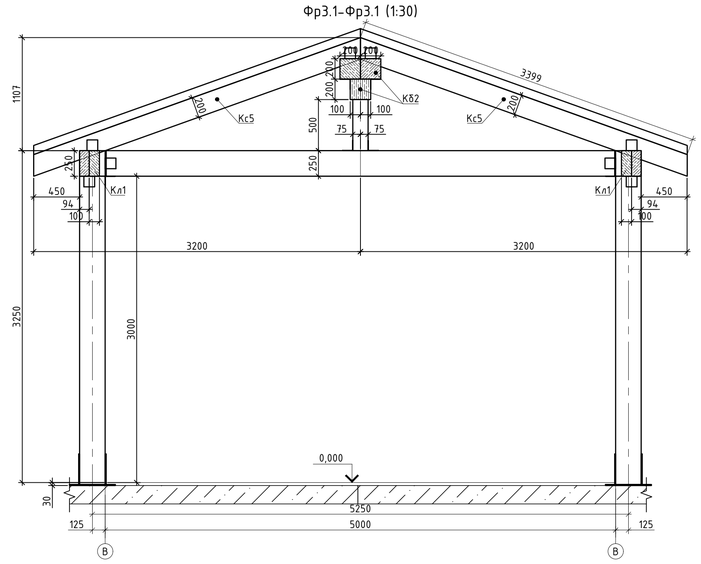

							М16-КД
Изм.	Кол. уч.	Лист	№ док.	Подп.	Дата		
ГИП						Стадия: Р	Лист: 9	Листов:
Разраб.		Андреев					
Н. контр.						Фрагмент 3. Узел А	


Согласовано

Взам. инв. №


Подп. и дата

Инв. № подл.


Фрагмент 4 (1:10)

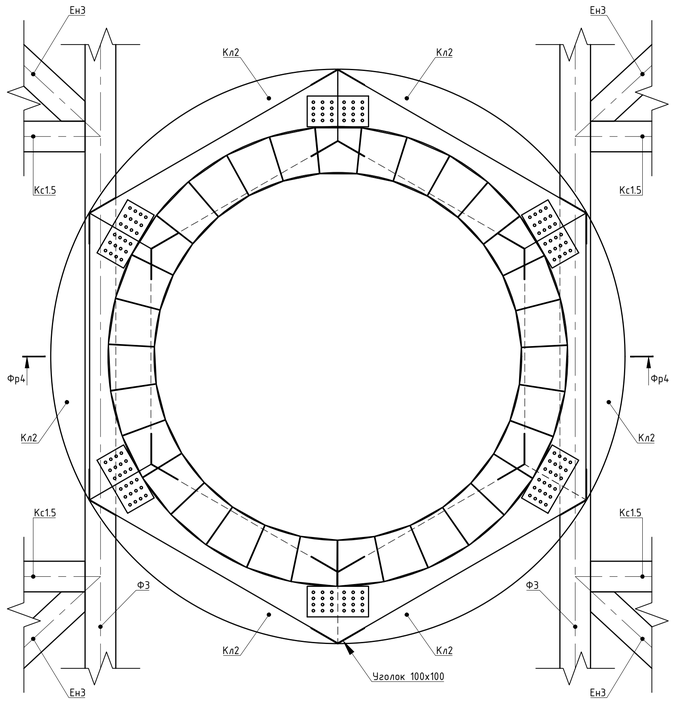


Деталь Кл4 (1:10)

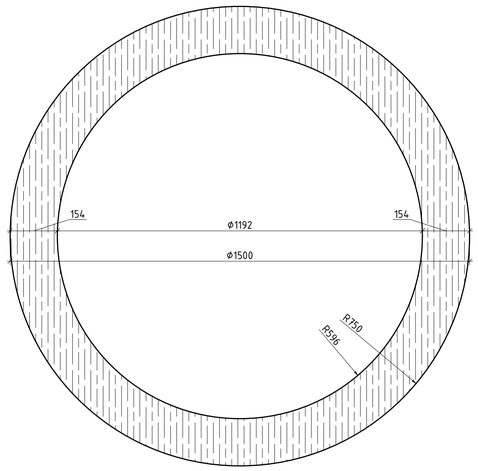


Деталь Кл5 (1:10)

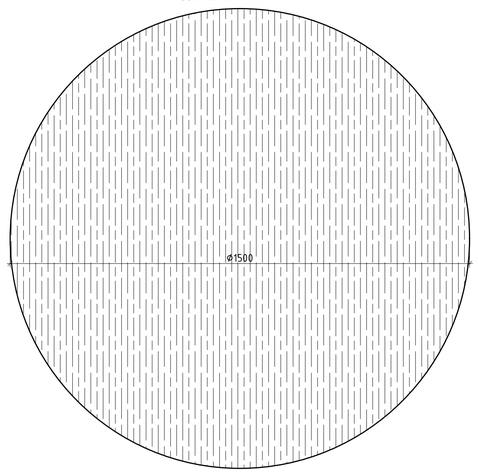


Фр4.1-Фр4.1 (1:10)

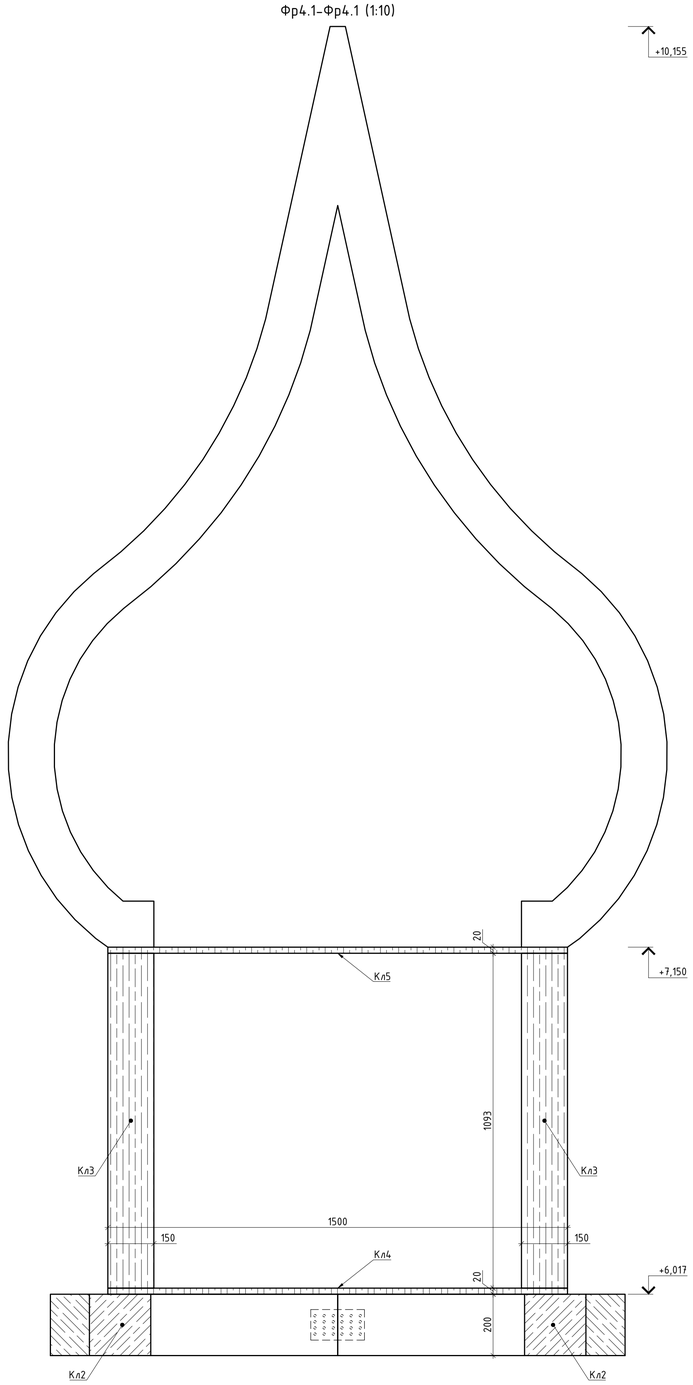

Деталь Кл3 (1:2)

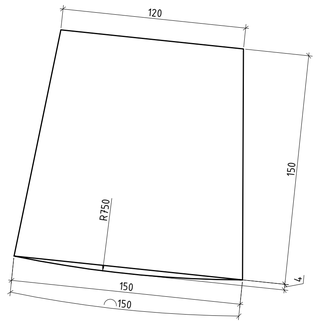

Деталь кольца Кл2 (1:5)

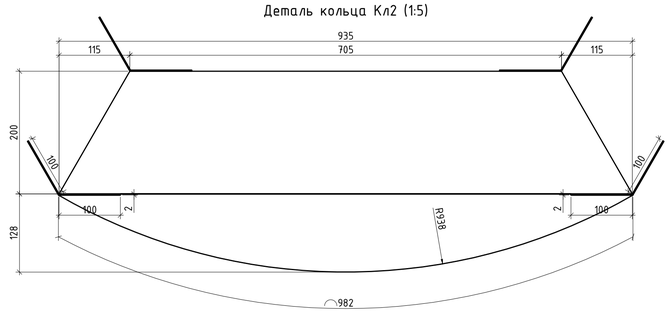

Спецификация фрагмента 4 (конструкции купола)

Поз.	Обозначение	Наименование	Кол.	Объем, м^3	Итого, м^3
Кл2	Деталь кольца	200х328х935	6	0,062	0,372
Кл3	Деталь кольца	150х154х1093	31	0,026	0,806
Кл4	Кольцо	20х154х1500	1	0,005	0,005
Кл5	Кольцо	20х1500х1500	1	0,045	0,045

Согласовано


Взам. инв. №


Подп. и дата

Инв. № подл.

						М16-КД		
01		Зам.						
Изм.	Кол. уч.	Лист	№ док.	Подп.	Дата			
ГИП							Стадия	Лист	Листов
Разраб.		Андреев					Р	10	
						Фрагмент 4			
Н. контр.									


Ферма Ф1 (1:10)

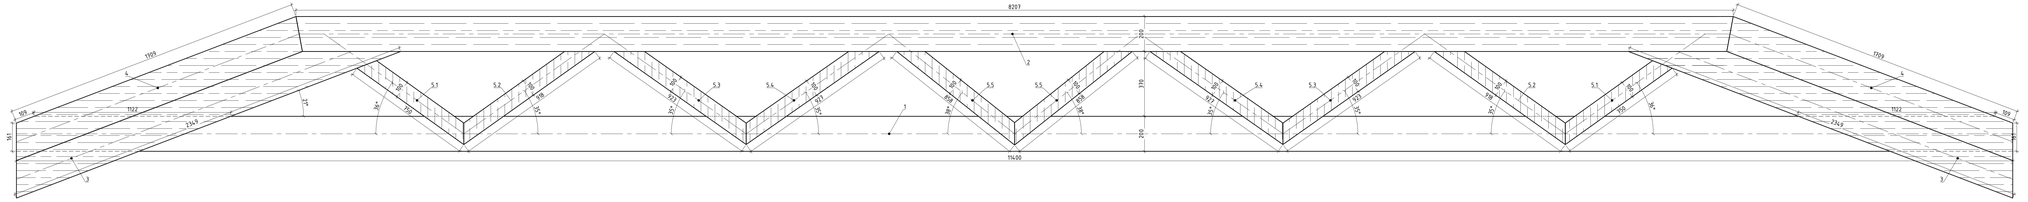


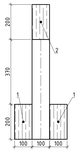

Спецификация фермы Ф1					
Поз.	Обозначение	Наименование	Кол.	Объем, м³	Итого, м³
1		Нижний пояс	2	0,23	0,46
2		Верхний пояс	1	0,16	0,16
3		Раскос	2	0,05	0,09
4		Раскос	2	0,03	0,07
5.1		Раскос	2	0,01	0,02
5.2		Раскос	2	0,01	0,02
5.3		Раскос	2	0,01	0,02
5.4		Раскос	2	0,01	0,02
5.5		Раскос	2	0,01	0,02


Ферма Ф2 (1:10)

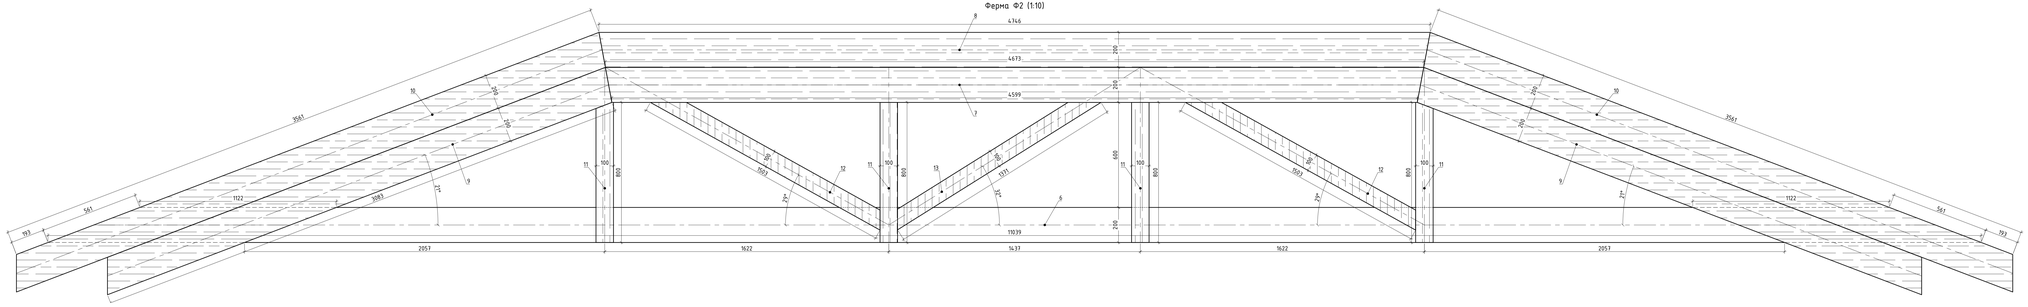


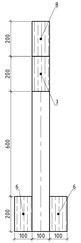

Спецификация фермы Ф2					
Поз.	Обозначение	Наименование	Кол.	Объем, м³	Итого, м³
6		Нижний пояс	2	0,22	0,44
7		Верхний пояс	1	0,09	0,09
8		Верхний пояс	1	0,09	0,09
9		Раскос	2	0,06	0,12
10		Раскос	2	0,07	0,14
11		Стойка	4	0,01	0,03
12		Раскос	2	0,02	0,03
13		Раскос	1	0,01	0,01

Ферма Ф3 (1:10)

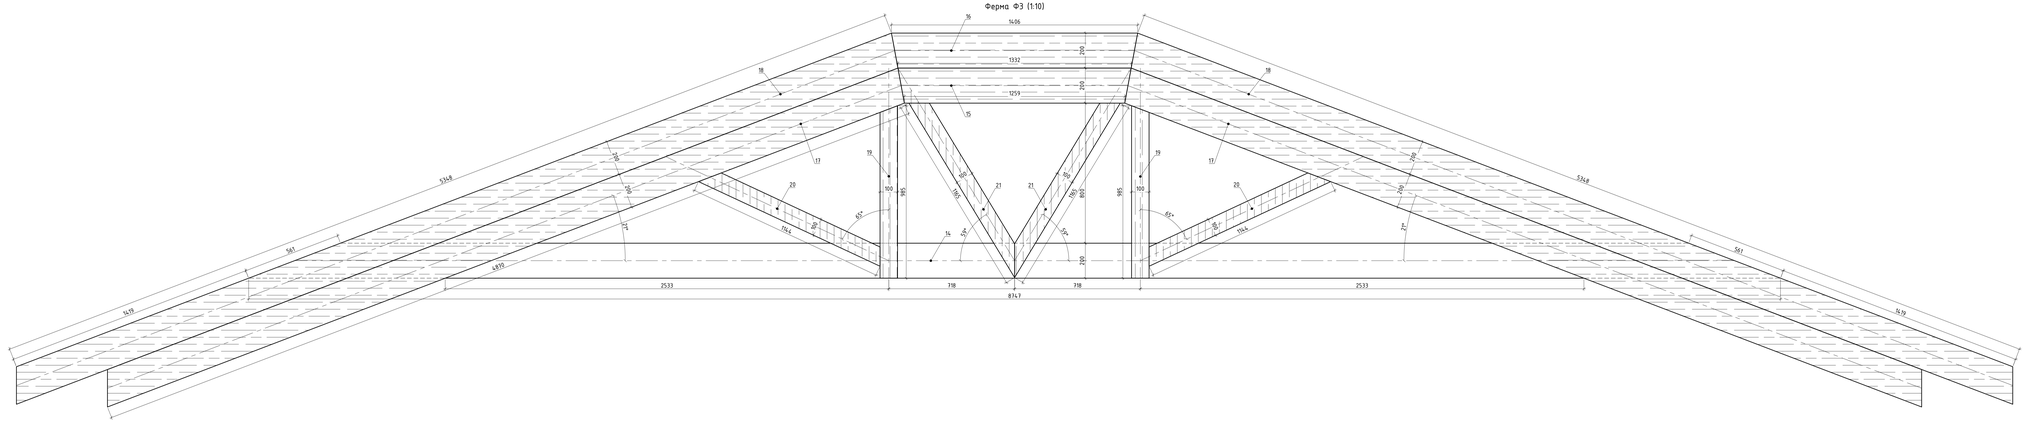

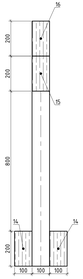


Спецификация фермы Ф3					
Поз.	Обозначение	Наименование	Кол.	Объем, м³	Итого, м³
14		Нижний пояс	2	0,17	0,35
15		Верхний пояс	1	0,03	0,03
16		Верхний пояс	1	0,03	0,03
17		Раскос	2	0,10	0,19
18		Раскос	2	0,11	0,21
19		Стойка	4	0,01	0,04
20		Раскос	2	0,01	0,02
21		Раскос	1	0,01	0,01


								М16-КД	
Изм.	Кол. уч.	Лист	№ док.	Подп.	Дата				
ГИП									
Разраб.		Андреев					Стадия	Лист	Листов
							Р	11	
							Фермы Ф1, Ф2, Ф3		
Н. контр.									

Инв. № подл. | Подп. и дата | Взам. инв. № | Согласовано


Фрагмент 5 (1:10)

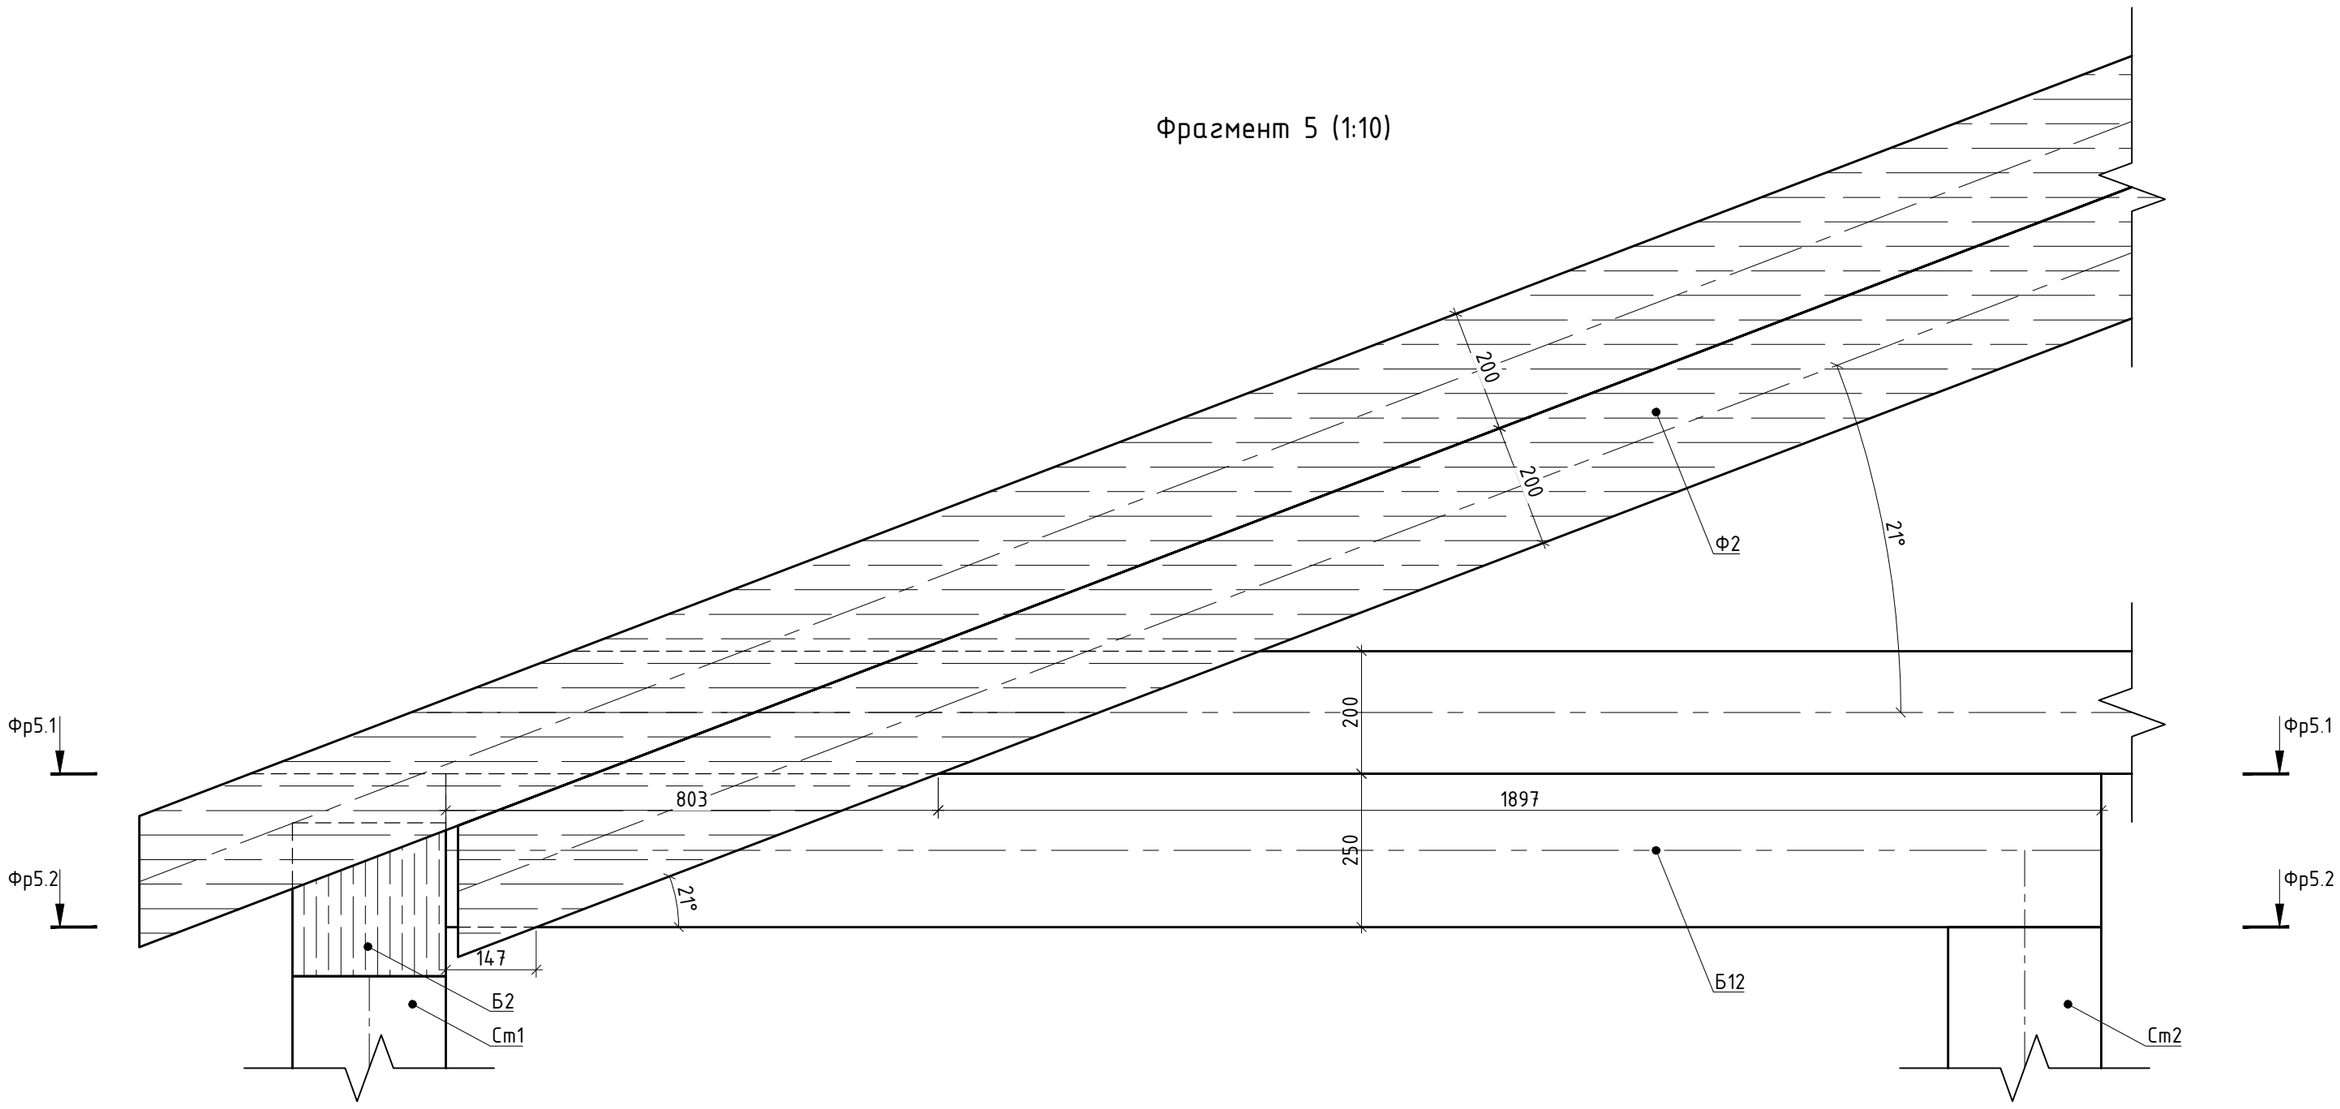

Фр5.1–Фр5.1 (1:10)

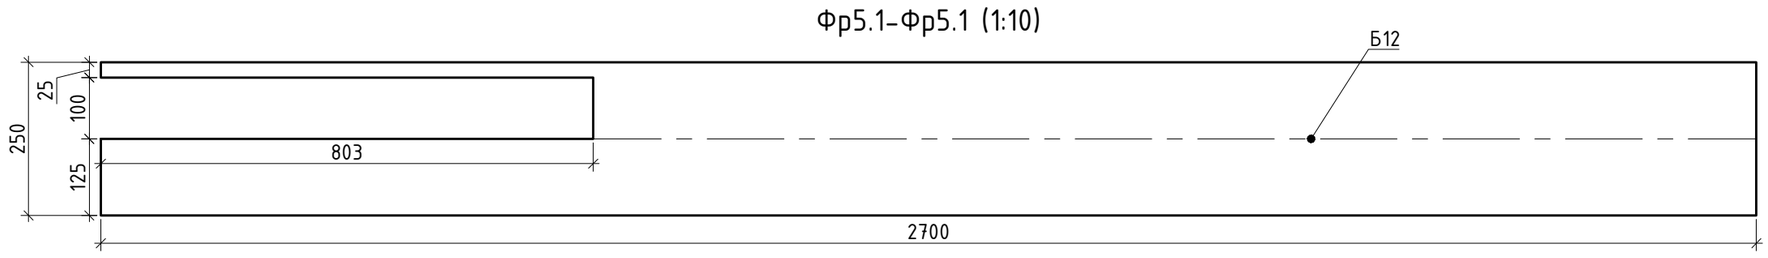

Фр5.2–Фр5.2 (1:10)

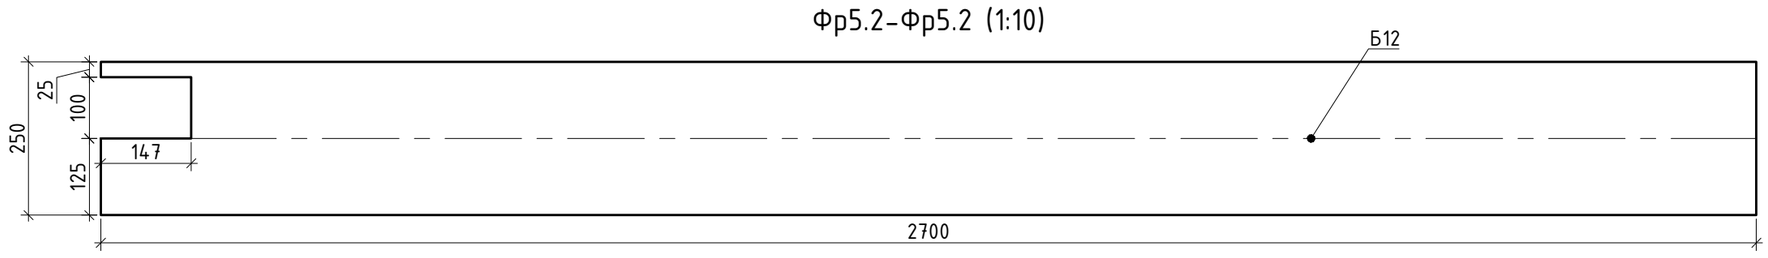

Согласовано

Взам. инв. №

Подп. и дата

Инв. № подл.

						М16-КД
		Нов.				
Изм.	Кол. уч	Лист	№ док.	Подп.	Дата	
ГИП						Стадия: Р; Лист: 12; Листов:
Разраб.		Андреев				
Н. контр.						Фрагмент 5. Балка Б12