Общество с ограниченной ответственностью «Домус»

191119, Санкт-Петербург, ул. Двинская д. 6 строение 1 кв. 37
тел: 342-45-40

Г. САНКТ-ПЕТЕРБУРГ, МИТРОФАНЬЕВСКОЕ ШОССЕ, УЧАСТОК 16, (ЗАПАДНЕЕ ДОМА 13, ЛИТЕРА Д ПО МАЛОЙ МИТРОФАНЬЕВСКОЙ УЛИЦЕ)

БЛАГОУСТРОЙСТВО ТЕРРИТОРИИ

ПРОЕКТНАЯ ДОКУМЕНТАЦИЯ

Раздел 4. Конструктивные решения

ШИФР М16-КР

Том 4

2026

Общество с ограниченной ответственностью «Домус»

191119, Санкт-Петербург, ул. Двинская д. 6 строение 1 кв. 37
тел: 342-45-40

Г. САНКТ-ПЕТЕРБУРГ, МИТРОФАНЬЕВСКОЕ ШОССЕ, УЧАСТОК 16, (ЗАПАДНЕЕ ДОМА 13, ЛИТЕРА Д ПО МАЛОЙ МИТРОФАНЬЕВСКОЙ УЛИЦЕ)

БЛАГОУСТРОЙСТВО ТЕРРИТОРИИ

ПРОЕКТНАЯ ДОКУМЕНТАЦИЯ

Раздел 4. Конструктивные решения

ШИФР М16-КР

Том 4

Генеральный директор **А. С. Бузин**

ГИП **М. В. Бузина**

2026

Содержание тома.

Обозначение	Наименование	страница
М16-КР	Содержание тома.	
	Текстовая часть:	
	а) сведения о топографических, инженерно-геологических, гидрогеологических, метеорологических и климатических условиях земельного участка, предоставленного для размещения объекта капитального строительства;	
	б) сведения об особых природных климатических условиях территории, на которой располагается земельный участок, предоставленный для размещения объекта капитального строительства;	
	в) сведения о прочностных и деформационных характеристиках грунта в основании объекта капитального строительства;	
	г) уровень грунтовых вод, их химический состав, агрессивность грунтовых вод и грунта по отношению к материалам, используемым при строительстве подземной части объекта капитального строительства;	
	д) описание и обоснование конструктивных решений зданий и сооружений, включая их пространственные схемы, принятые при выполнении расчетов строительных конструкций;	
	е) описание и обоснование технических решений, обеспечивающих необходимую прочность, устойчивость, пространственную неизменяемость зданий и сооружений объекта капитального строительства в целом, а также их отдельных конструктивных элементов, узлов, деталей в процессе изготовления, перевозки, строительства и эксплуатации объекта капитального строительства;	
	ж) описание конструктивных и технических решений подземной части объекта капитального строительства;	
	з) описание и обоснование принятых объемно-планировочных решений зданий и сооружений объекта капитального строительства;	
	и) обоснование номенклатуры, компоновки и площадей основных производственных, экспериментальных, сборочных, ремонтных и иных цехов, а также лабораторий, складских и административно-бытовых помещений, иных помещений вспомогательного и обслуживающего назначения - для объектов производственного назначения;	

Взам. инв №

Подпись и дата

Инв.№ подл.

						М16-КР			
						г. Санкт-Петербург, Митрофаньевское шоссе, участок 16, (западнее дома 13, литера Д по Малой Митрофаньевской улице)			
Изм	Кол	Лист	№док	Подпись	Дата				
Разраб.		Вакулин			06.26	Благоустройство территории	Стадия	Лист	Листов
ГИП		Бузина М.В.			06.26		П	1	
ГАП		Вакулин					ООО "Домус" г. Санкт-Петербург		
Н.контр.		Гусева				Конструктивные и объемно-планировочные решения			

	л) обоснование проектных решений и мероприятий, обеспечивающих: соблюдение требуемых теплозащитных характеристик ограждающих конструкций; снижение шума и вибраций; гидроизоляцию и пароизоляцию помещений; снижение загазованности помещений; удаление избытков тепла; соблюдение безопасного уровня электромагнитных и иных излучений, соблюдение санитарно-гигиенических условий; пожарную безопасность;	
	м) характеристику и обоснование конструкций полов, кровли, подвесных потолков, перегородок, а также отделки помещений;	
	н) перечень мероприятий по защите строительных конструкций и фундаментов от разрушения;	
	о) описание инженерных решений и сооружений, обеспечивающих защиту территории объекта капитального строительства, отдельных зданий и сооружений объекта капитального строительства, а также персонала (жителей) от опасных природных и техногенных процессов; в графической части	
М16-КР	Графическая часть.	
Лист 2	Часовня. План на отм.0,000 в осях 1-1/А-Г. М 1:100	
Лист 3	Часовня. План кровли в осях 1-15/А-Г. М 1:100	
Лист 4	Часовня. Разрез 1-1, Разрез 2-2. М 1:100	
Лист 5	Бытовое здание. План на отм.0,000 в осях 1-1/А-Г. М 1:100	
Лист 6	Бытовое здание. Разрез 3-3, Разрез 4-4. М 1:100	
Лист 7	Часовня. Схема расположения плит П1 на отм. -0,210 (отн.). Разрез 1-1. М1:50	
Лист 8	Бытовое здание. Схема расположения плит П1 на отм. -0,210 (отн.). Разрез 2-2. М1:50	
Лист 9	Часовня. Схема расположения стоек на отм. -0,030 (отн.). М1:50	
Лист 10	Бытовое здание. Схема расположения стоек на отм. -0,030 (отн.). М1:50	

Взам. инв №

Подпись и дата

Инв.№ подл.

Изм	Кол	Лист	№док	Подпись	Дата	М16-КР	Лист 2

а)сведения о топографических, инженерно-геологических, гидрогеологических, метеорологических и климатических условиях земельного участка, предоставленного для размещения объекта капитального строительства;

Зона строительства относится к климатическому району II, подрайону II-В по СНиП 23-01-99* «Строительная климатология». Климат района характеризуется умеренно тёплым летом и длительной умеренно холодной зимой с оттепелями. Среднегодовая температура воздуха 3,3°С. Наиболее холодный месяц – январь со средней температурой -8,7°С, абсолютный минимум -49°С.

Наиболее тёплый месяц – июль со средней температурой 16,7°С, абсолютный максимум 33°С.Продолжительность периода отрицательных температур – 149 суток. Преобладающее направление ветра в году – юго-западное, среднегодовая скорость ветра 4,6м/сек, максимальная, повторяющаяся 1 раз в 20 лет – 27 м/сек. Рассматриваемая территория характеризуется умеренным избыточно влажным климатом с неустойчивым режимом погоды, которая относится ко $II^{в}$ подрайону по климатическому районированию России для строительства. По количеству атмосферных осадков район относится к зоне избыточного увлажнения. Среднегодовое количество осадков составляет 734 мм, из них 62 % приходится на тёплый период года. Устойчивый снежный покров сохраняется с 04.12 по 10.02, расчётная толщина снежного покрова – 0,55 м.

Часовня и бытовое здание расположены по адресу г. Санкт-Петербург, Митрофаньевское шоссе, участок 16 (западнее дома 13, литера Д по Малой Митрофаньевской улице).

Непосредственно под пятном застройки зданий инженерные сети отсутствуют.

Почвенно-растительный слой (0,1-0,4м). Нижележащий слой представлен суглинками легкими пылеватыми, твердыми, с гравием и галькой до 10%, коричневыми и коричневато-зелеными, с редкими линзами супесей, с гнездами и линзами песков, насыщенных водой.

б) сведения об особых природных климатических условиях территории, на которой располагается земельный участок, предоставленный для размещения объекта капитального строительства;

Особые природные климатические условия территории, на которой располагается земельный участок, предоставленный для размещения часовни и бытового здания, отсутствуют.

в) сведения о прочностных и деформационных характеристиках грунта в основании объекта капитального строительства;

В качестве основания незаглублённых фундаментов из плит ПАГ-18 приняты:

Суглинки легкие пылеватые, твердые, с гравием и галькой до 10%, коричневые и коричневато-зеленые, с редкими линзами супесей, с гнездами и линзами песков, насыщенных водой.

г) уровень грунтовых вод, их химический состав, агрессивность грунтовых вод и грунта по отношению к материалам, используемым при строительстве подземной части объекта капитального строительства;

На площадке встречены подземные воды типа «верховодка». На отдельных участках площадки наблюдается переувлажнение поверхности. В сухое время года отсутствуют воды типа «верховодка».

Линзы и гнезда песка в слабофильтрующих ледниковых суглинках могут содержать подземные воды спорадического распространения, появление которых возможно в любое время года на любой глубине.

д) описание и обоснование конструктивных решений зданий и сооружений, включая их пространственные схемы, принятые при выполнении расчетов строительных конструкций;

Часовня запроектирована 1-о этажной, с высотой в коньке 6,26м, с высотой креста 11,01м от уровня дневной поверхности.

В плане часовня представляет собой однонефную базилику с размерами в осях 11,0х17,1м. Стойки деревянные, сечением 200х200мм. Стропильная система деревянная, сечением 200х100мм. Потолочные балки деревянные, сечением 200х100мм.

Конструктивная схема каркаса часовни - это здание с полным каркасом из деревянных стоек и деревянных стропил. По статической схеме – 2-х шарнирная рама. Распор стропильной системы воспринимается затяжками.

Пространственную неизменяемость обеспечивает установка вертикальных связей в продольном и поперечном направлении.

Фундаменты часовни из плит ПАГ-18 (2х6м) мелкого заложения, с отм. заложения -0,210(отн.) - +4,030(абс.).

Бытовое здание запроектировано 1-о этажным, с высотой в коньке 6,32м.

В плане бытовое здание представляет собой прямоугольник с размерами в осях 13,2х14,4м. Стойки деревянные, сечением 200х200мм. Стропильная система деревянная, сечением 200х100мм. Потолочные балки деревянные, сечением 200х100мм.

Конструктивная схема каркаса бытового здания - это здание с полным каркасом из деревянных стоек и деревянных стропил. По статической схеме – 2-х шарнирная рама. Распор стропильной системы воспринимается затяжками.

Пространственную неизменяемость обеспечивает установка вертикальных связей в продольном и поперечном направлении.

Фундаменты бытового здания из плит ПАГ-18 (2х6м) мелкого заложения, с отм. заложения - 0,210(отн.) - +3,67(абс.).

е) описание и обоснование технических решений, обеспечивающих необходимую прочность, устойчивость, пространственную неизменяемость зданий и сооружений объекта капитального строительства в целом, а также их отдельных конструктивных элементов, узлов, деталей в процессе изготовления, перевозки, строительства и эксплуатации объекта капитального строительства;

В процессе монтажа здания на строительной площадке производится укрупнительная сборка элементов заводского изготовления с последующей установкой в проектное положение. Для монтажа конструкций должен быть составлен проект производства работ. Для обеспечения высокого качества монтажных соединений на заводе произвести общую или контрольную сборку изготовленных элементов. В процессе общей сборки проверить точность изготовления отправочных элементов произвести подгонку кромок для монтажных сварных соединений, рассверловку монтажных отверстий под болты на проектный диаметр.

Деревянные стойки устанавливаются в вертикальное положение при помощи усиленных монтажных уголков. Следующим этапом устанавливаются вертикальные связи в продольном и поперечном направлениях.

Подъем в проектное положение стропильных ферм осуществляется с помощью траверсы для предотвращения потери устойчивости затяжек.

В процессе эксплуатации здания не допускается превышение расчетных нагрузок на перекрытие и покрытия. Установление наблюдения за осадками здания технической службой. Периодический осмотр конструкций для выявления нарушения целостности защитных окрасочных слоев.

ж) описание конструктивных и технических решений подземной части объекта капитального строительства;

Фундаменты часовни из плит ПАГ-18 (2х6м) мелкого заложения, с отм. заложения -0,210(отн.) - +4,030(абс.).

Фундаменты бытового здания из плит ПАГ-18 (2х6м) мелкого заложения, с отм. заложения -0,210(отн.) - +3,67(абс.).

Растительный слой мощностью от 100 до 200мм заменяется на песок средней крупности с трамбованием.

Несущим слоем для фундаментов приняты суглинки легкие пылеватые, твердые, с гравием и галькой до 10%, коричневые и коричневато-зеленые, с редкими линзами супесей, с гнездами и линзами песков, насыщенных водой.

з) описание и обоснование принятых объемно-планировочных решений зданий и сооружений объекта капитального строительства;

Принятые объемно-пространственные и архитектурно-художественные решения обусловлены следующим:

1. Стилевое решение объектов выполнено в традициях русской храмовой архитектуры, что обусловлено функциональным назначением временного храма и необходимостью гармоничного включения объектов в исторический контекст территории церкви Митрофания Воронежского (XIX в.).

2. Объемно-пространственная композиция временного храма:
   - прямоугольная в плане форма с размерами 8 300 × 5 000 мм;
   - высота здания до конька кровли — 9 800 мм;
   - наличие шатрового завершения, характерного для культовых сооружений;
   - организация входной группы с юго-восточной стороны.

3. Объемно-пространственная композиция Бытового здания:
   - прямоугольная в плане форма с размерами 5 000 × 4 400 мм;
   - скатная кровля;
   - функциональное зонирование внутреннего пространства.

4. Соблюдение предельных параметров — проектные решения приняты с учетом требований к временным нестационарным сооружениям, установленных договором аренды и Правилами благоустройства территории Санкт-Петербурга.

з1) Обоснование принятых архитектурных решений в части обеспечения соответствия зданий требованиям энергетической эффективности

В соответствии с требованиями энергетической эффективности (Федеральный закон от 23.11.2009 № 261-ФЗ «Об энергосбережении и о повышении энергетической эффективности») проектируемые объекты относятся к категории временных нестационарных сооружений, не

предназначенных для круглогодичного использования с постоянным пребыванием людей. Требования энергетической эффективности к указанным объектам не предъявляются.

з2) Перечень мероприятий по обеспечению соблюдения установленных требований энергетической эффективности

Ввиду того, что требования энергетической эффективности на проектируемые объекты не распространяются, перечень мероприятий не разрабатывается.

з3) Описание и обоснование принятых архитектурных решений, направленных на повышение энергетической эффективности

Проектируемые объекты не имеют систем инженерно-технического обеспечения, не требуют подключения к сетям тепло- и электроснабжения. Мероприятия по повышению энергетической эффективности не предусматриваются.

и) обоснование номенклатуры, компоновки и площадей основных производственных, экспериментальных, сборочных, ремонтных и иных цехов, а также лабораторий, складских и административно-бытовых помещений, иных помещений вспомогательного и обслуживающего назначения - для объектов производственного назначения;

Номенклатура зданий и помещений принята в составе часовни и бытового здания.

Часовня запроектирована одноэтажной, с высотой в коньке 6,26 м и высотой креста 11,01 м от уровня дневной поверхности. В плане часовня представляет собой однонефную базилику с размерами в осях 11,0 × 17,1 м. Площадь часовни составляет 132,6 м^2.

Компоновка часовни принята с учетом ее функционального назначения и объемно-планировочной схемы однонефной базилики. Конструктивная схема здания – полный деревянный каркас из деревянных стоек и деревянных стропил.

Бытовое здание запроектировано одноэтажным, с высотой в коньке 6,32 м. В плане бытовое здание представляет собой прямоугольник с размерами в осях 13,2 × 14,4 м. Площадь бытового здания в габаритах осей составляет 141,0 м^2.

Компоновка бытового здания принята в виде прямоугольного одноэтажного объема с деревянным каркасом. Конструктивная схема здания – полный каркас из деревянных стоек и деревянных стропил.

Принятые площади зданий определены их габаритами в осях и соответствуют объемно-планировочным решениям, предусмотренным проектной документацией.


л) обоснование проектных решений и мероприятий, обеспечивающих:
соблюдение требуемых теплозащитных характеристик ограждающих конструкций;

Наружные стены толщиной 300мм. С наружной стороны оштукатуривание по плитам ЦСП с окраской фасадными красками. С внутренней стороны оштукатуривание по плитам ГКЛ с окраской интерьерными красками. Внутренняя часть стены заполняется базальтовой негорючей ватой объемным весом 45кг/м^3 с установкой по внутренней поверхности пароизоляции.

Утепление кровли – минераловатные плиты объемным весом 15кг/м^3 толщиной 200мм. С наружной стороны устанавливается ветроизоляция, продух 25мм и сплошная обрешетка для раскладки гидроизоляции. С внутренней стороны устанавливается пароизоляция, обшивка из плит ГКЛ с окраской интерьерными красками.

ГРАФИЧЕСКАЯ ЧАСТЬ

1. План на отм. 0,000 1:100

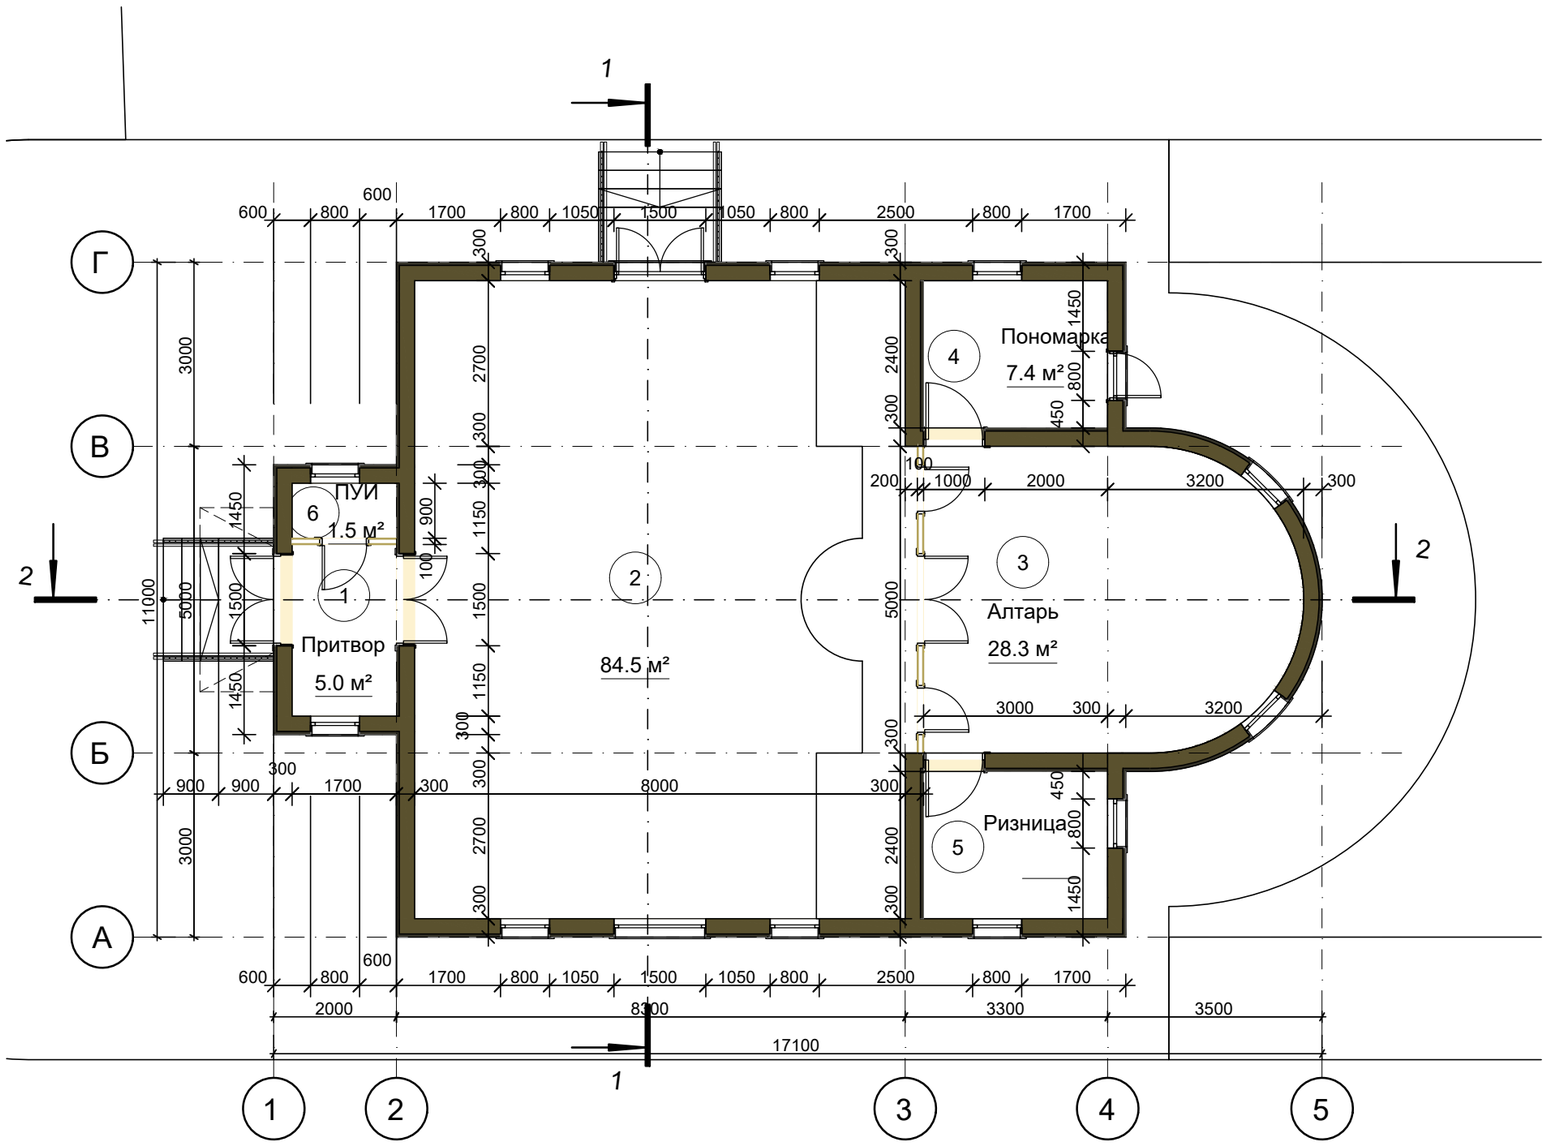

Согласовано:


Взам. инв. №

Подп. и дата

Инв. № подл.

						M16-КР	
						г.Санкт-Петербург, Митрофаньевское шоссе, участок 16, (западнее дома 13, литера Д по Малой Митрофаньевской улице)	
Изм.	Кол.уч.	Лист	№док	Подпись	Дата		
Разработал		Вакулин			06.26	Благоустройство территории	Стадия: П; Лист: 2; Листов:
Проверил		Бузина			06.26		
Н.контр		Гусева			06.26	Часовня. План на отм. 0,000	ООО "Домус" г. Санкт-Петербург
ГИП		Бузина			06.26		

3. Кровля 1:100

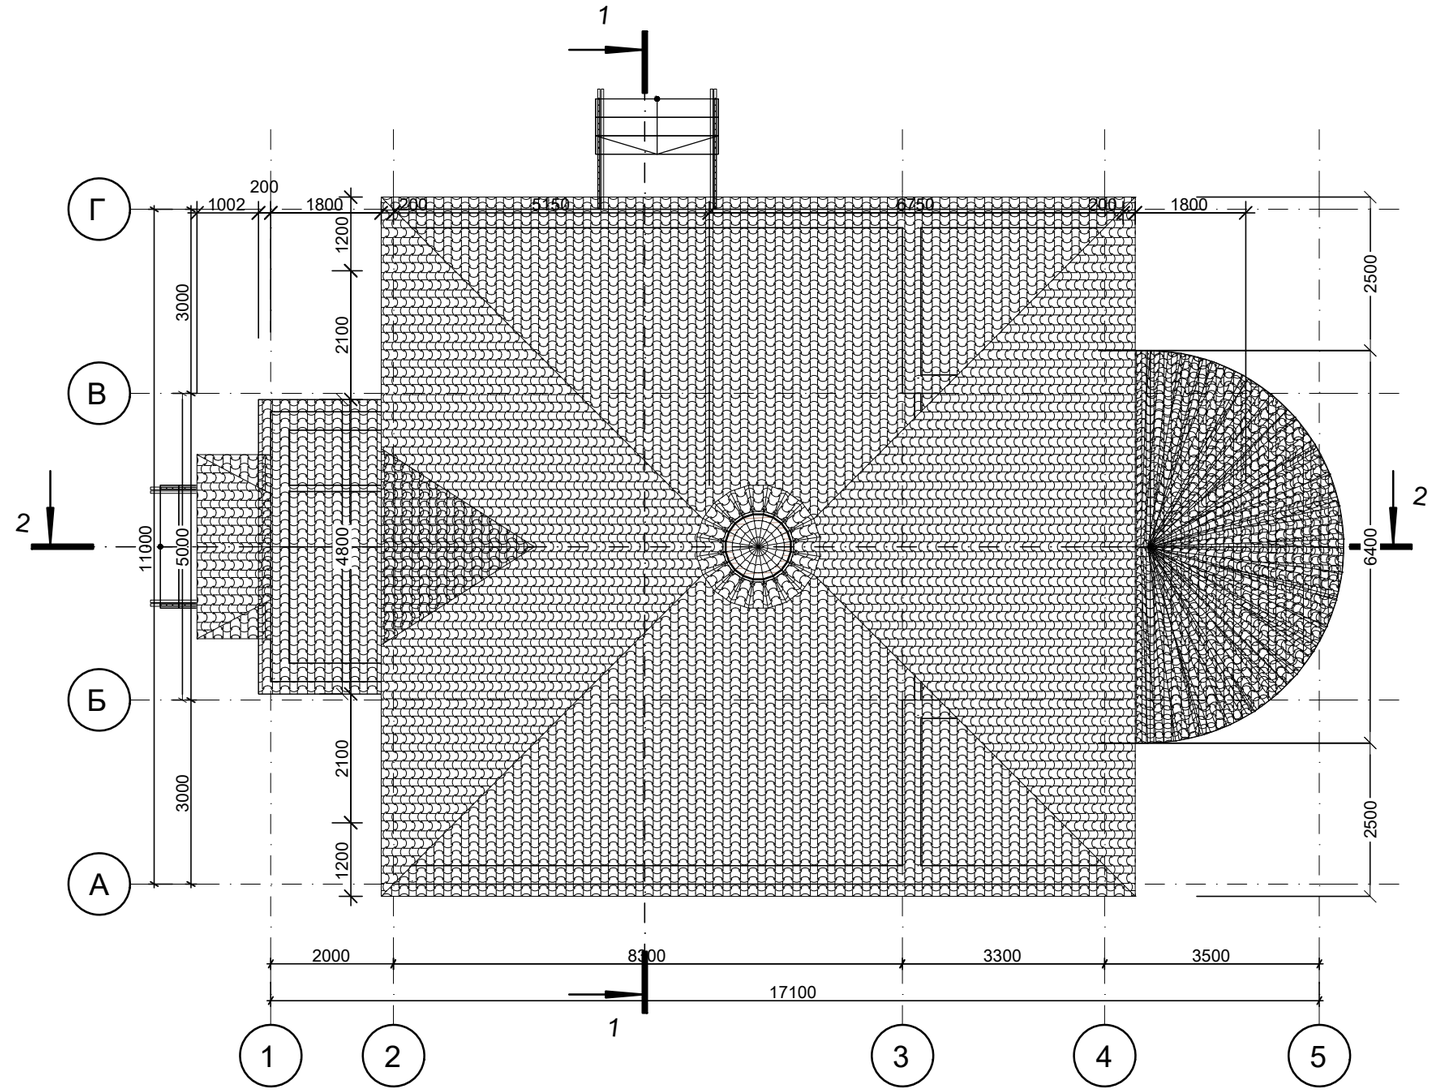

Согласовано:


Взам. инв. №

Подп. и дата


Инв. № подл.

						М16-КР	
						г.Санкт-Петербург, Митрофаньевское шоссе, участок 16, (западнее дома 13, литера Д по Малой Митрофаньевской улице)	
Изм.	Кол.уч.	Лист	№док	Подпись	Дата		
Разработал		Вакулин			06.26	Благоустройство территории	Стадия: П; Лист: 3; Листов:
Проверил		Бузина			06.26		
Н.контр		Гусева			06.26	Часовня. План кровли	ООО "Домус" г. Санкт-Петербург
ГИП		Бузина			06.26		

1 Разрез 1-1 1:100

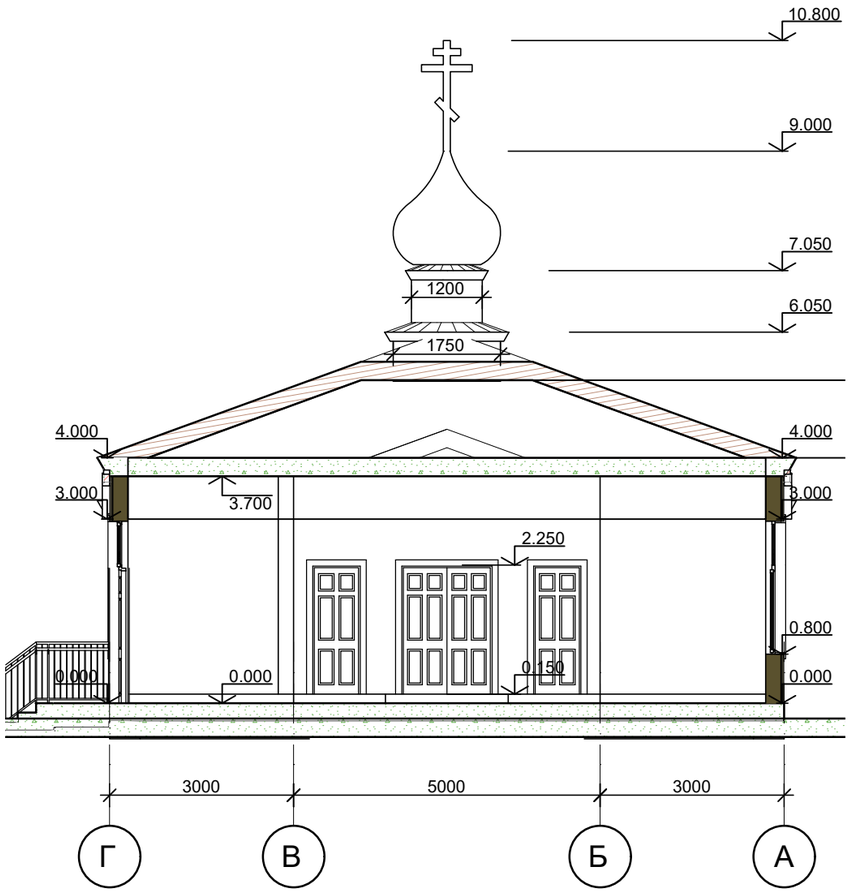

2 Разрез 2-2 1:100

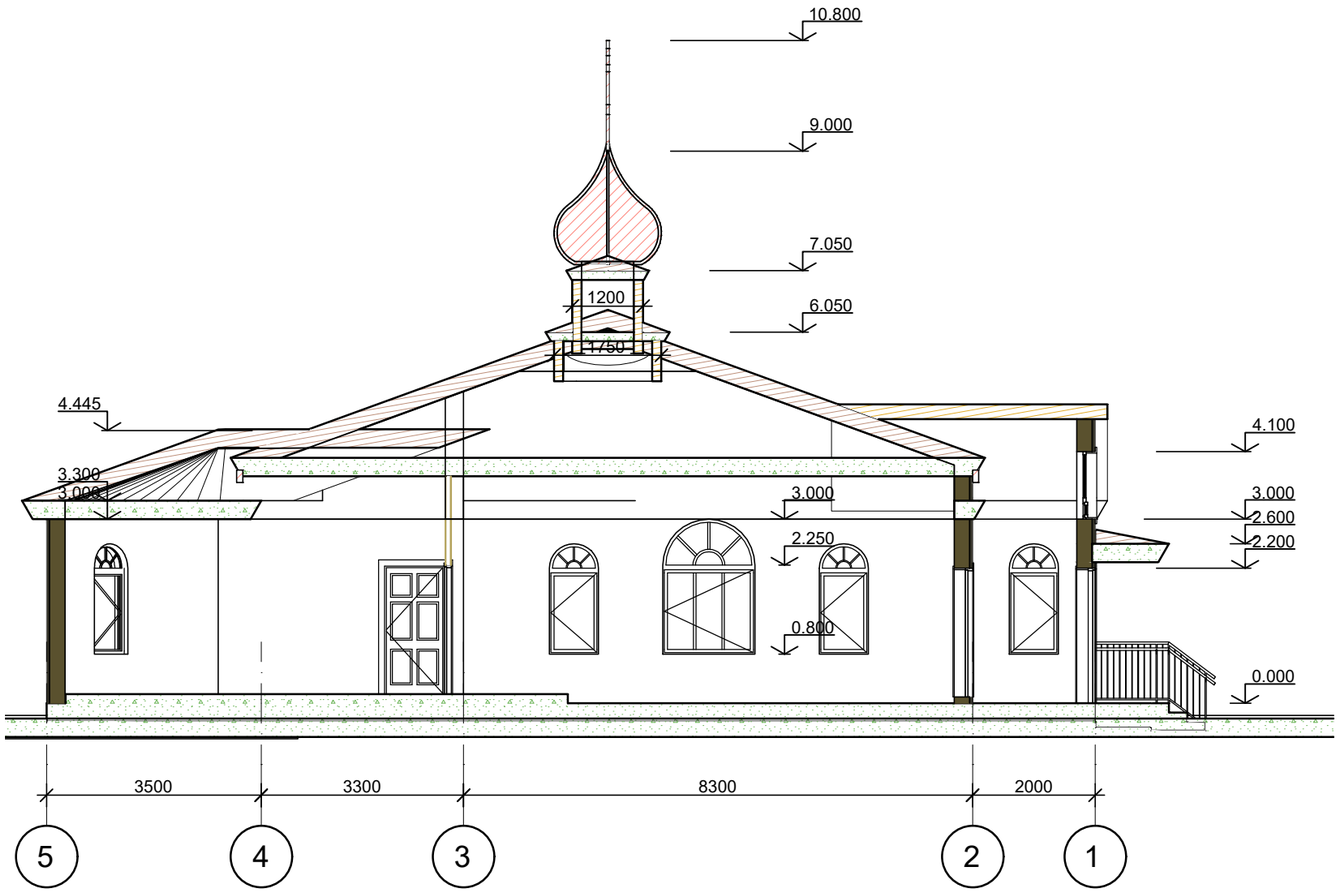

Согласовано:


Взам. инв. №

Подп. и дата

Инв. № подл.

						М16-КР	
						г.Санкт-Петербург, Митрофаньевское шоссе, участок 16, (западнее дома 13, литера Д по Малой Митрофаньевской улице)	
Изм.	Кол.уч.	Лист	№док	Подпись	Дата		
Разработал		Вакулин			06.26	Благоустройство территории	Стадия: П; Лист: 4; Листов:
Проверил		Бузина			06.26		
Н.контр		Гусева			06.26	Часовня. Разрез 1-1. Разрез 2-2	ООО "Домус" г. Санкт-Петербург
ГИП		Бузина			06.26		

1. План на отм. 0,000. 1:100

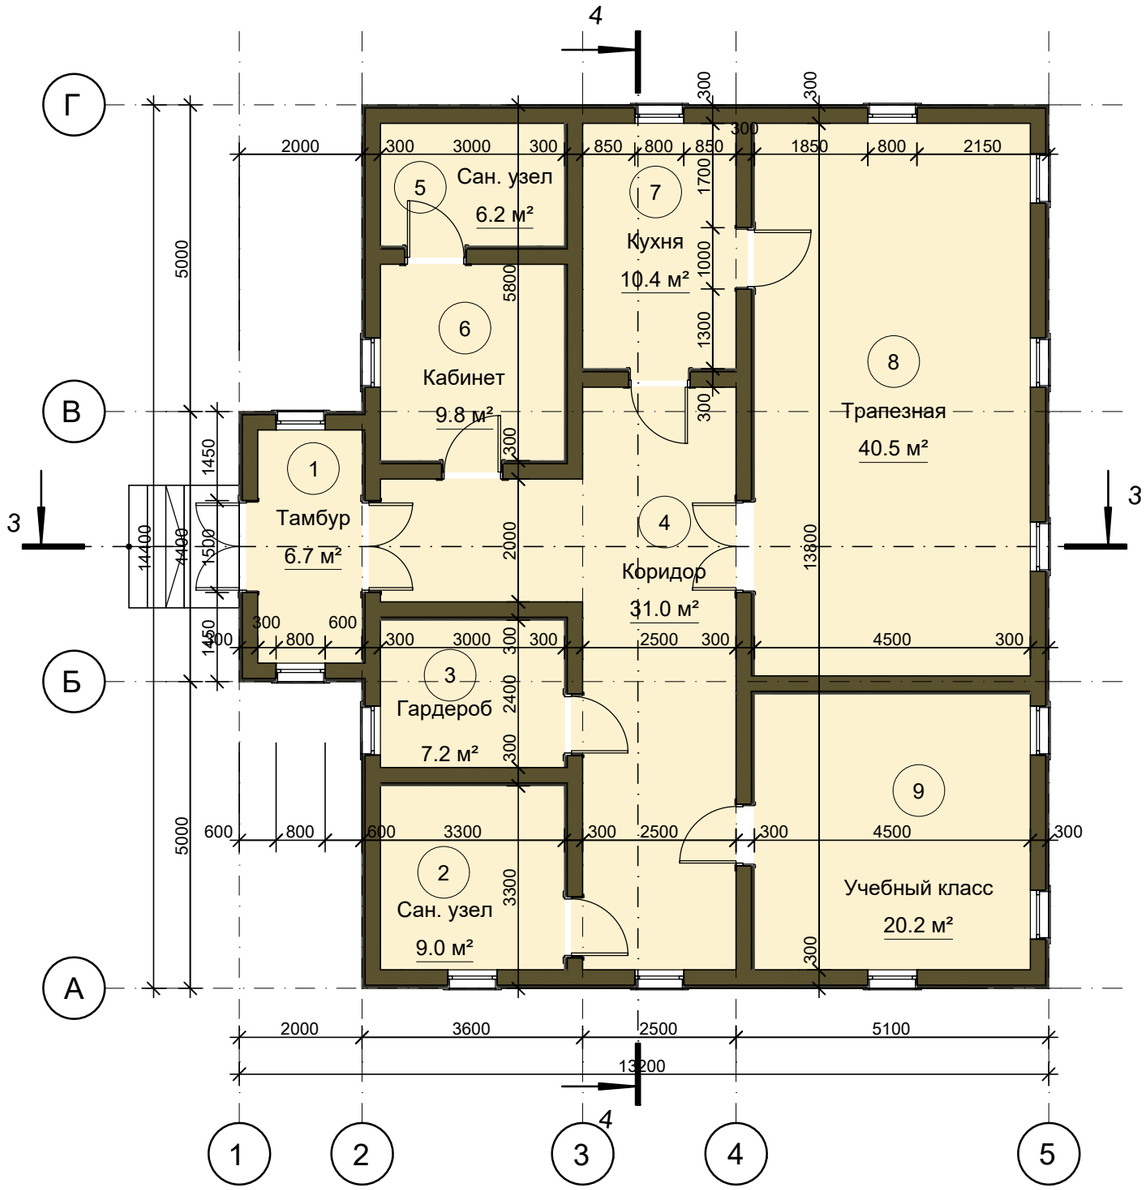

Изм.	Кол.уч.	Лист	№док	Подпись	Дата
Разработал		Вакулин			06.26
Проверил		Бузина			06.26
Н.контр		Гусева			06.26
ГИП		Бузина			06.26

М16-КР

г.Санкт-Петербург, Митрофаньевское шоссе, участок 16,
(западнее дома 13, литера Д по Малой Митрофаньевской улице)

Благоустройство территории	Стадия	Лист	Листов
	П	5	
Бытовое здание. План на отм. 0,000	ООО "Домус" г. Санкт-Петербург		


Согласовано:

Взам. инв. №


Подп. и дата

Инв. № подл.

3 Разрез 3-3 1:100

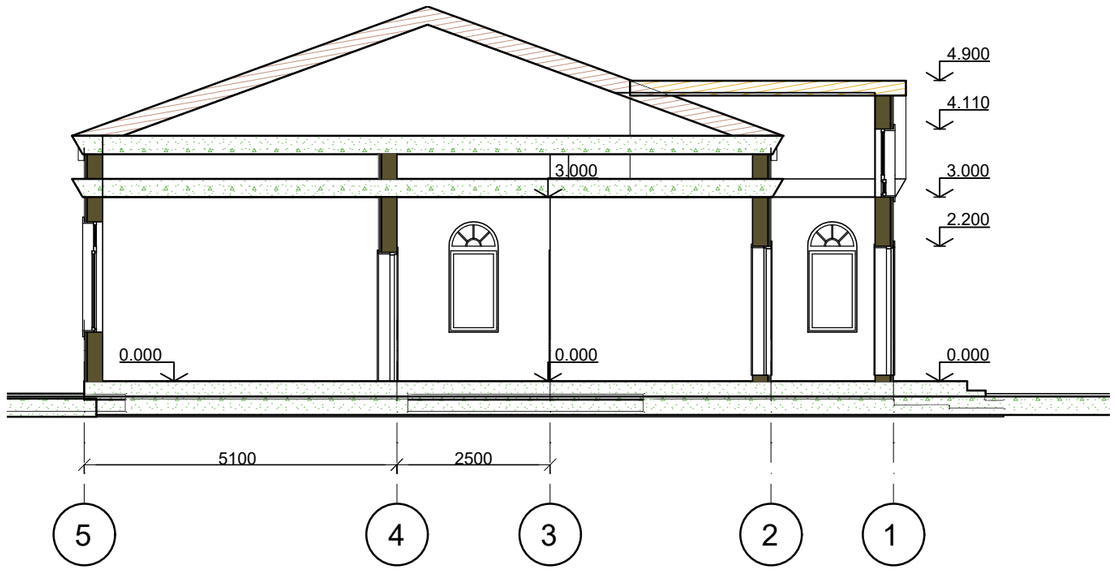

4 Разрез 4-4 1:100

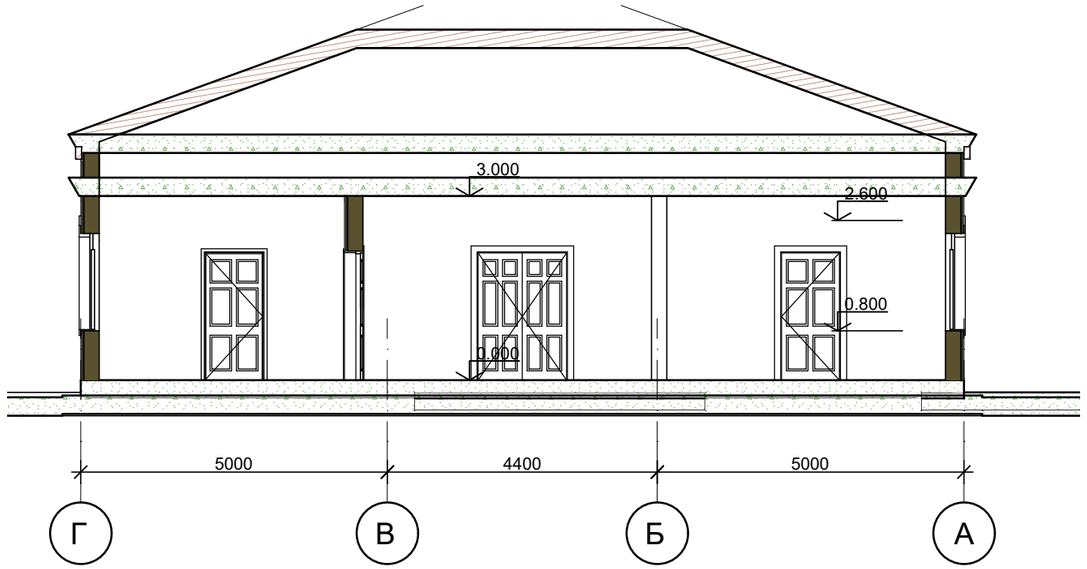

Согласовано:

Взам. инв. №

Подп. и дата

Инв. № подл.

Изм.	Кол.уч.	Лист	№док	Подпись	Дата
Разработал		Вакулин			06.26
Проверил		Бузина			06.26
Н.контр		Гусева			06.26
ГИП		Бузина			06.26

М16-КР


г.Санкт-Петербург, Митрофаньевское шоссе, участок 16,
(западнее дома 13, литера Д по Малой Митрофаньевской улице)

Благоустройство территории


Стадия	Лист	Листов
П	6	

Бытовое здание. Разрез 3-3. Разрез 4-4

ООО "Домус"
г. Санкт-Петербург

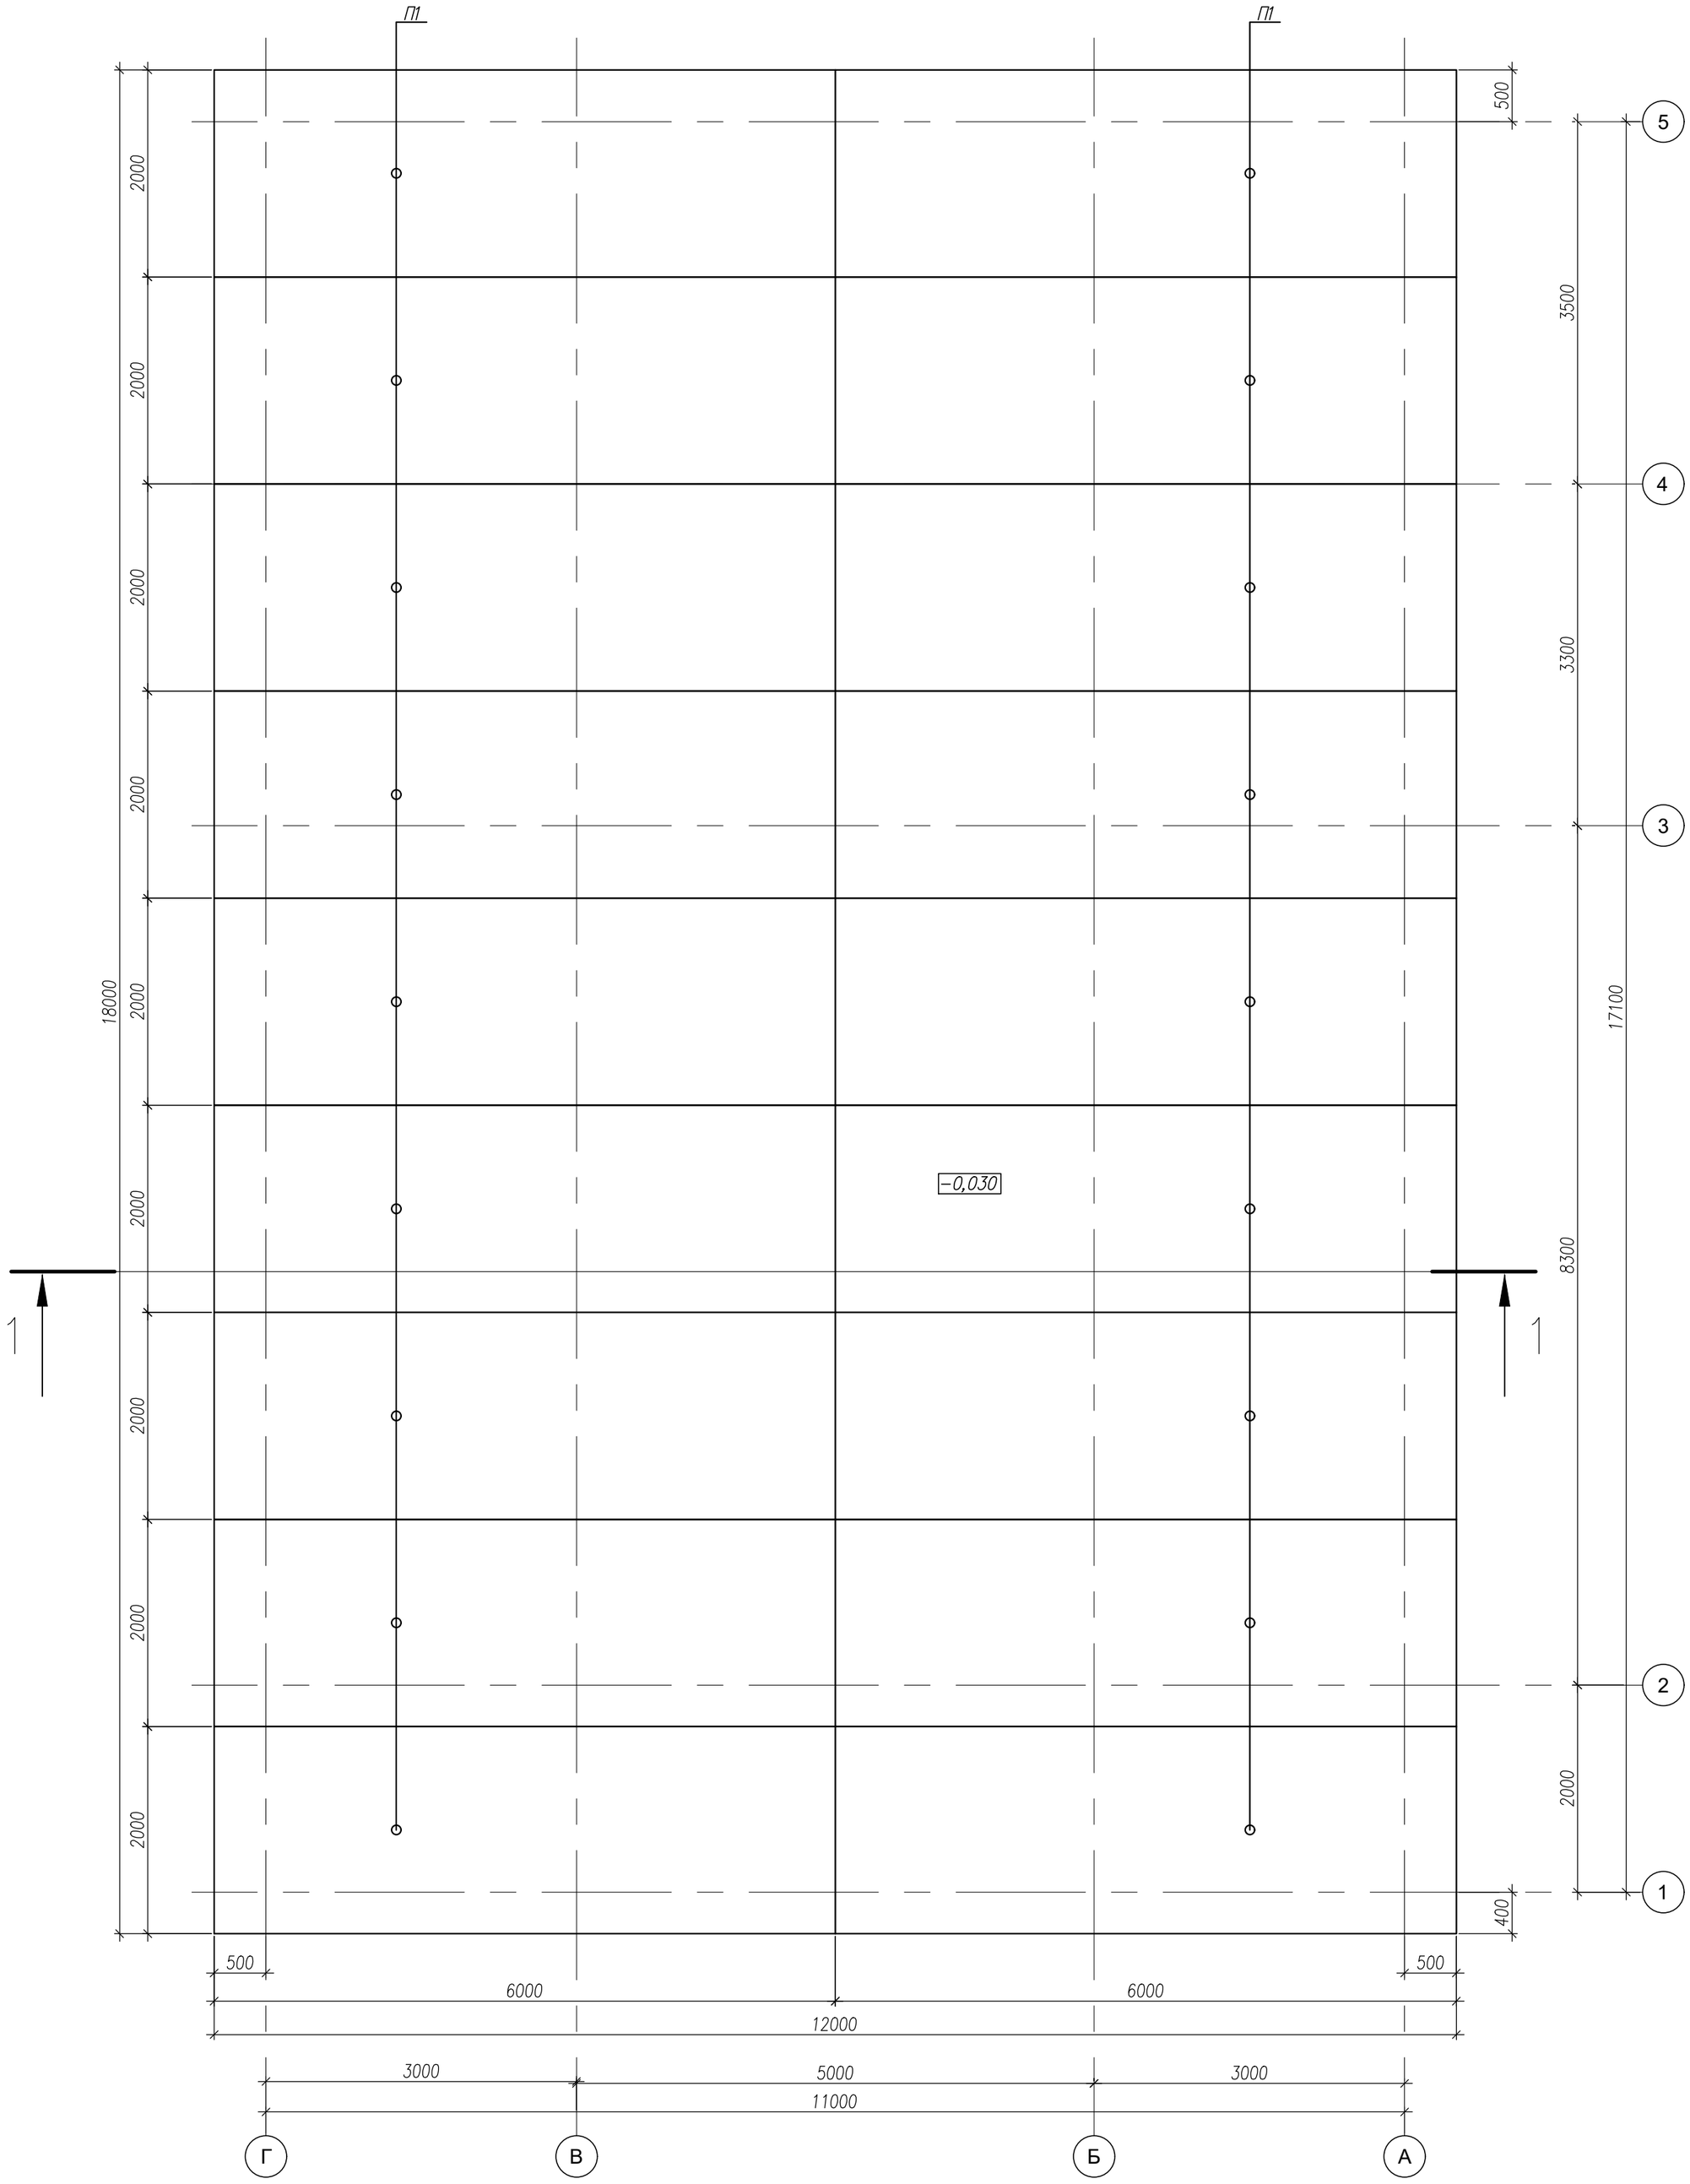

1 – 1

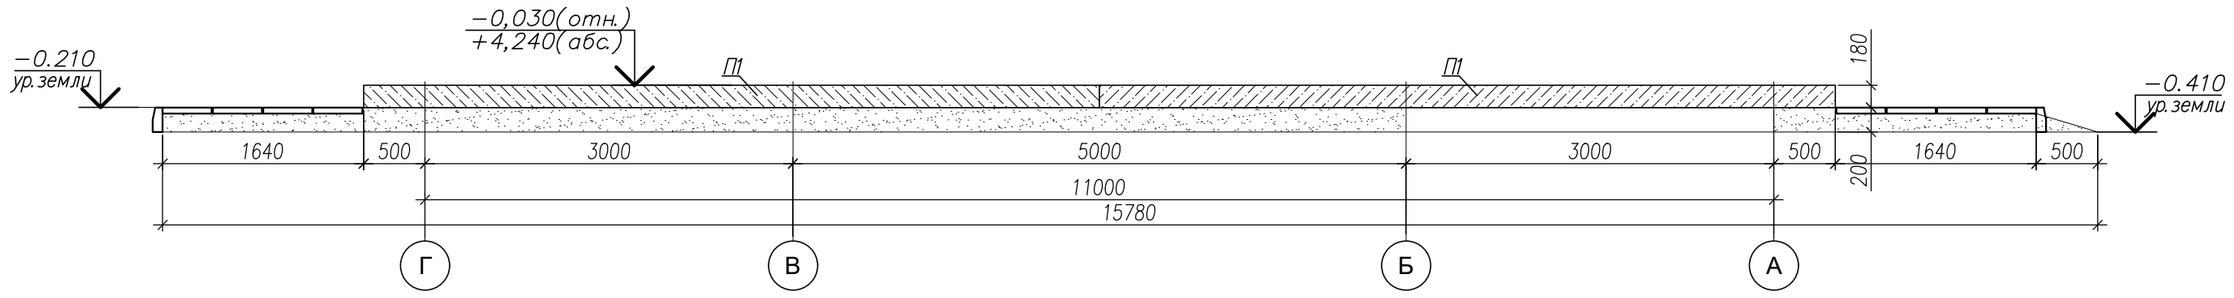

Спецификация к схеме расположения сборных плит

Поз.	Обозначение	Наименование	Кол-во	Масса ед.,кг	Приме-чание
		плиты сборные			
П1	Данный лист	ПАГ-18 ГОСТ25912-2015	18		
		Материалы			
		Песок средней крупности	58		$м^3$
		Рубероид РПП-300 ГОСТ10923-93	15		рулон

Согласовано:

Взам. инв. №

Подп. и дата

Инв. № подл.

Изм.	Кол.уч.	Лист	№док	Подпись	Дата
Разработал		Андреев			06.26
Проверил		Бузина			06.26
Н.контр		Гусева			06.26
ГИП		Бузина			06.26

М16-КР


г.Санкт-Петербург, Митрофаньевское шоссе, участок 16,
(западнее дома 13, литера Д по Малой Митрофаньевской улице)


Благоустройство территории

Стадия	Лист	Листов
П	7	

Часовня. Схема расположения плит П1.
Разрез 1-1

ООО "Домус"
г. Санкт-Петербург

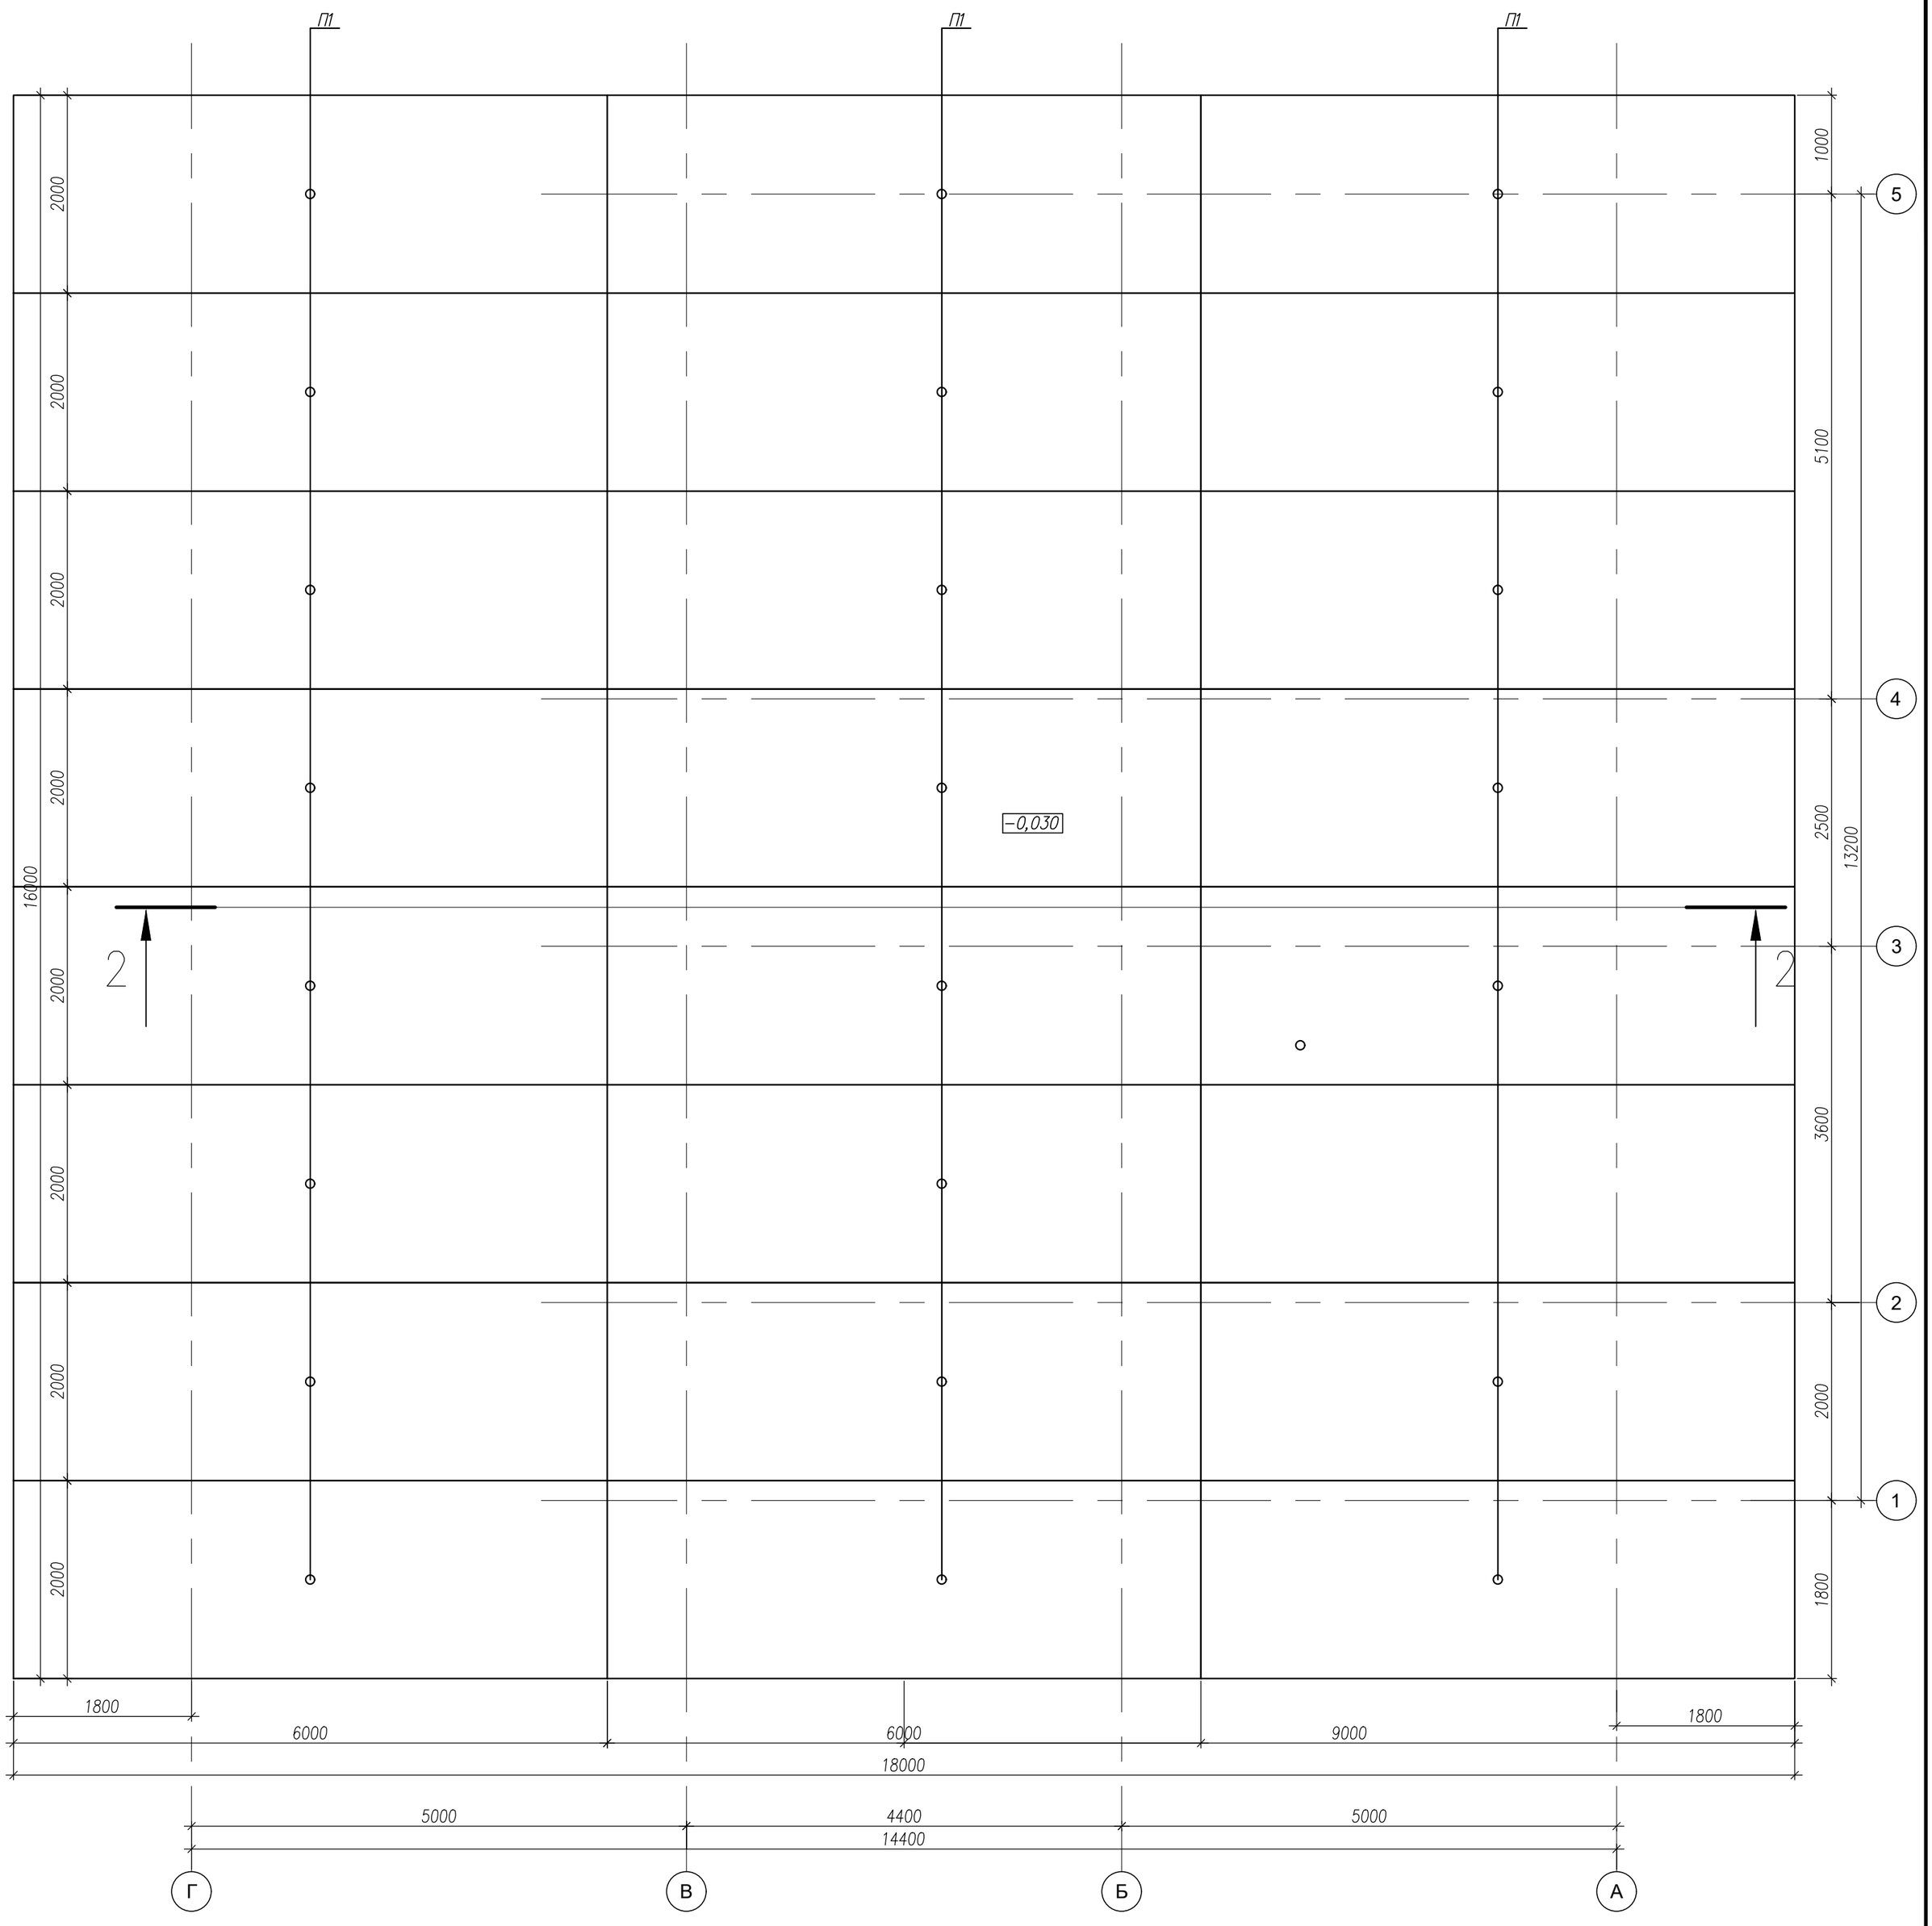

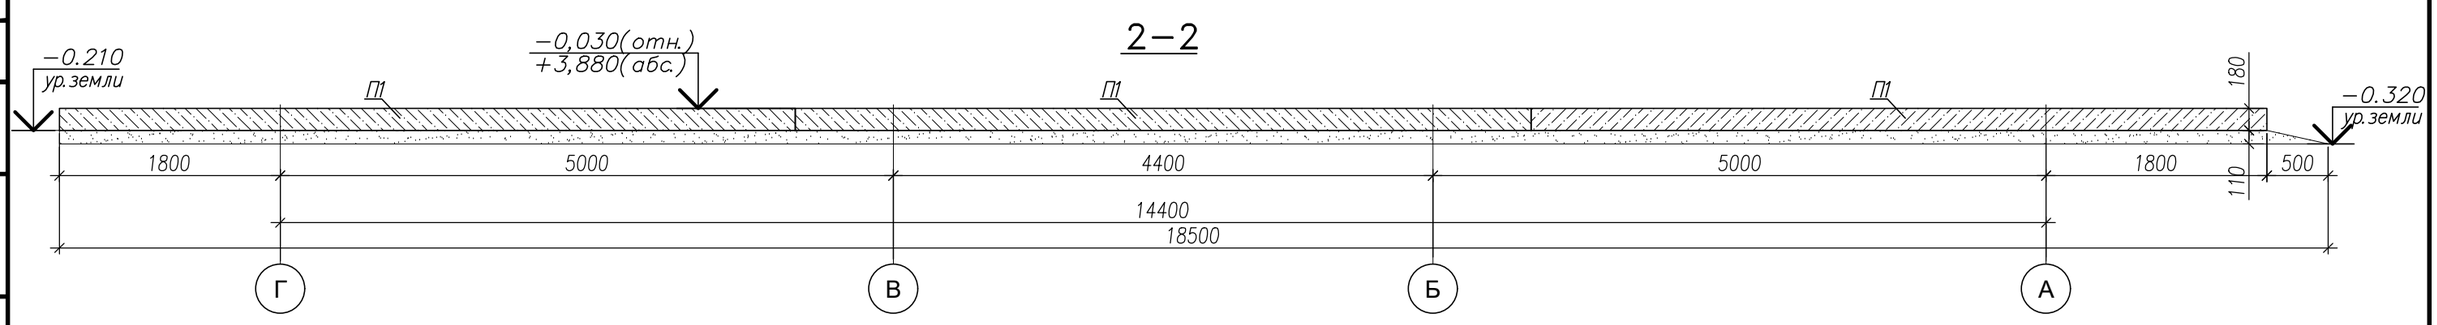

Спецификация к схеме расположения сборных плит

Поз.	Обозначение	Наименование	Кол-во	Масса ед.,кг	Приме-чание
		плиты сборные			
П1	Данный лист	ПАГ-18 ГОСТ25912-2015	24		
		Материалы			
		Песок средней крупности	33		$м^3$
		Рубероид РПП-300 ГОСТ10923-93	20		рулон

Согласовано:

Взам. инв. №

Подп. и дата

Инв. № подл.

Изм.	Кол.уч.	Лист	№док	Подпись	Дата
Разработал		Андреев			06.26
Проверил		Бузина			06.26
Н.контр		Гусева			06.26
ГИП		Бузина			06.26

М16-КР

г.Санкт-Петербург, Митрофаньевское шоссе, участок 16,
(западнее дома 13, литера Д по Малой Митрофаньевской улице)


Благоустройство территории

Стадия	Лист	Листов
П	8	

Бытовое здание.
Схема расположения плит П1. Разрез 2-2

ООО "Домус"
г. Санкт-Петербург

Схема расположения стоек (1:30)

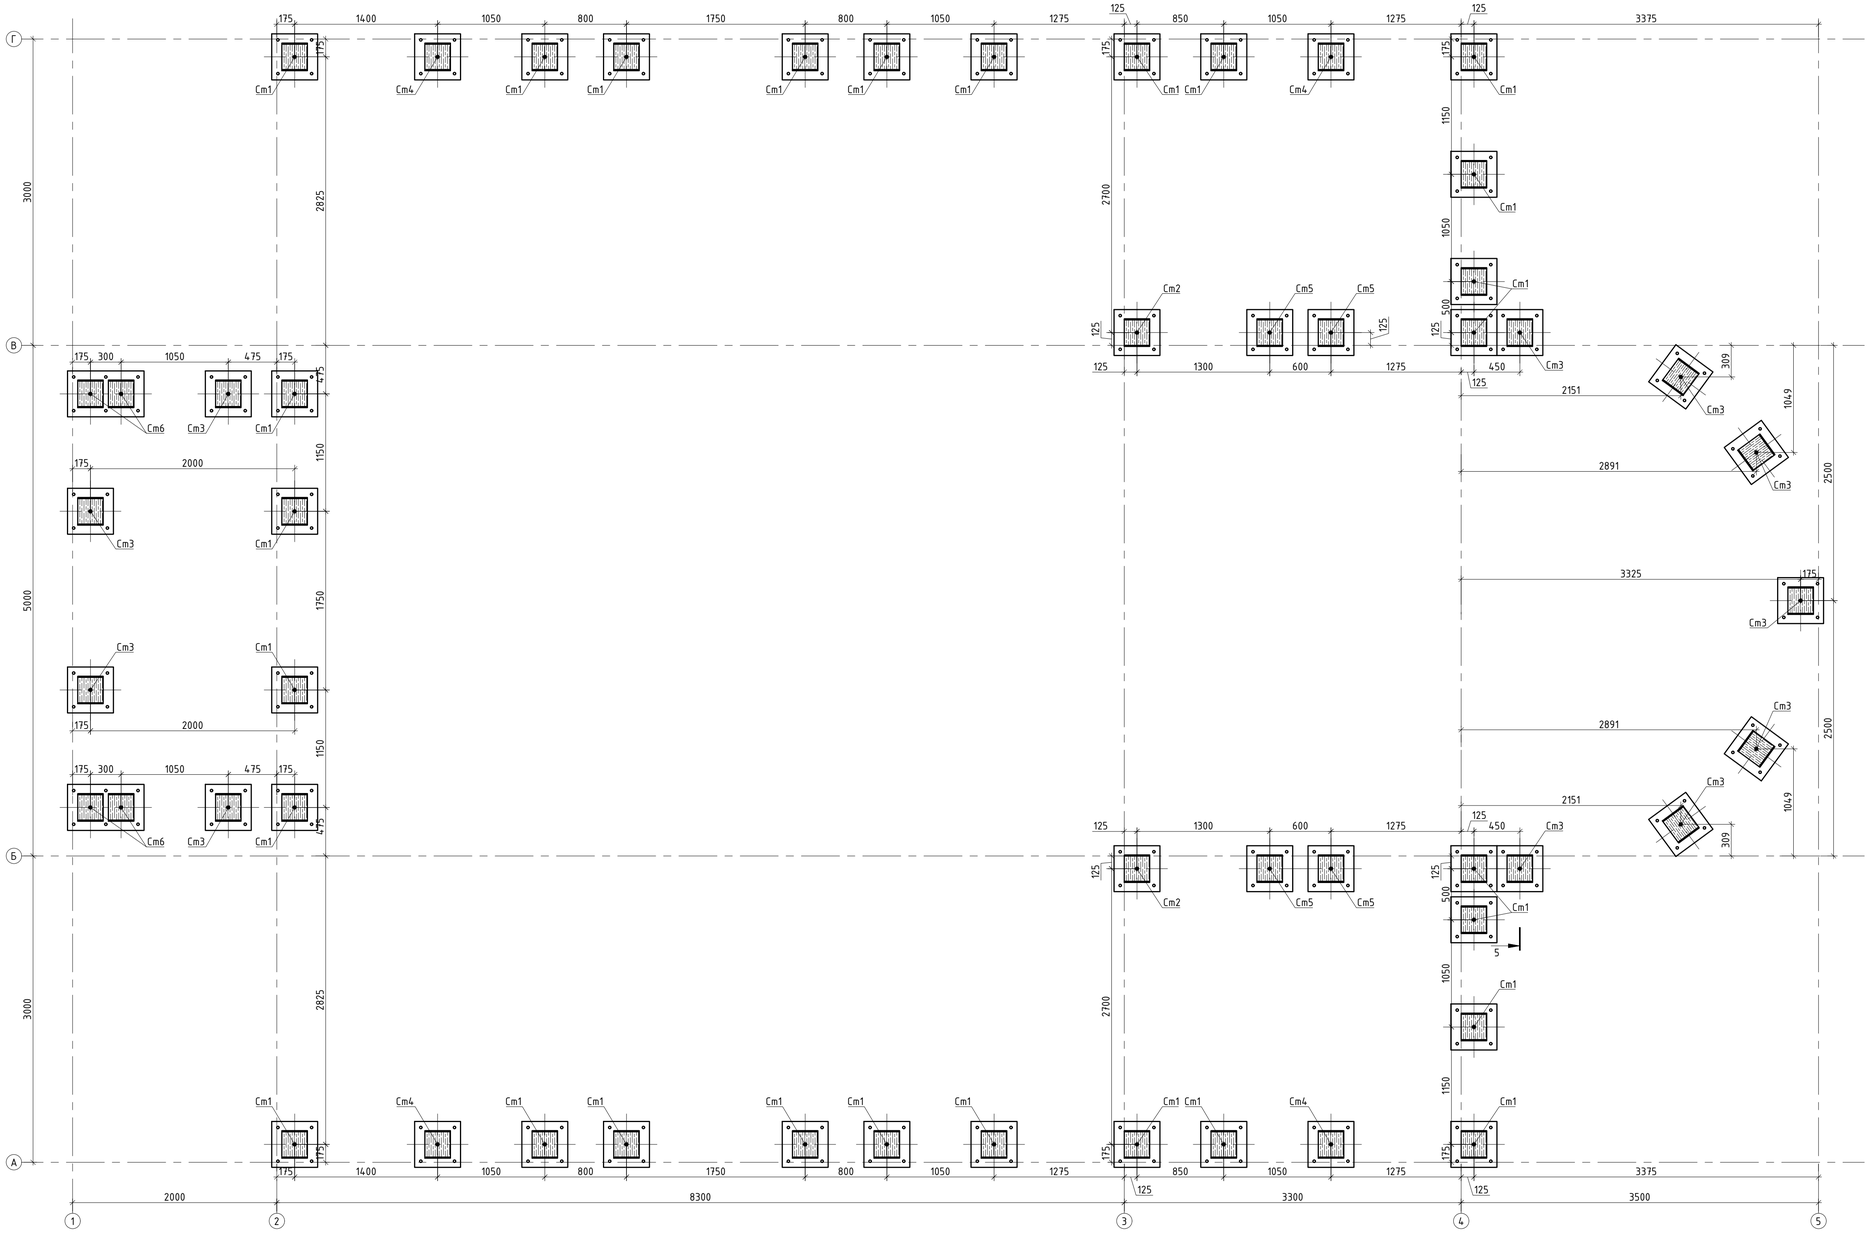

Спецификация

Поз.	Обозначение	Наименование	Кол.	Объем, м³	Итого, м³
Ст1	Стойка	250х250х3670	28	0,23	6,42
	База стойки	Тип 1	28		
Ст3	Стойка	250х250х2770	13	0,17	2,25
	База стойки	Тип 1	13		
Ст4	Стойка	250х250х3455	4	0,22	0,86
	База стойки	Тип 1	4		
Ст5	Стойка	250х250х3520	6	0,22	1,32
	База стойки	Тип 1	6		
Ст6	Стойка	250х250х2770	4	0,17	0,69
	База стойки	Тип 2	2		

Спецификация баз стоек

Тип	Внутри типа	A, мм	B, мм	t, мм	n, шт	Масса, кг	$n_{общ}$, шт	Масса общая, кг
Тип 1	Вертикальные (2 шт)	250	300	10	2	0,118	51	6,005
	Горизонтальный	450	450	10	1	0,159	51	8,107
Тип 2	Вертикальные (2 шт)	250	300	10	4	0,236	2	0,471
	Горизонтальный	750	450	10	1	0,265	2	0,530

Согласовано:

Взам. инв. №

Подп. и дата

Инв. № подл.

Изм.	Кол.уч.	Лист	№док	Подпись	Дата
Разработал		Андреев			06.26
Проверил		Бузина			06.26
Н.контр		Гусева			06.26
ГИП		Бузина			06.26

М16-КР

г.Санкт-Петербург, Митрофаньевское шоссе, участок 16,
(западнее дома 13, литера Д по Малой Митрофаньевской улице)


Благоустройство территории

Стадия	Лист	Листов
П	9	

Часовня.
Схема расположения стоек на отм. -0,030

ООО "Домус"
г. Санкт-Петербург

Схема расположения стоек (1:30)

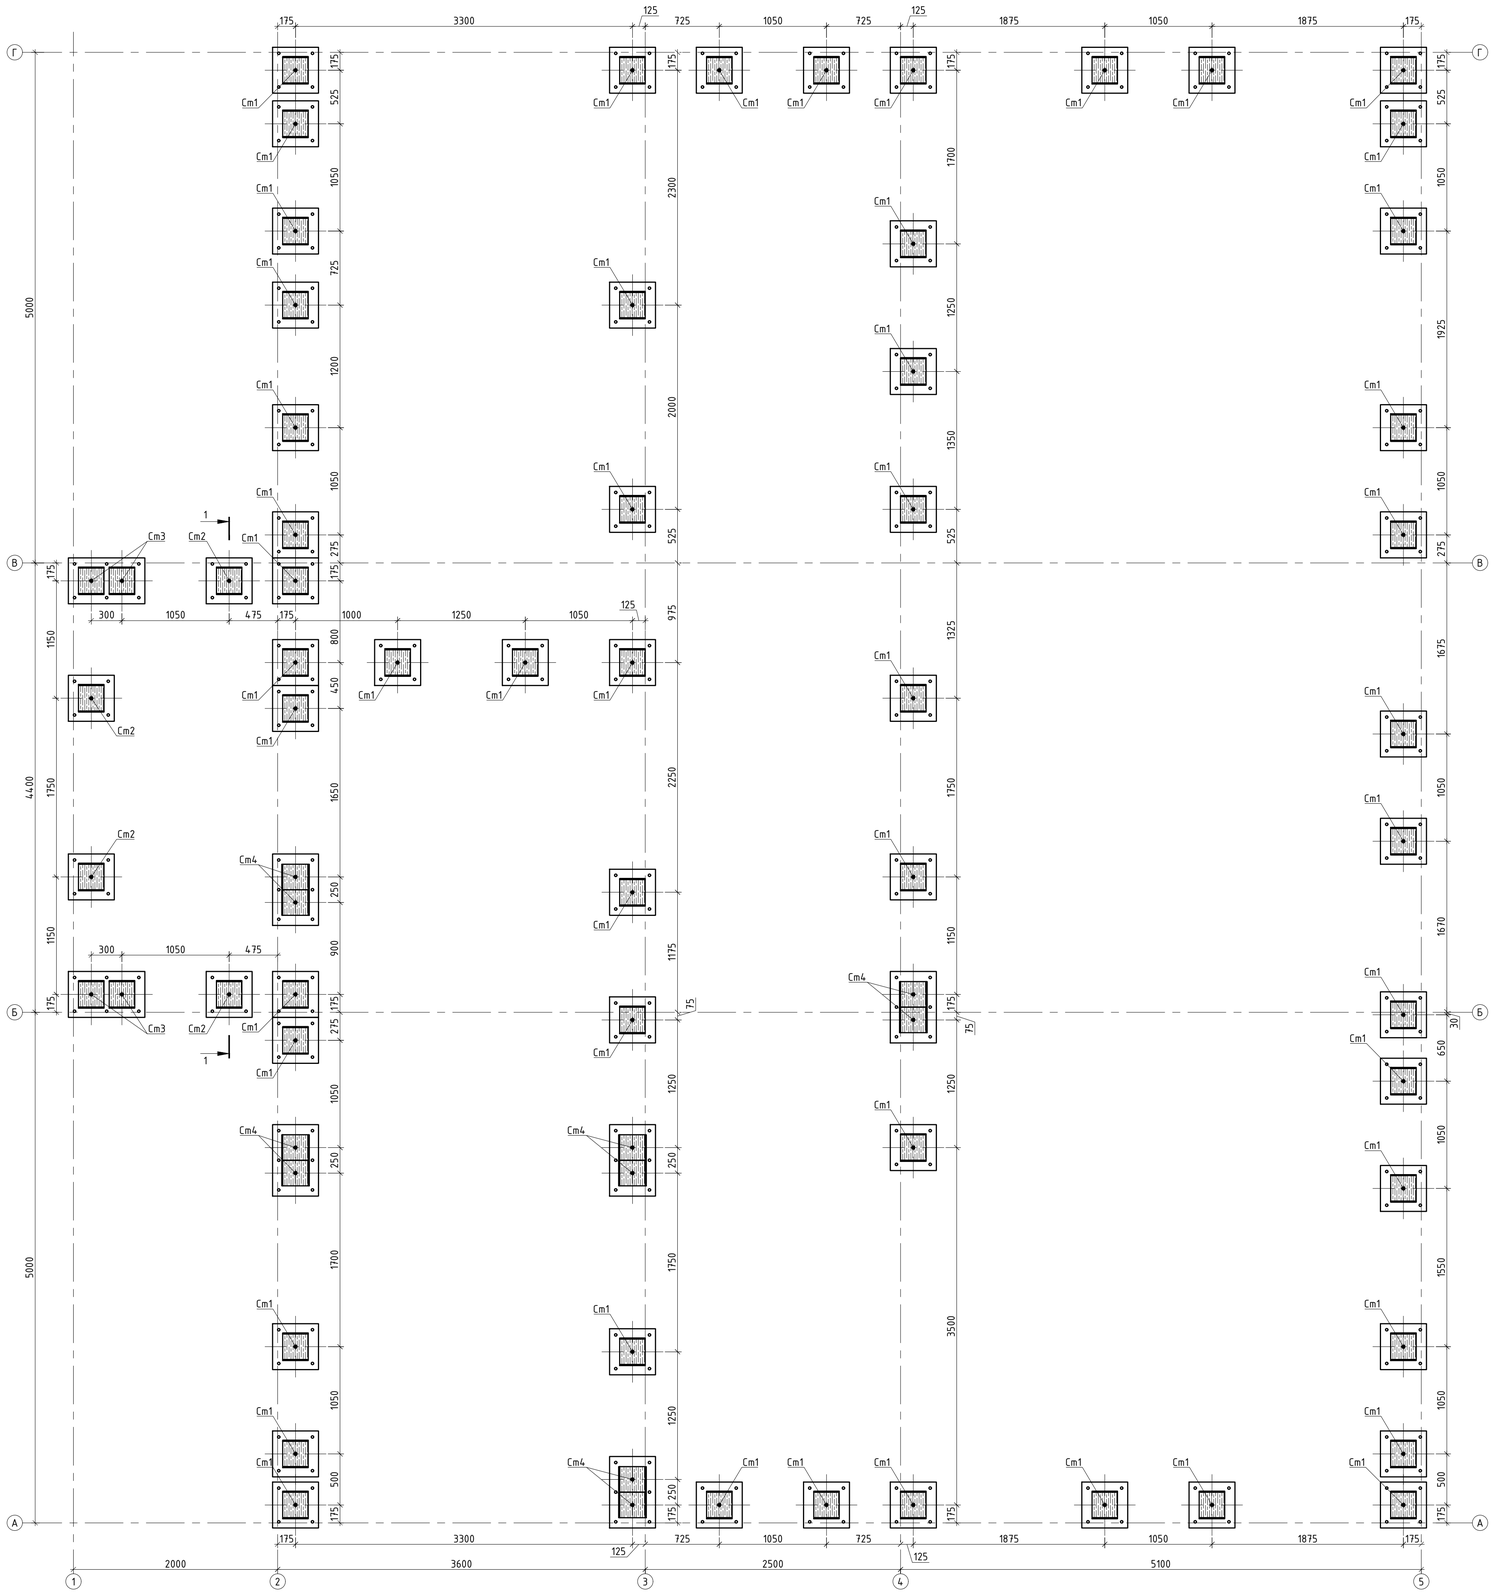

Спецификация элементов бытового сооружения

Поз.	Обозначение	Наименование	Кол.	Объем, м³	Итого, м³
Ст1	Стойка	250х250х3770	52	0,24	12,25
	База стойки	Тип 1	52		
Ст2	Стойка	250х250х2770	4	0,17	0,69
	База стойки	Тип 1	4		
Ст3	Стойка	250х250х2770	4	0,17	0,69
	База стойки	Тип 2	2		
Ст4	Стойка	250х250х3770	10	0,24	2,36
	База стойки	Тип 3	5		

Спецификация баз стоек

Тип	Внутри типа	A, мм	B, мм	t, мм	n, шт	Масса, кг	$n_{\Sigma,шт}$, шт	Масса общая, кг
Тип 1	Вертикальные (2 шт)	250	300	10	2	0,118	56	6,594
	Горизантальный	450	450	10	1	0,159		8,902
Тип 2	Вертикальные (2 шт)	250	300	10	4	0,236	2	0,471
	Горизантальный	750	450	10	1	0,265		0,530
Тип 3	Вертикальные (2 шт)	250	300	10	4	0,236	5	1,178
	Горизантальный	750	450	10	1	0,265		1,325

Согласовано:

Взам. инв. №

Подп. и дата

Инв. № подл.

Изм.	Кол.уч.	Лист	№док.	Подпись	Дата
Разработал		Андреев			06.26
Проверил		Бузина			06.26
Н.контр		Гусева			06.26
ГИП		Бузина			06.26

М16-КР

г.Санкт-Петербург, Митрофаньевское шоссе, участок 16, (западнее дома 13, литера Д по Малой Митрофаньевской улице)

Благоустройство территории

Стадия	Лист	Листов
П	10	

Бытовое здание.
Схема расположения стоек на отм. -0,030

ООО "Домус"
г. Санкт-Петербург